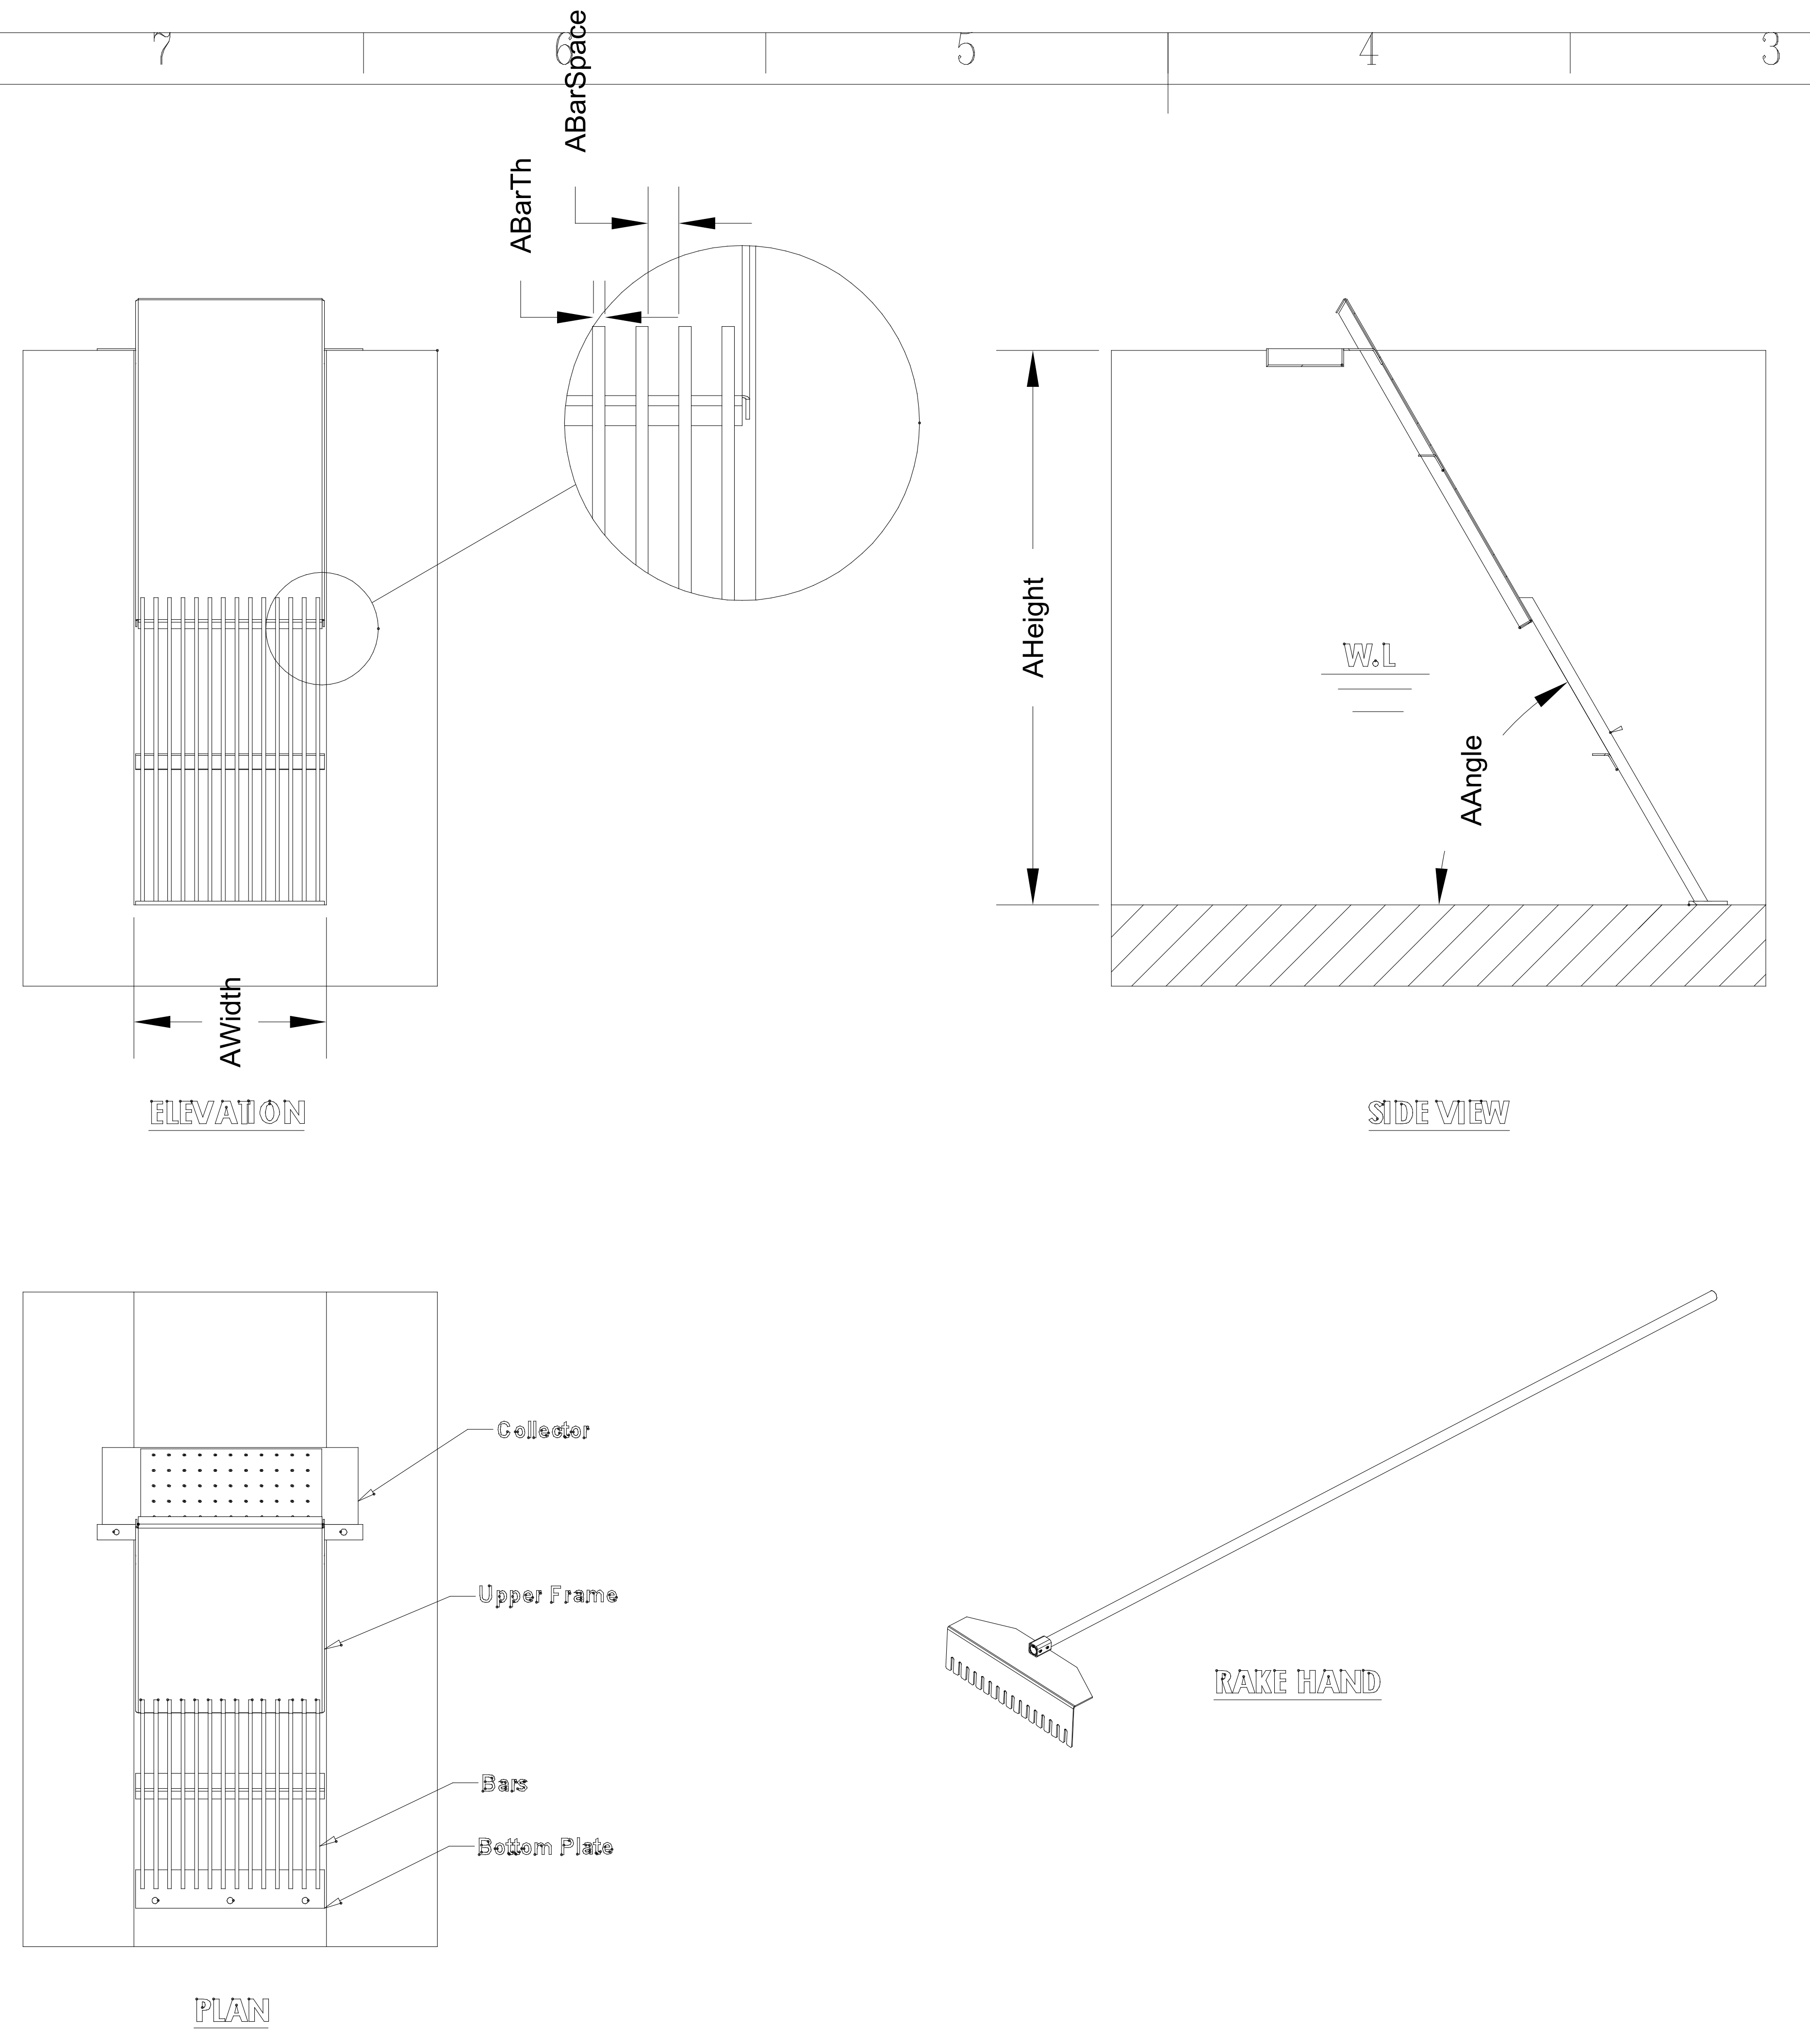

REV.NO.	DATE	ZONE	REVISION	BY.	APPVD.

General Description

Service	: Inlet Area
Type	: Bar Coarse Screen
Channel Depth	: 1500
Channel Width	: 600
Water Depth	: 500
Bar Section	: 12 x 50
Bar Spacing	: 25
Inclination Angle	: 60°
Material	: St.St. 304
Qty	: 1
Dimensions	: All Dimensions in mm

General Tolerance According to DIN 7168-M

APPVD.	W.A		
CHKD.	W.F		
DRAWN	D.M	17/04/2024	
OWNER:	National Organization For Potable Water and Sanitary Drainage "NOPWASD"		
CONSULTANT:			
MAIN CONTRACTOR:			
Client	VA TECH WABAG		
CIVIL CONTRACTOR:			
MANUFACTURER:	The Integrated Environmental Technologies and OilServices Co. S.A.E. 5,Heliopolis Company Bldg. Block No. [illegible] Tel : +02 [illegible] , +02 [illegible] Behind Sheraton Heliopolis Hotel, Airport Road, Cairo, Egypt Fax : +02 [illegible] P.O.Box : 2472 Cairo [illegible] E-mail : [illegible]		
PROJECT:	Delga WWTP – Capacity 15000 m3/day El Fashn Center – Beni Suif Governorate		
TITLE:	Manual Screen (General Assembly)		
DWG NO.		SIZE	A3
SCALE	1:10	SHEET	1 OF 1
WELD:			

THIS DRAWING IS FOR OFFER PURPOSE ONLY AND MAY BE CHANGED DURING FABRICATION .