
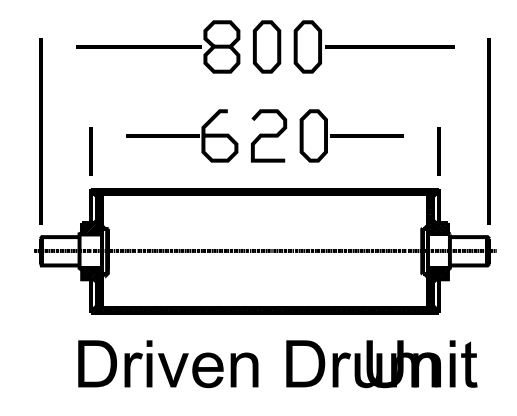
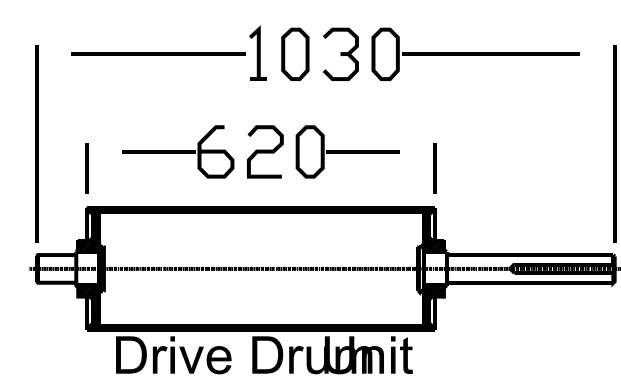
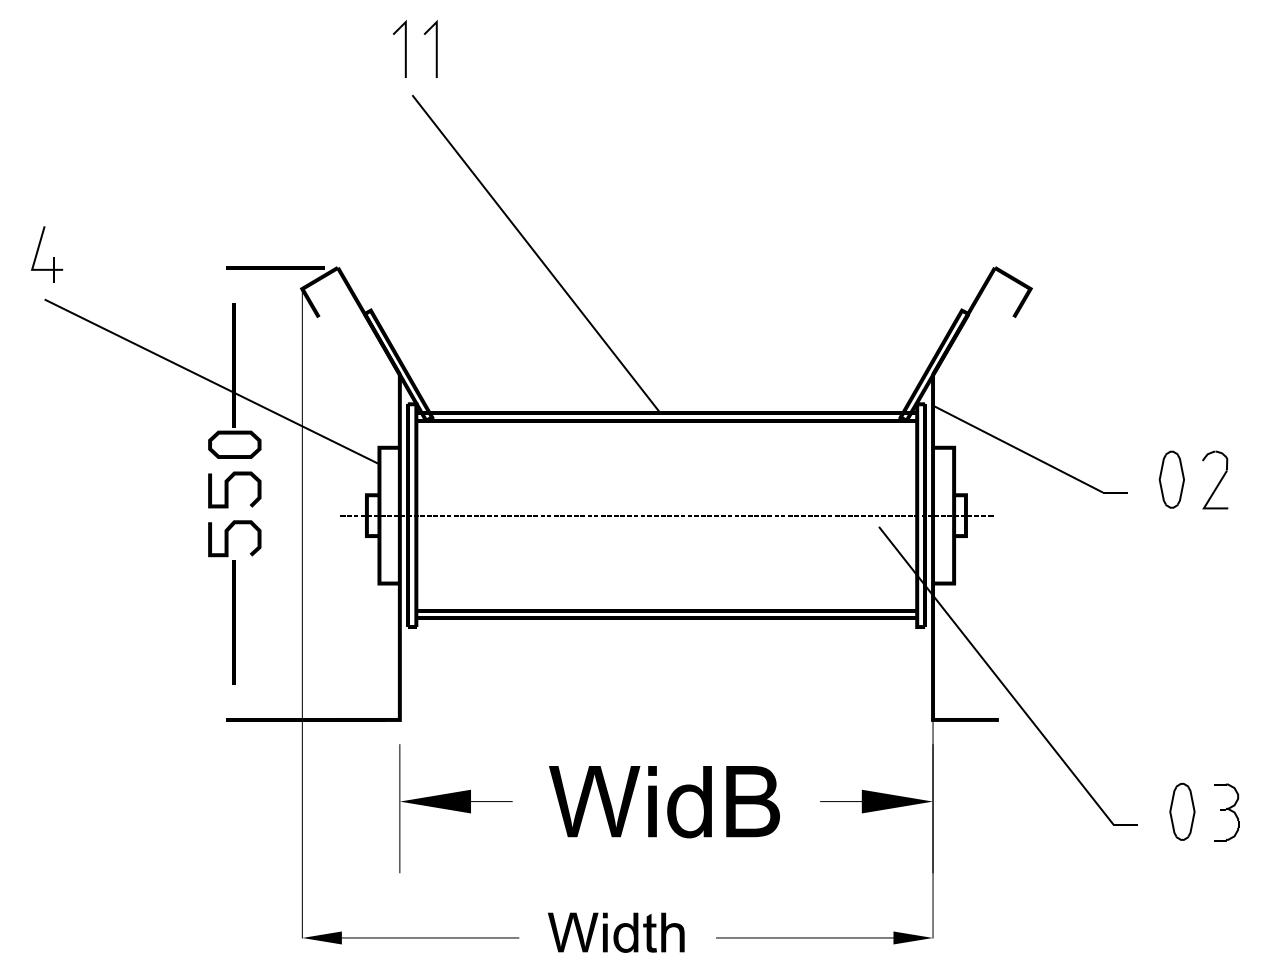
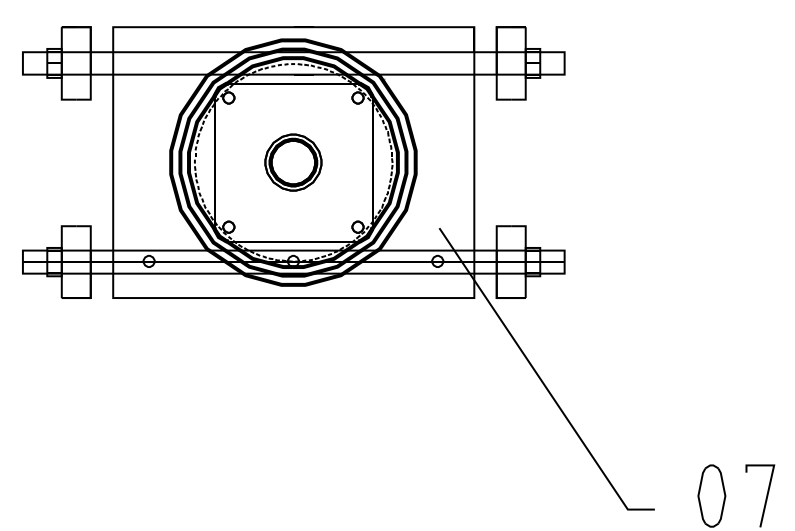
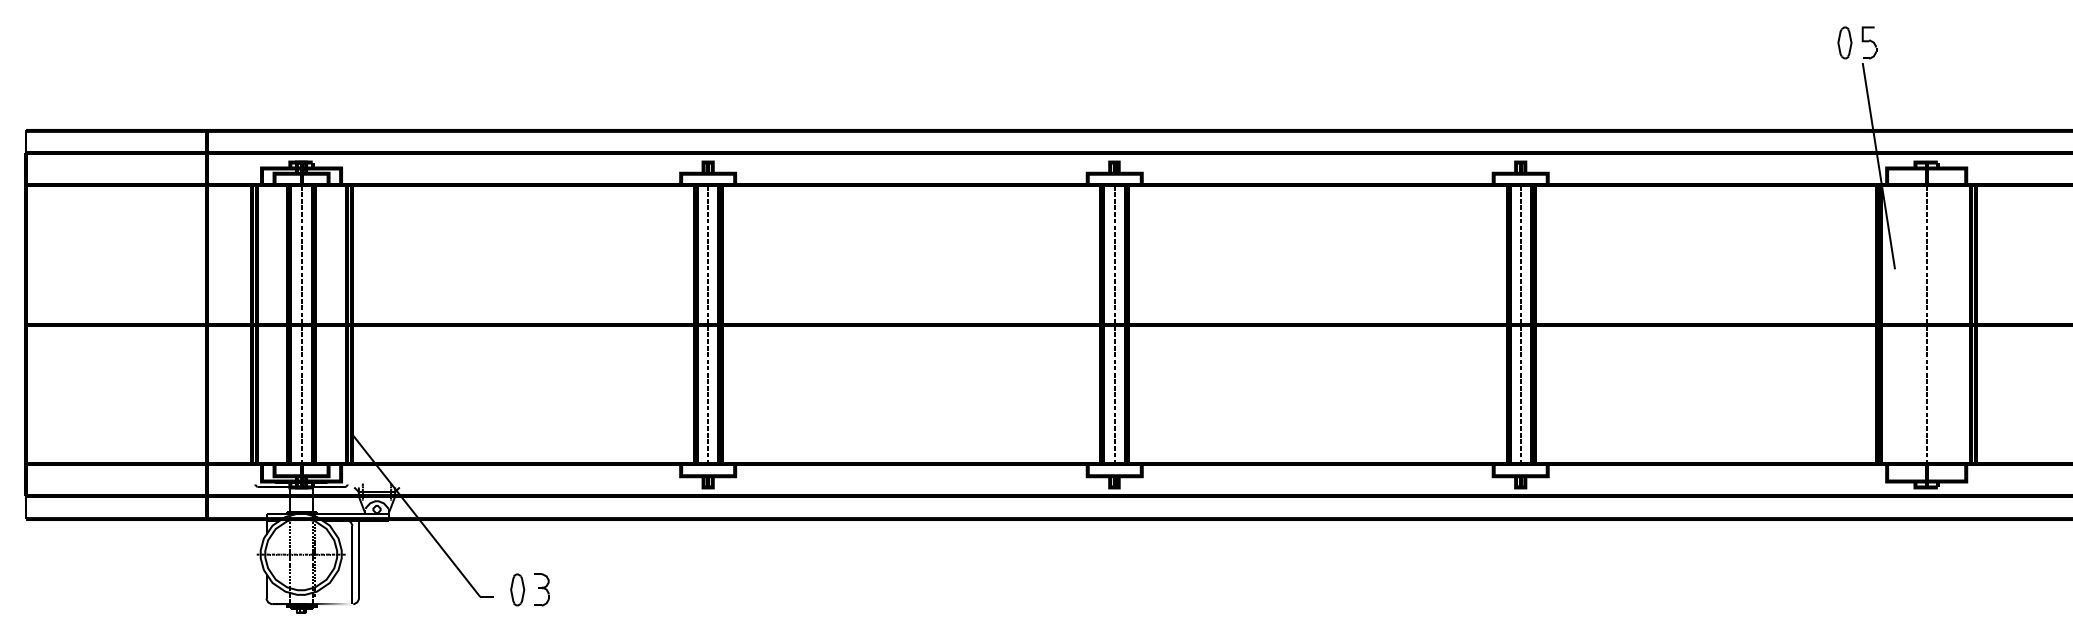


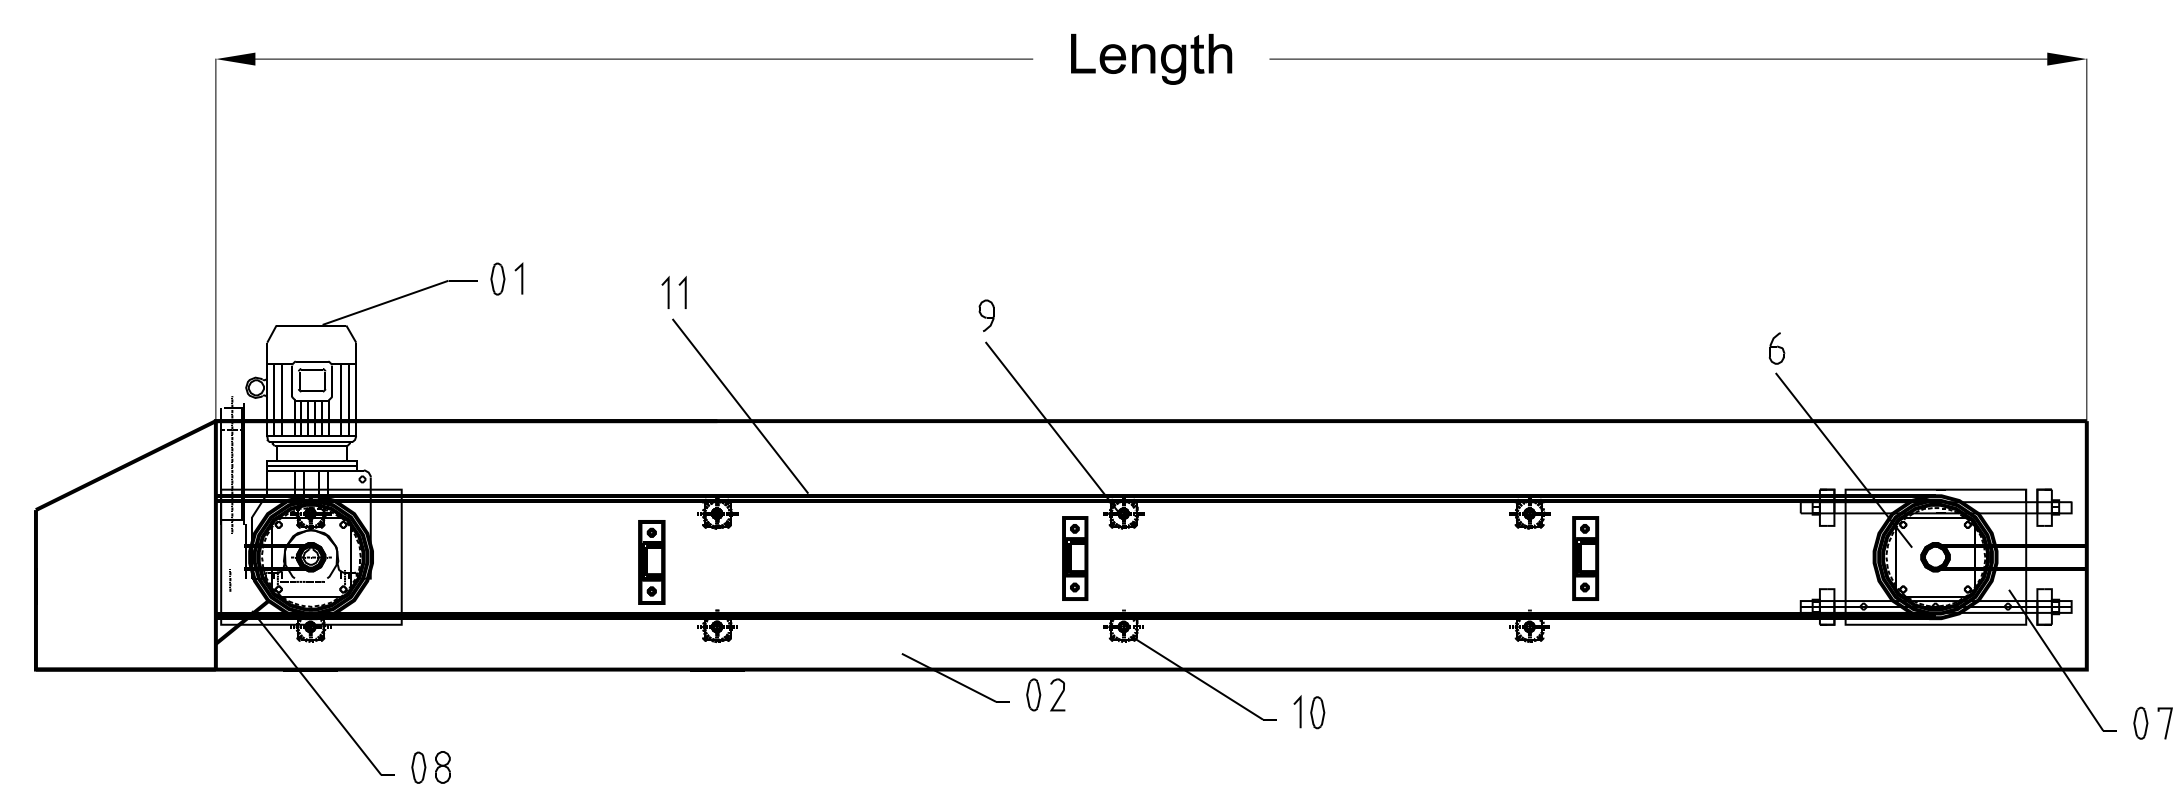

TURN KEY CONTRACTORS:				
Z.C.E		ELZABRAA		
AUTOSATRAD ROAD _ ARAB ABO SAAD _ CAIRO _ EGYPT				
elzabaraa.sag2014@gmail.com				
TITALE				
Belt conveyor				
SCALE	REF. DWG. NO.		SIZE	REV.
DRAWN	PREPARED	CHECKED	APPROVED	DATE
K.T	A.S	A.S	S.MICHAEL	