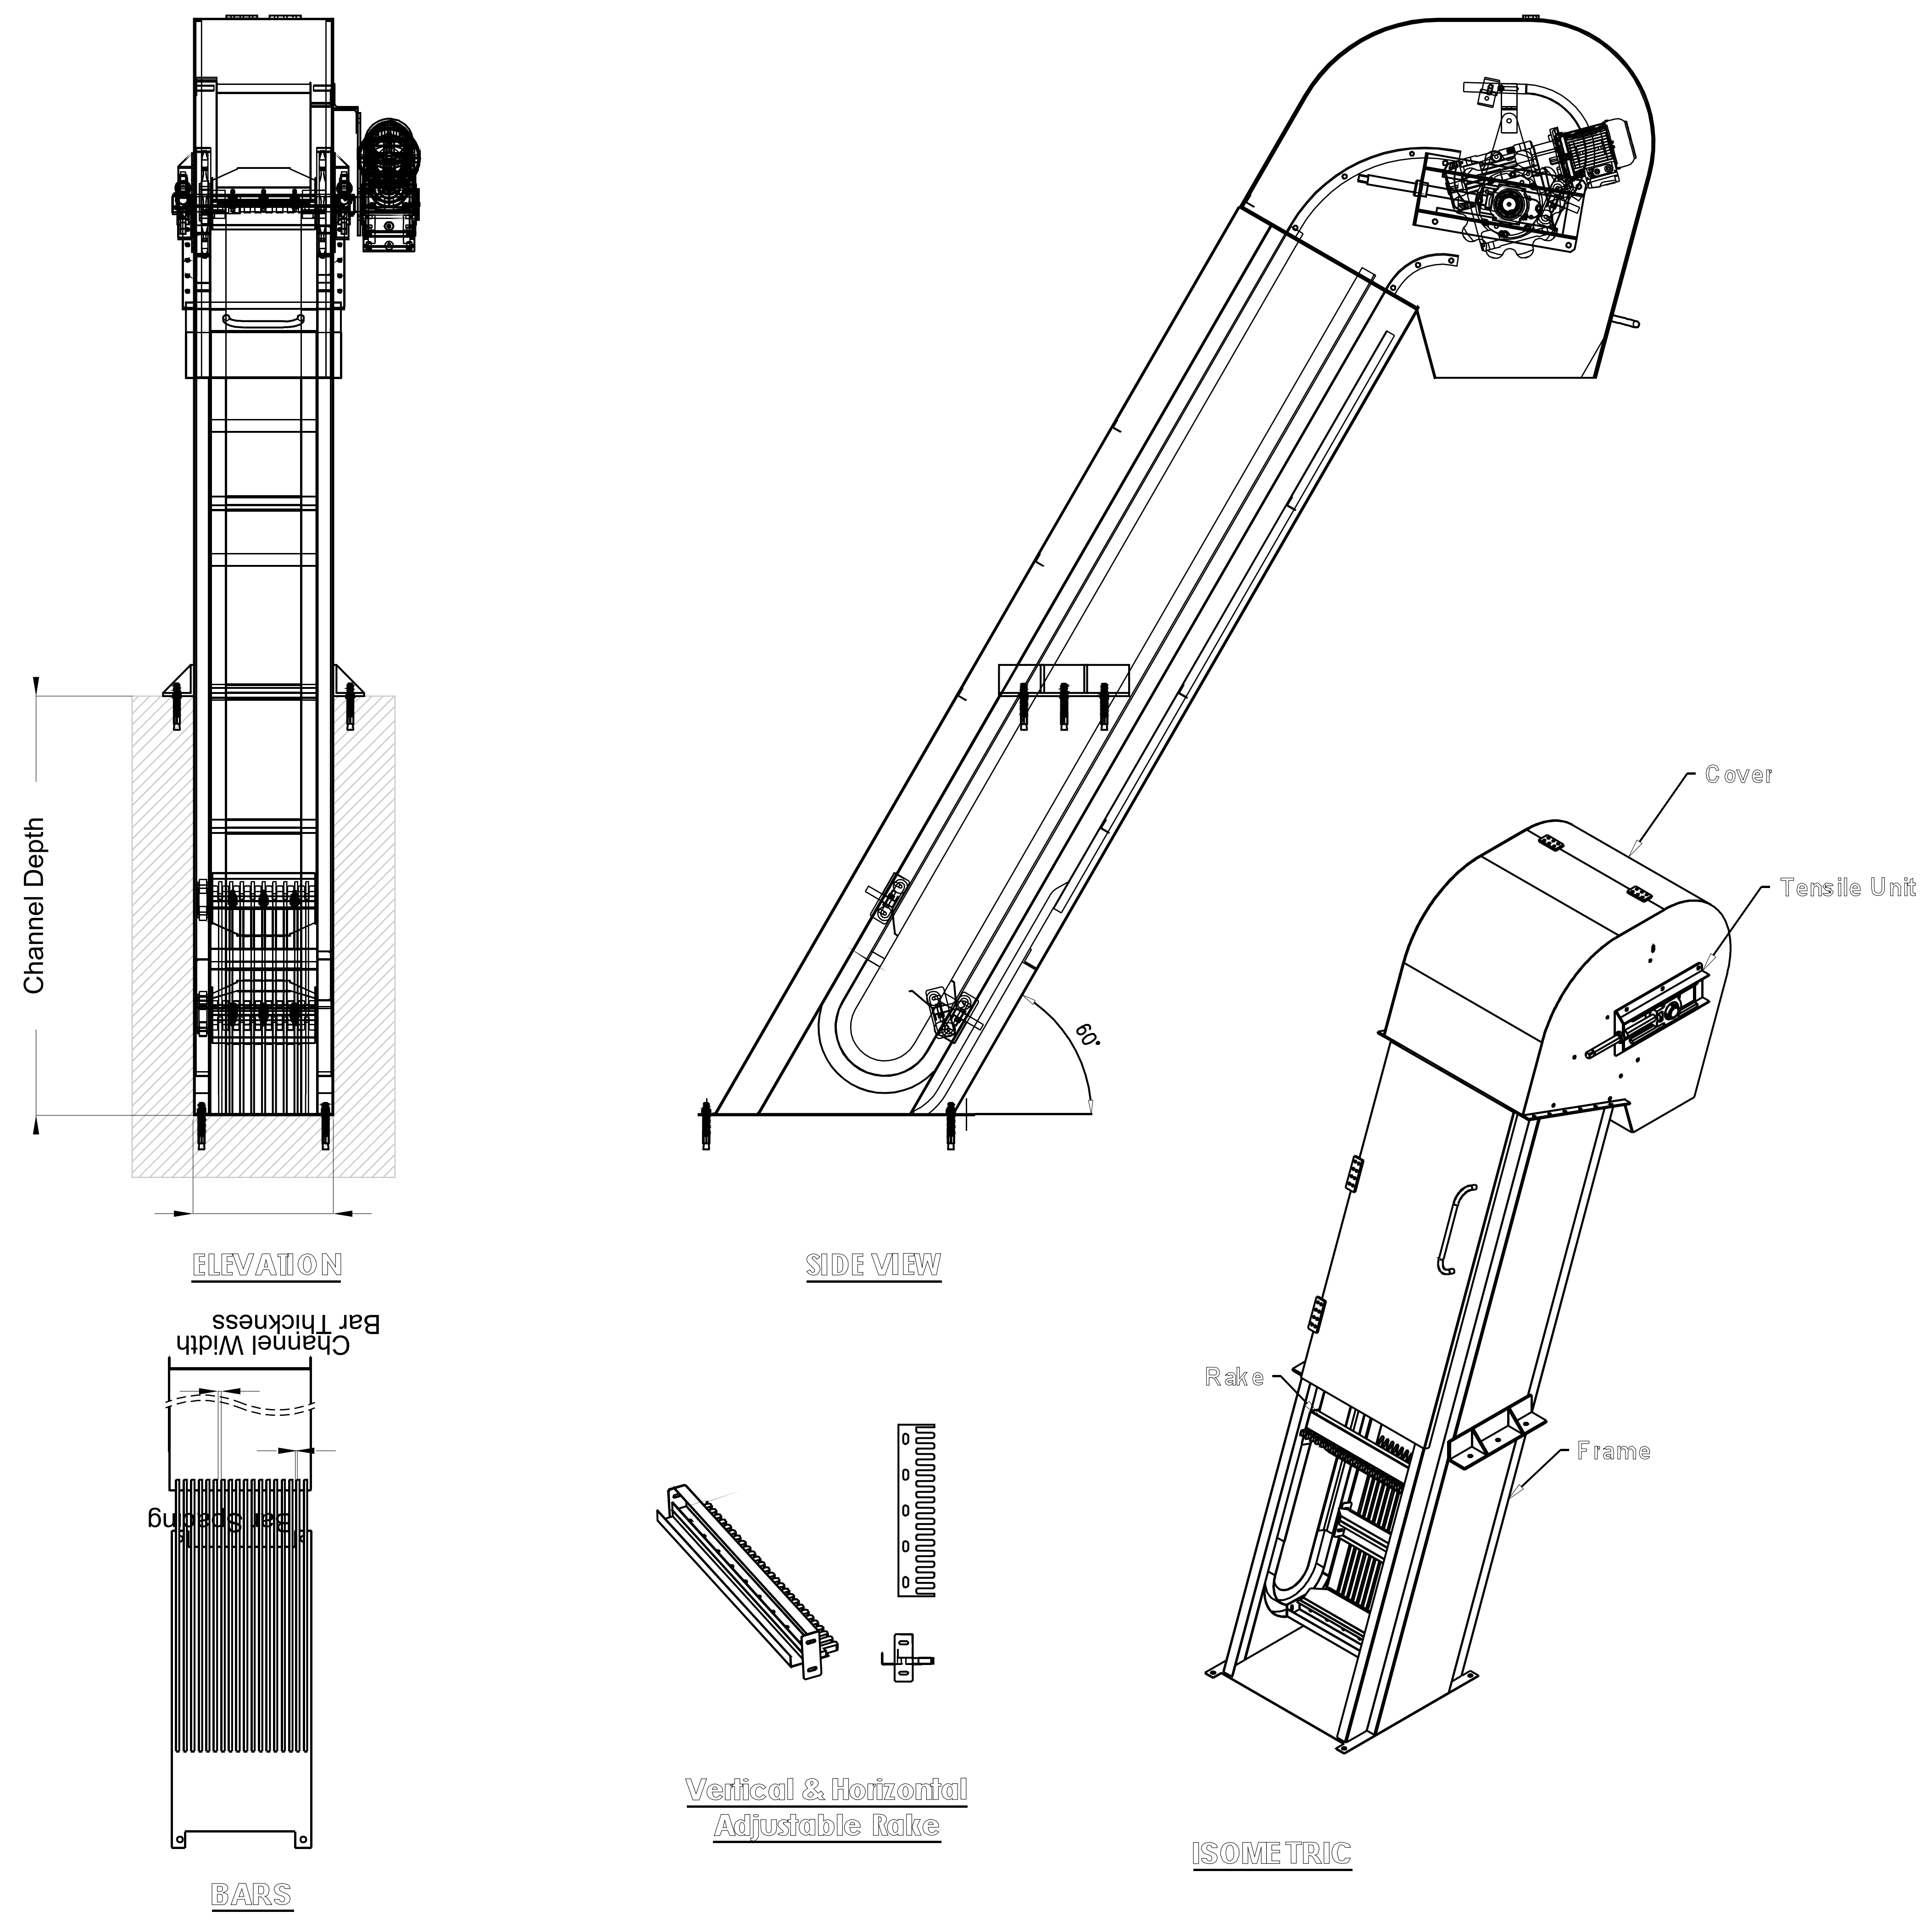

REV.NO.	DATE	ZONE	REVISION	BY.	APPVD.

General Description

Service	: Inlet Area
Type	:Mechanical Coarse Screen Multi rake
Channel Depth	: 1500
Channel Width	: 600
Water Depth	: 500
Bar Section	: 12 x 50
Bar Spacing	: 15
Inclination Angle	: 60°
Material	: St.St. 304
Qty	: 3
Dimensions	: All Dimensions in mm

General Tolerance According to DIN 7168-M

THIS DRAWING IS FOR OFFER PURPOSE ONLY AND MAY BE CHANGED DURING FABRICATION .

APPVD.	W.A		
CHKD.	W.F		
DRAWN	D.M	01/09/2024	
OWNER:	National Organization For Potable Water and Sanitary Drainage "NOPWASD"		
CONSULTANT:			
MAIN CONTRACTOR:			
Client	VA TECH WABAG		
CIVIL CONTRACTOR:			
MANUFACTURER:	The Integrated Environmental Technologies and OilServices Co. S.A.E. 5,Heliopolis Company Bldg. Block No. 1226 Behind Sheraton Heliopolis Hotel, Airport Road. Cairo, Egypt P.O.Box : 2472 Ciaro 11361 Tel : + 02 22684645 , + 02 22689689 Fax : + 02 22675150 E-mail : ietos@ietos.com		
PROJECT:	Delga WWTP – Capacity 15000 m3/day El Fashn Center – Beni Suif Governorate		
TITLE:	Mechanical Screen (General Assembly)		
DWG NO.		SIZE	A3
SCALE	1:10	SHEET	1 OF 1
WELD:			