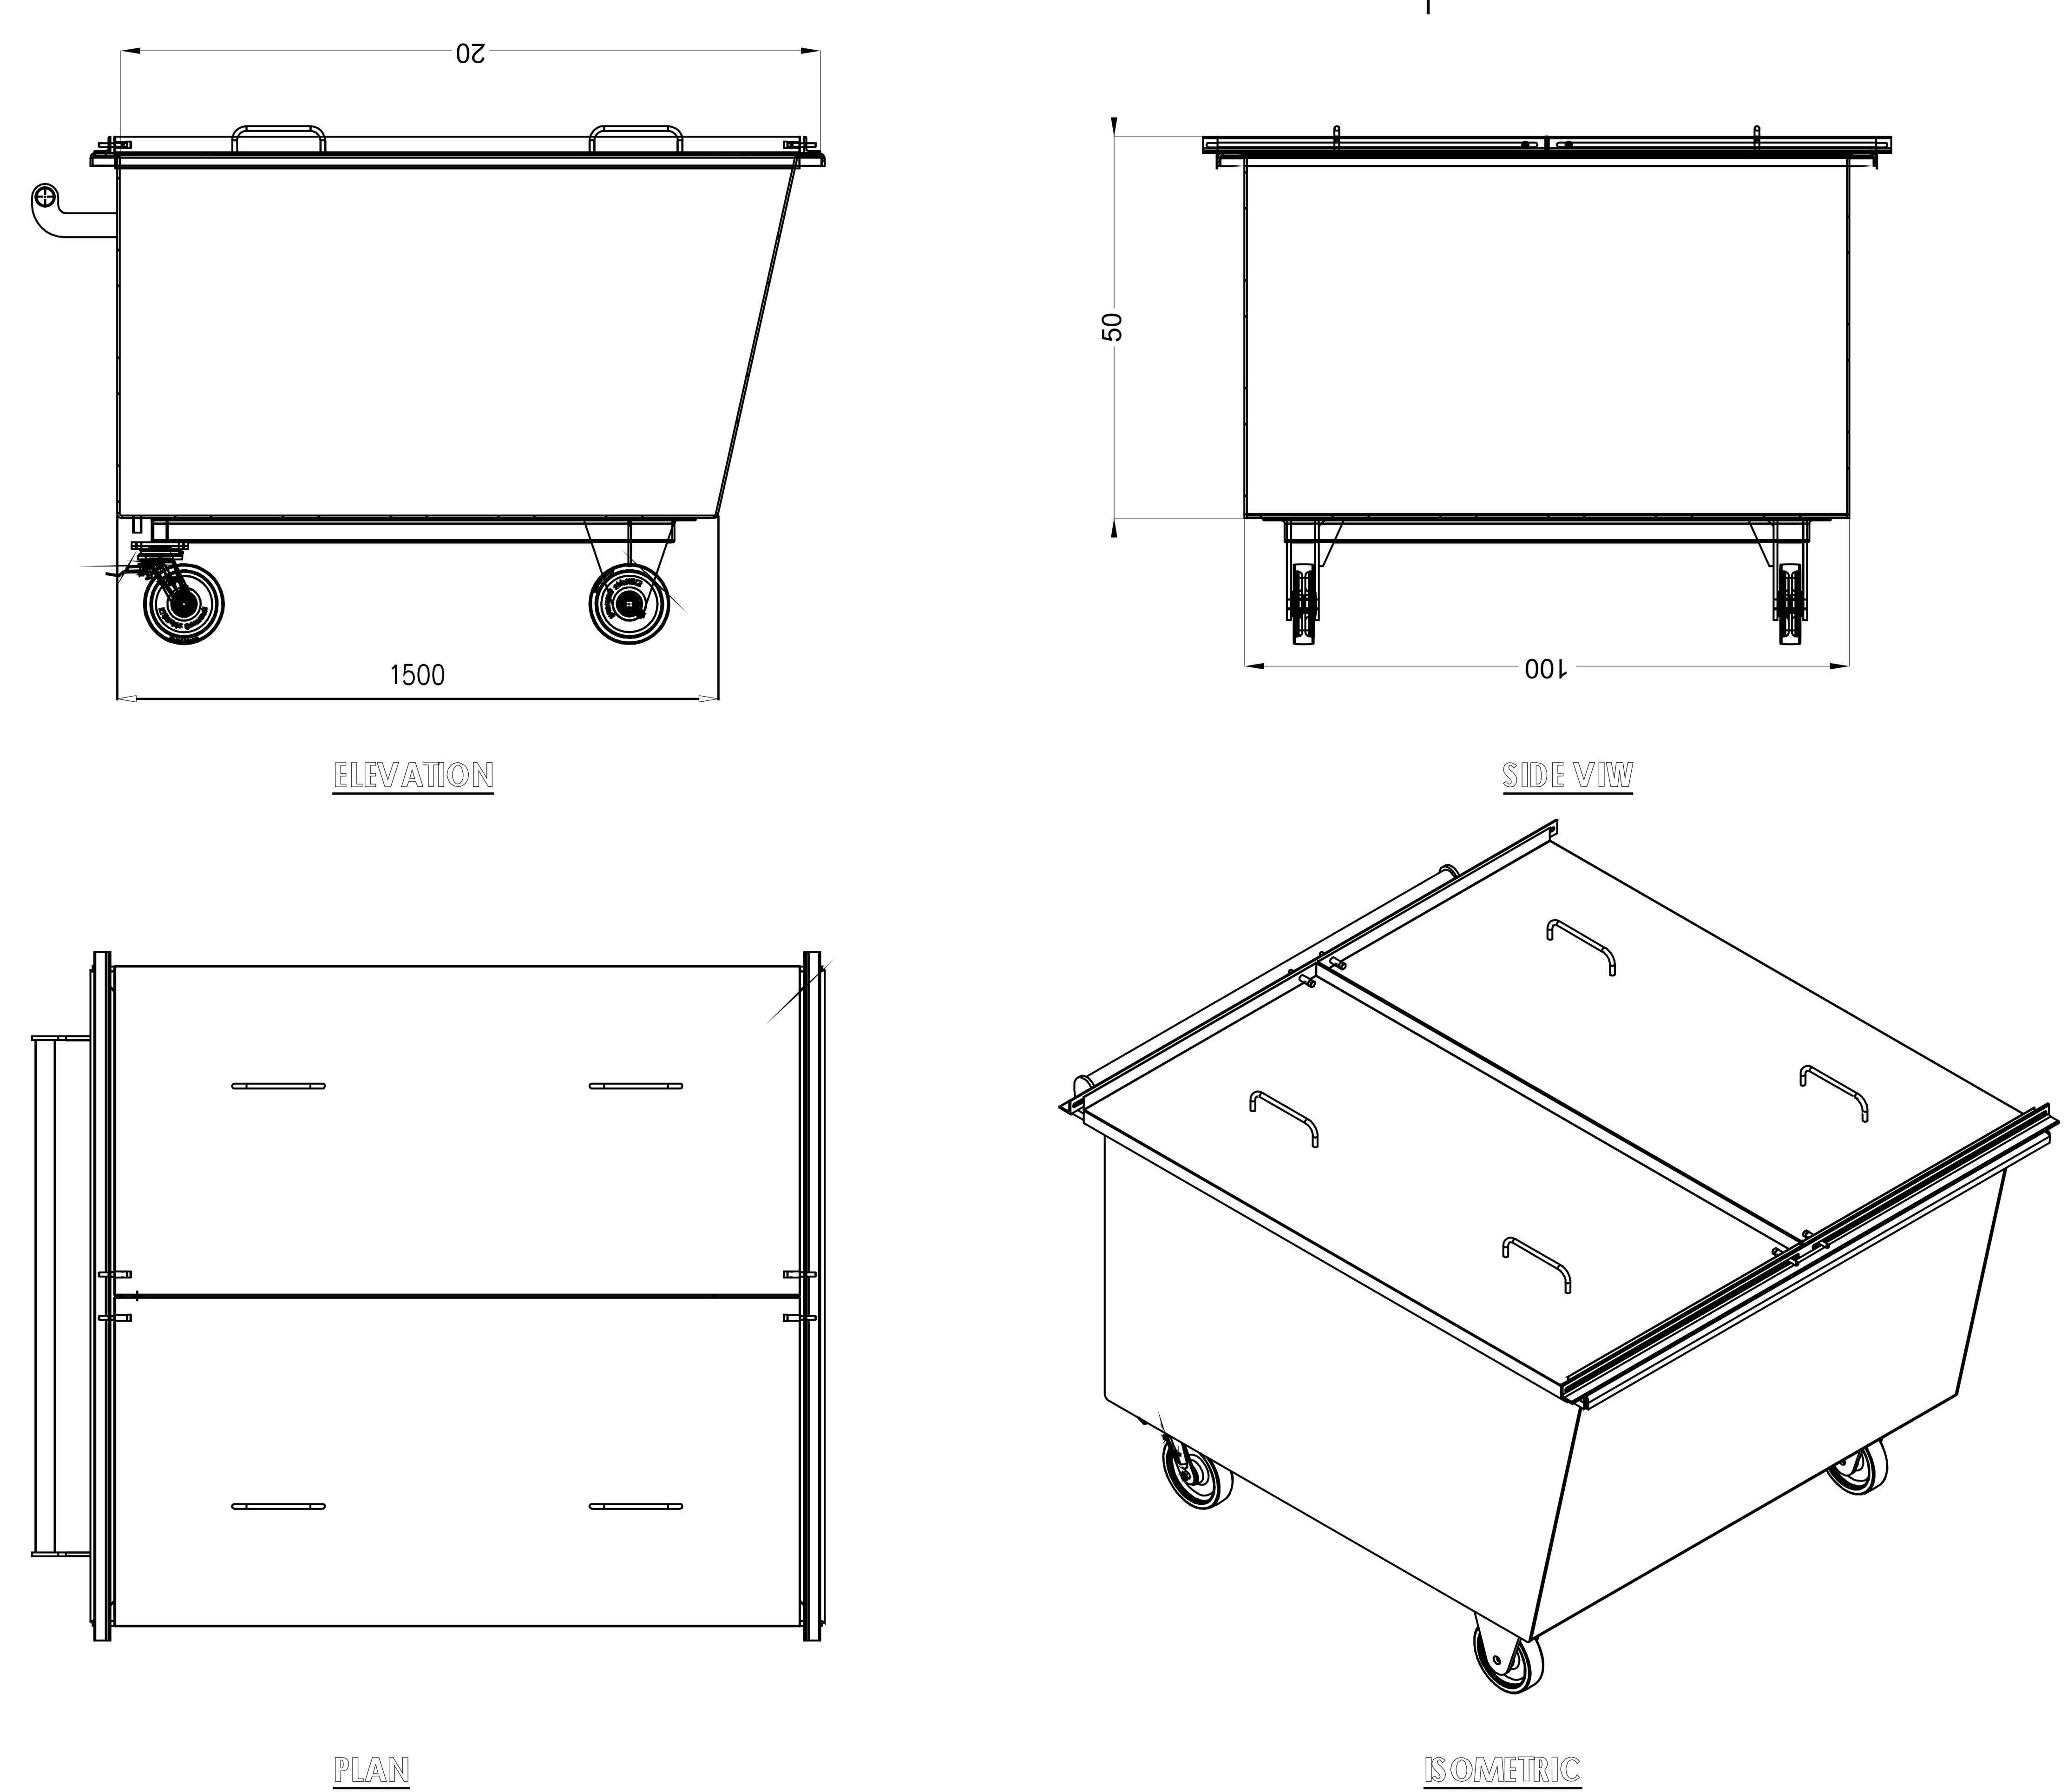

REV.NO.	DATE	ZONE	REVISION	BY.	APPVD.

General Description

Type	: Collecting Box with Cover
Capacity	: 2 m3
Length	: 1700
Width	: 1500
Height	: 900
Thickness	: 6
Materail	: Epoxy Coated St. 37

Qty. 2

All Dimensions in mm

GENERAL TOLERANCE ACC. TO DIN 7168-m

WELDING ACC. TO AWS D9.1

THIS DRAWING IS FOR OFFER PURPOSE ONLY AND MAY BE CHANGED DURING FABRICATION .

APPVD.	W.A		
CHKD.	W.F		
DRAWN	D.M	17/04/2024	
OWNER:	National Organization For Potable Water and Sanitary Drainage "NOPWASD"		
CONSULTANT:			
MAIN CONTRACTOR:			
Client	VA TECH WABAG		
CIVIL CONTRACTOR:			
MANUFACTURER:	The Integrated Environmental Technologies and OilServices Co. S.A.E. 5,Heliopolis Company Bldg. Block No. 1226 Behind Sheraton Heliopolis Hotel, Airport Road. Cairo, Egypt P.O.Box : 2472 Claro 11361 Tel : + 02 22694645 , + 02 22689889 Fax : + 02 22675150 E-mail : ietos@ietos.com		
PROJECT:	Delga WWTP – Capacity 15000 m3/day El Fashn Center – Beni Suif Governorate		
TITLE:	Container (Collecting Box) (General Assembly)		
DWG NO.		SIZE	A3
SCALE	1:10	SHEET	1 OF 1
WELD:			