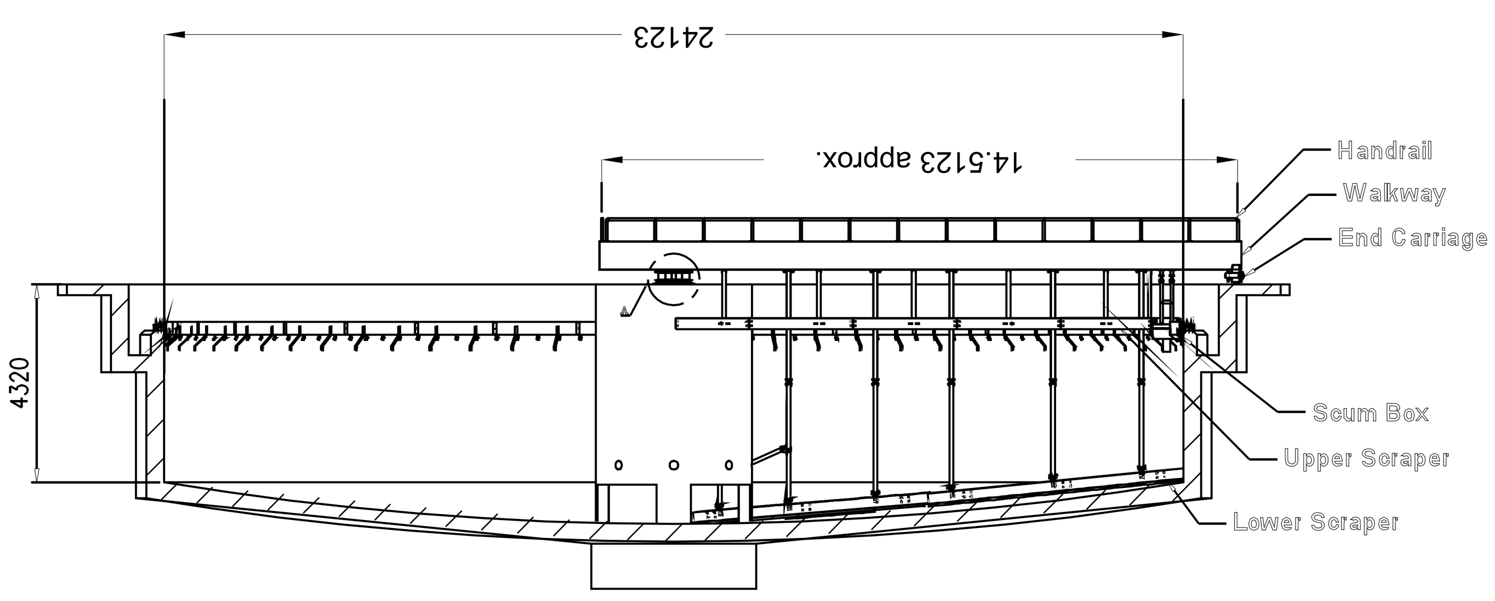

SECTION A-A

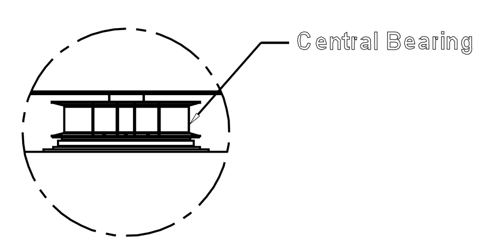

DETAIL A

General Description

Type :Rotating Half Scraper Bridge

Service :Final SettlingTank

Operation :Electrical Motor

Bridge Length :14600 mm Approx.

Dimension :All Dim. in MM

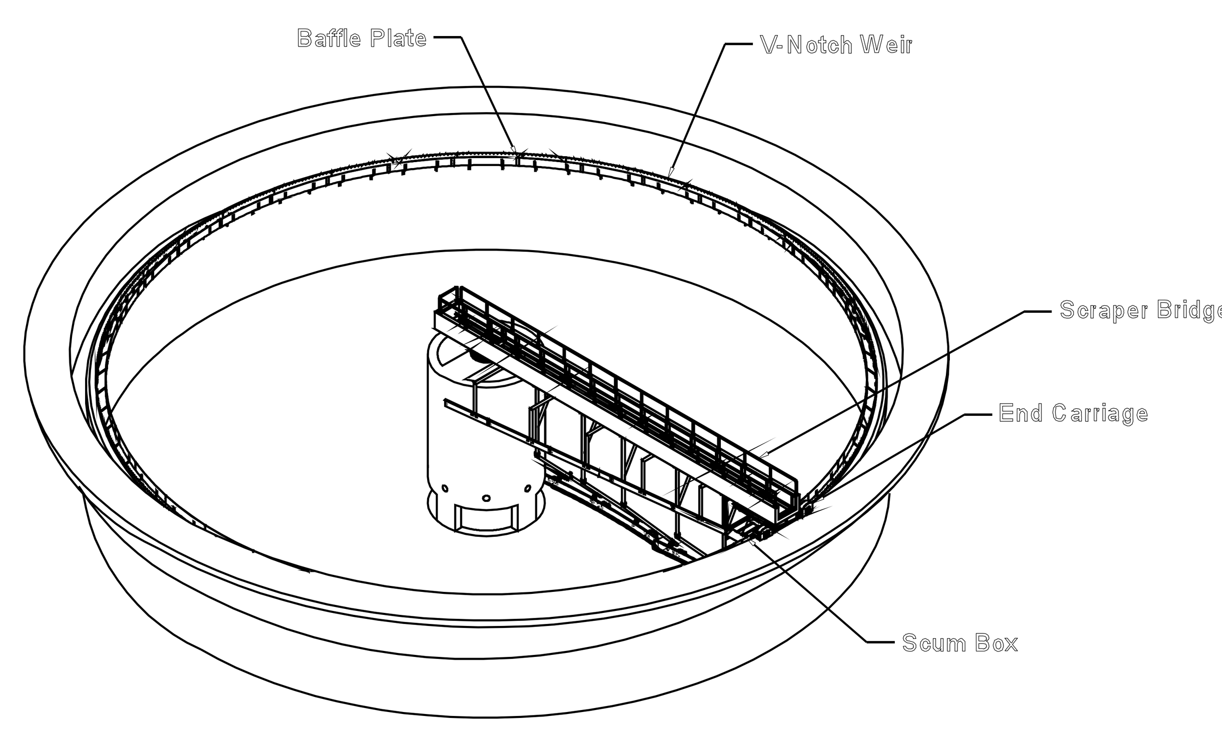

ISOMETRIC

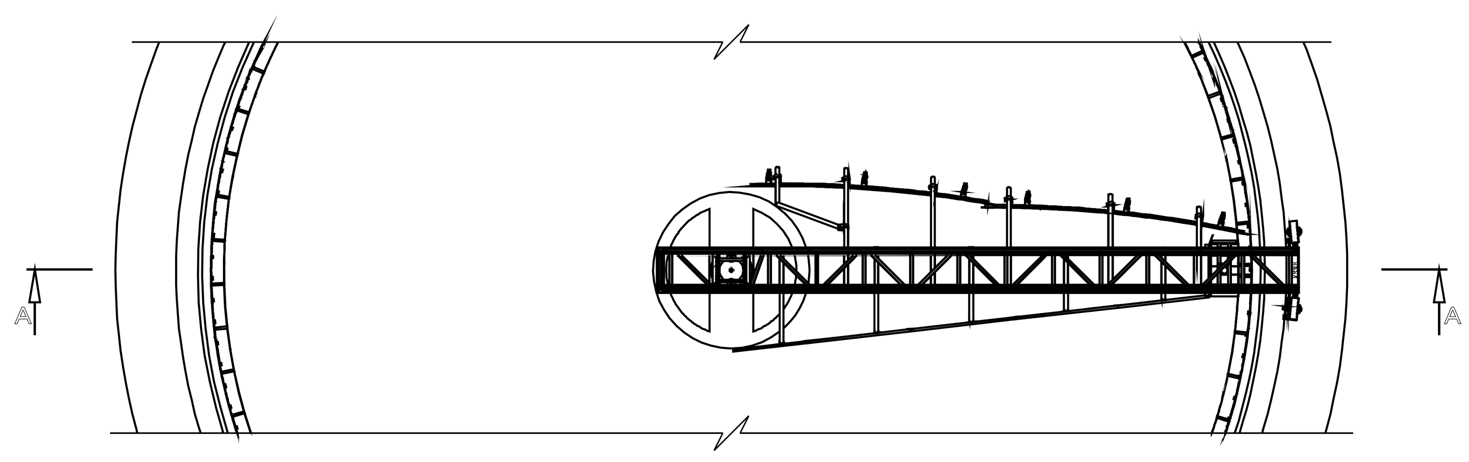

PLAN VIEW

REV.NO.	DATE	ZONE	REVISION	BY.	APPVD.

APPVD.	W.A	
CHKD.	W.F	
DRAWN	D.M	24/03/2024
OWNER:	National Organization For Potable Water and Sanitary Drainage "NOPWASD"	
CONSULTANT:		
MAIN CONTRACTOR:		
Client	VA TECH WABAG	
CIVIL CONTRACTOR:		
MANUFACTURER:	The Integrated Environmental Technologies and OilServices Co. S.A.E. 5,Heliopolis Company Bldg. Block No. 1226 Behind Sheraton Heliopolis Hotel, Airport Road. Cairo, Egypt P.O.Box : 2472 Claro 11361 Tel : + 02 22684645 , + 02 22689889 Fax : + 02 22675150 E-mail : ietos@ietos.com	
PROJECT:	Delga WWTP – Capacity 15000 m3/day El Fashn Center – Beni Suif Governorate	
TITLE:	Scraper Bridge (General Assembly)	

DWG NO.		SIZE	A3
SCALE	1:10	SHEET	1 OF 1
WELD:			

THIS DRAWING IS FOR OFFER PURPOSE ONLY AND MAY BE CHANGED DURING FABRICATION .