


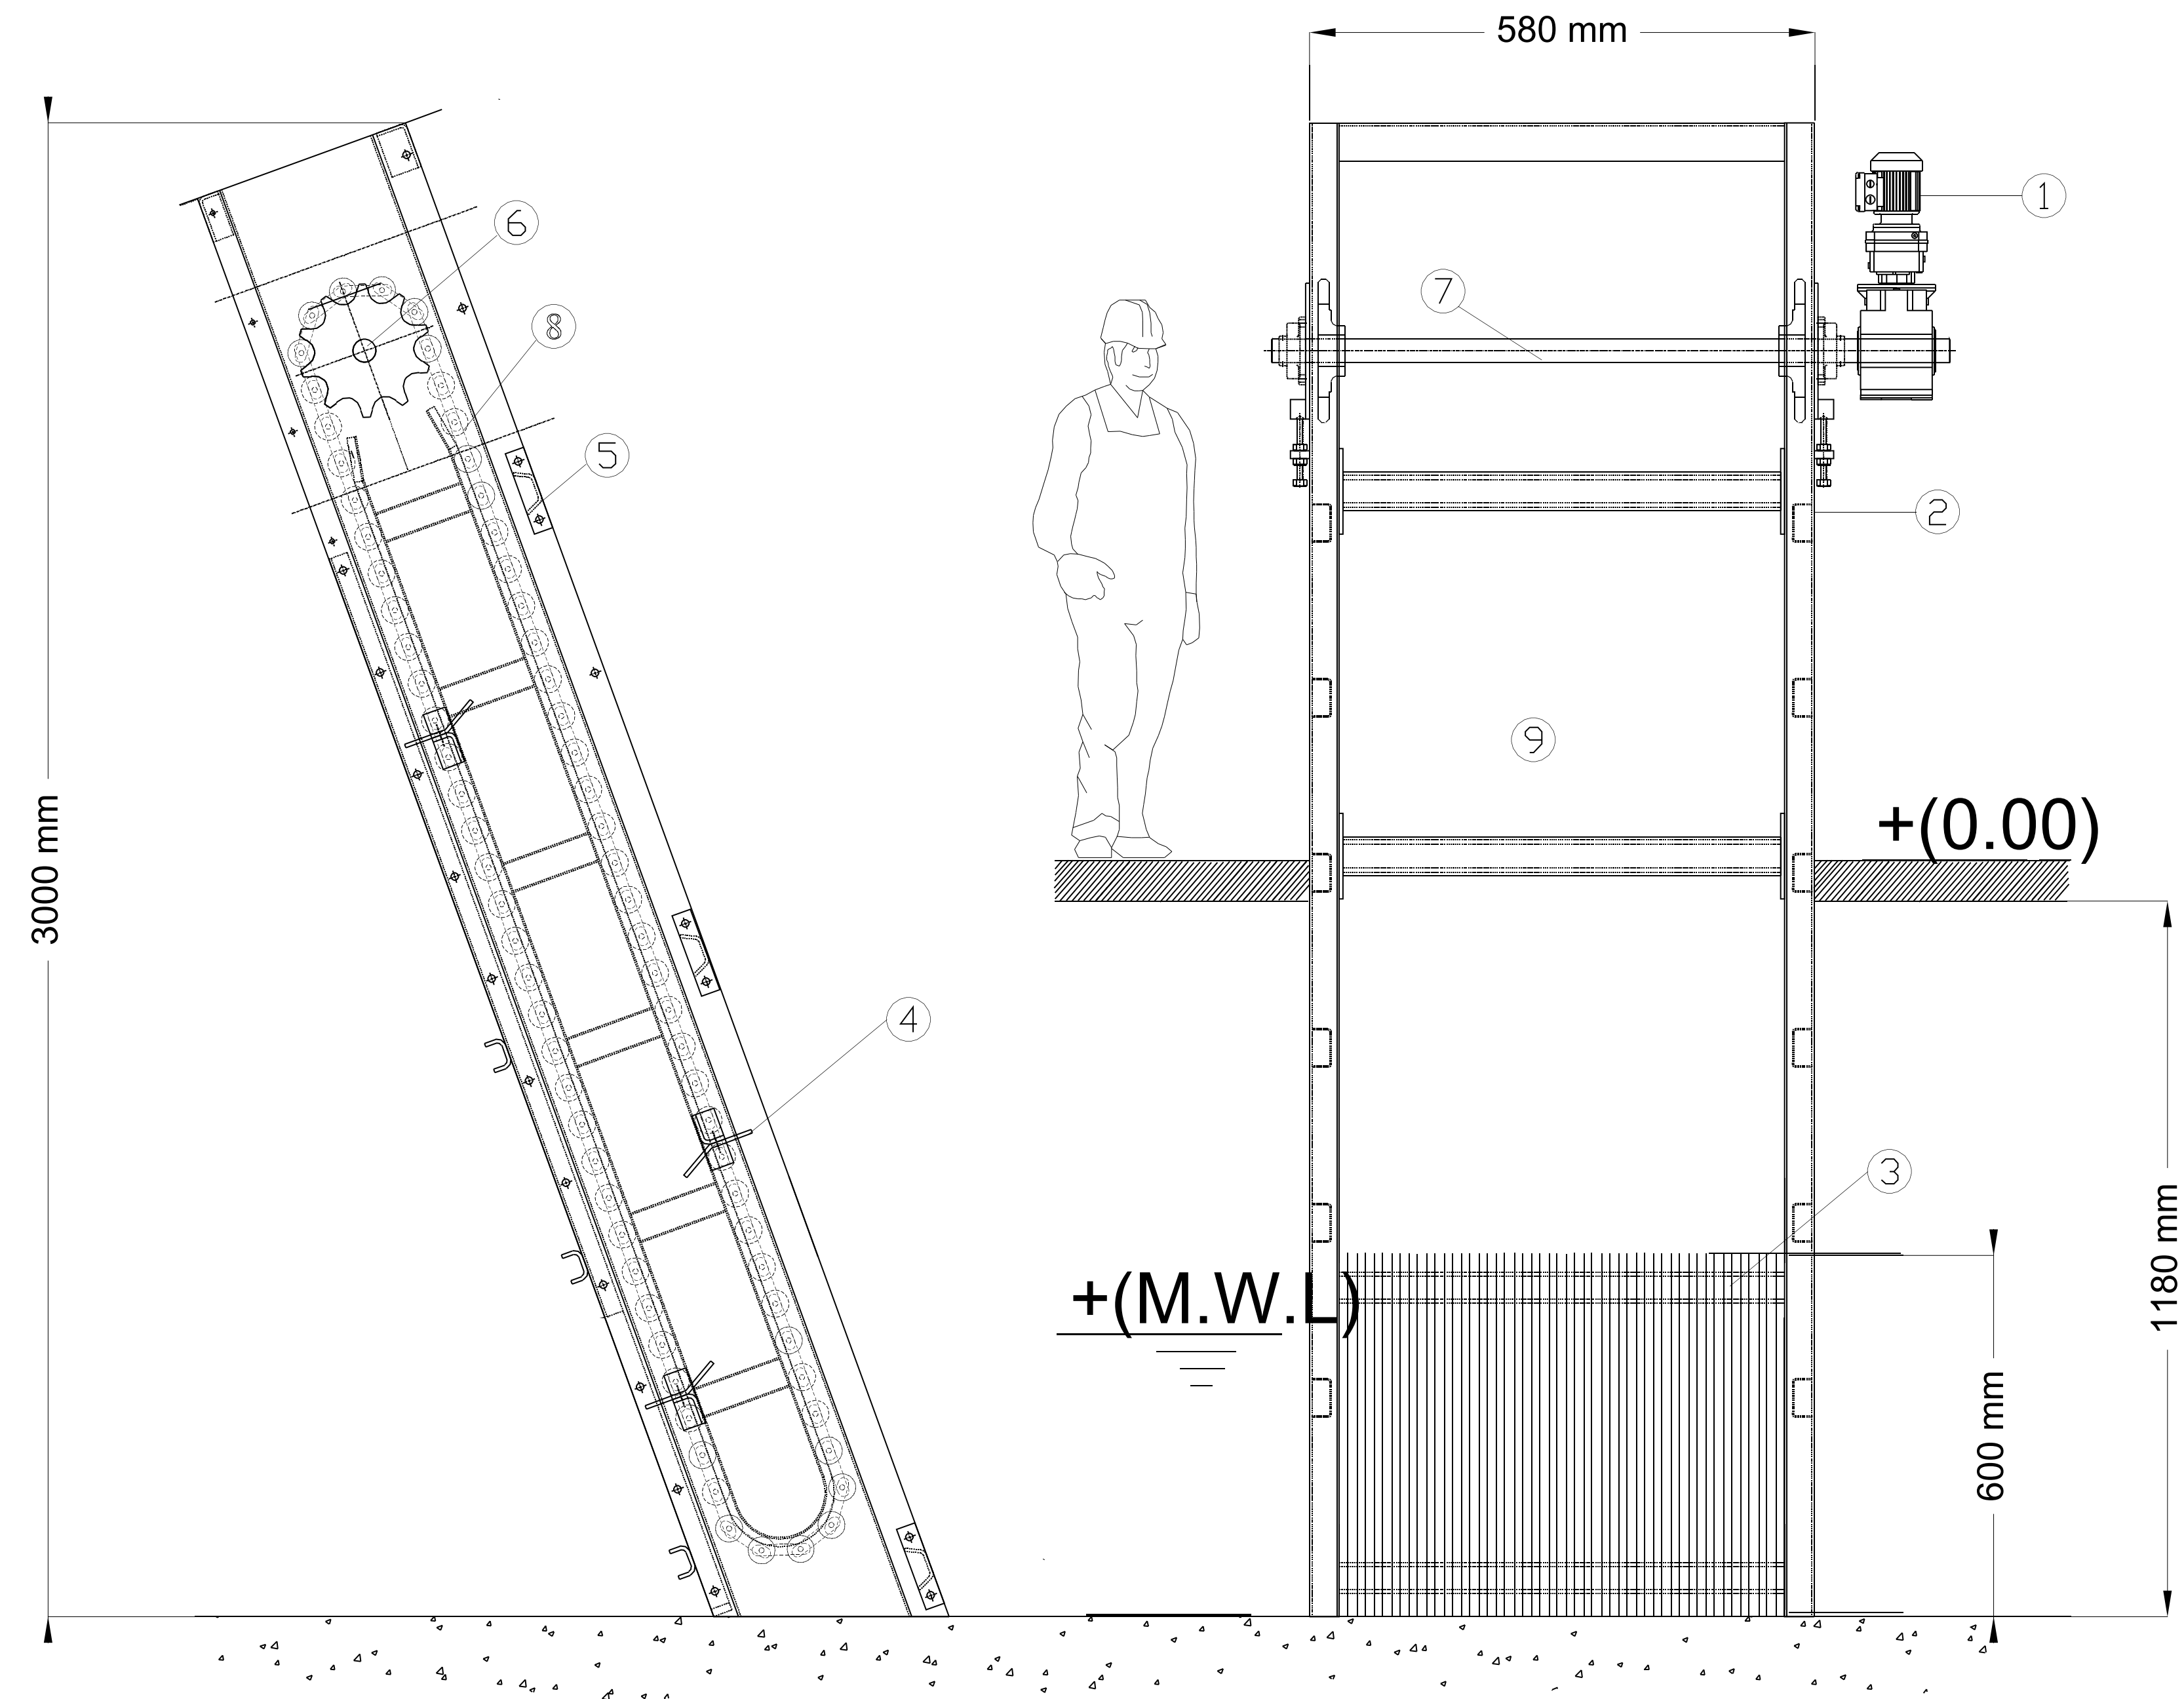

TURN KEY CONTRACTORS:

Z.C.E
AUTOSATRAD ROAD _ ARAB ABO SAAD _ CAIRO _ HELWAN
elzabzaa.sag2014@gmail.com

TITALE

Mechanical screen

SCALE	REF. DWG. NO.	SIZE	REV.
DRAWN	PREPARED	CHECKED	APPROVED
K.T	A.S	A.S	S.MICHAEL