



Z.C.E

EIZAHRAA FOR ENGINEERING CONTRACTING AND Supplying

شركة الزهراء
للمقاولات الهندسية
والتوريدات

Project Name:

testdxffiles

Client Name:

tdxff

Capacity:

tdxf



Z.C.E

شركة الزهراء
للمقاولات الهندسية
والتوريدات

EIZAHRAA FOR ENGINEERING CONTRACTING AND Supplying

mbzvm.,bjhgfdgh

sfgfsv

xfvxf

vxfvf

xv xf vx

xcv fsdv sfd s



Z.C.E

EIZAHRAA FOR ENGINEERING CONTRACTING AND Supplying

شركة الزهراء
للمقاولات الهندسية
والتوريدات

1. Gritremoval



Z.C.E

شركة الزهراء
للمقاولات الهندسية
والتوريدات

EIZAHRAA FOR ENGINEERING CONTRACTING AND Supplying

Manufacturer	Factory
Quantity	One bridge serve two channel
Function	Waste water
Installation location	Rectangle tank
Installation country	Egypt
Installation (indoor, outdoor)	outdoor
Continuous operation	yes
No. Of hours a day	24/24 h

Total tank width	600 mm
Total tank length	7500 mm
Water depth	600 mm
Length of the bridge	2000 mm
Width of bridge	1000 mm
Qty of driving wheels / bridge	2
Qty of free wheels / bridge	2
Qty of drive gearbox / bridge	1
Admissible load on bridge / tank	500 kg / m ²
Max. Allowable deflection / tank	1/500

Walkway type	Grating
Handrail Type	tubular
Handrail Height	1000 mm
Wheel Diameter	300 mm
Wheel Width	90 mm
Wheel rail	square bar 40x40mm



Z.C.E

شركة الزهراء
للمقاولات الهندسية
والتوريدات

EIZAHRAA FOR ENGINEERING CONTRACTING AND Supplying

Grease scrapper Thickness	6 mm
Height of the scrapper	300 mm
Fixation of sludge scrapper	by pipe suspenders
Rubber wearing strips cross section	12x100 mm
Scum ramp thickness	6mm
Gearbox Qty	1
Gearbox Trade mark	SEW
Model	SA57/T
Electric Motor Trade Mark	SEW
Rated Power	0.37 kW
Supply Voltage	380 V, 3 Phases, 50 Hz
Insulation	Class F
Temp Rise	Class B
Ingress Protection	IP65
Sand Scrapper Thickness	6 mm
Height of the scrapper	300 mm
Fixation of sludge scrapper	by pipe suspenders
Rubber wearing strips cross section	12x100 mm
Drive Unit Gearbox Qty	1
Drive Unit Trade Mark	SEW
Drive Unit Model	SA77/T
Electric Motor Trade Mark	SEW
Electric Motor Rated Power	0.18 kW





Z.C.E

شركة الزهراء
للمقاولات الهندسية
والتوريدات

EIZAHRAA FOR ENGINEERING CONTRACTING AND Supplying

Insulation	Class F
Temp Rise	Class B
Ingress Protection	IP65
Local control panel	Electrostatic painting
Panel thicknesses	2 mm
Component	Schneider
Operation	Manual / Automatic timer switch
Material of Bridge	Hot deep galvanized steel
Scum ramp	AISI 304
Grease Scraper	AISI 304
Sludge Scraper	AISI 304
Bolts and nuts	AISI 304 (A2)
Open mesh floor	GRP or Hot deep galvanized steel
Wheel	Carbon steel
Wheel Shaft	Carbon steel

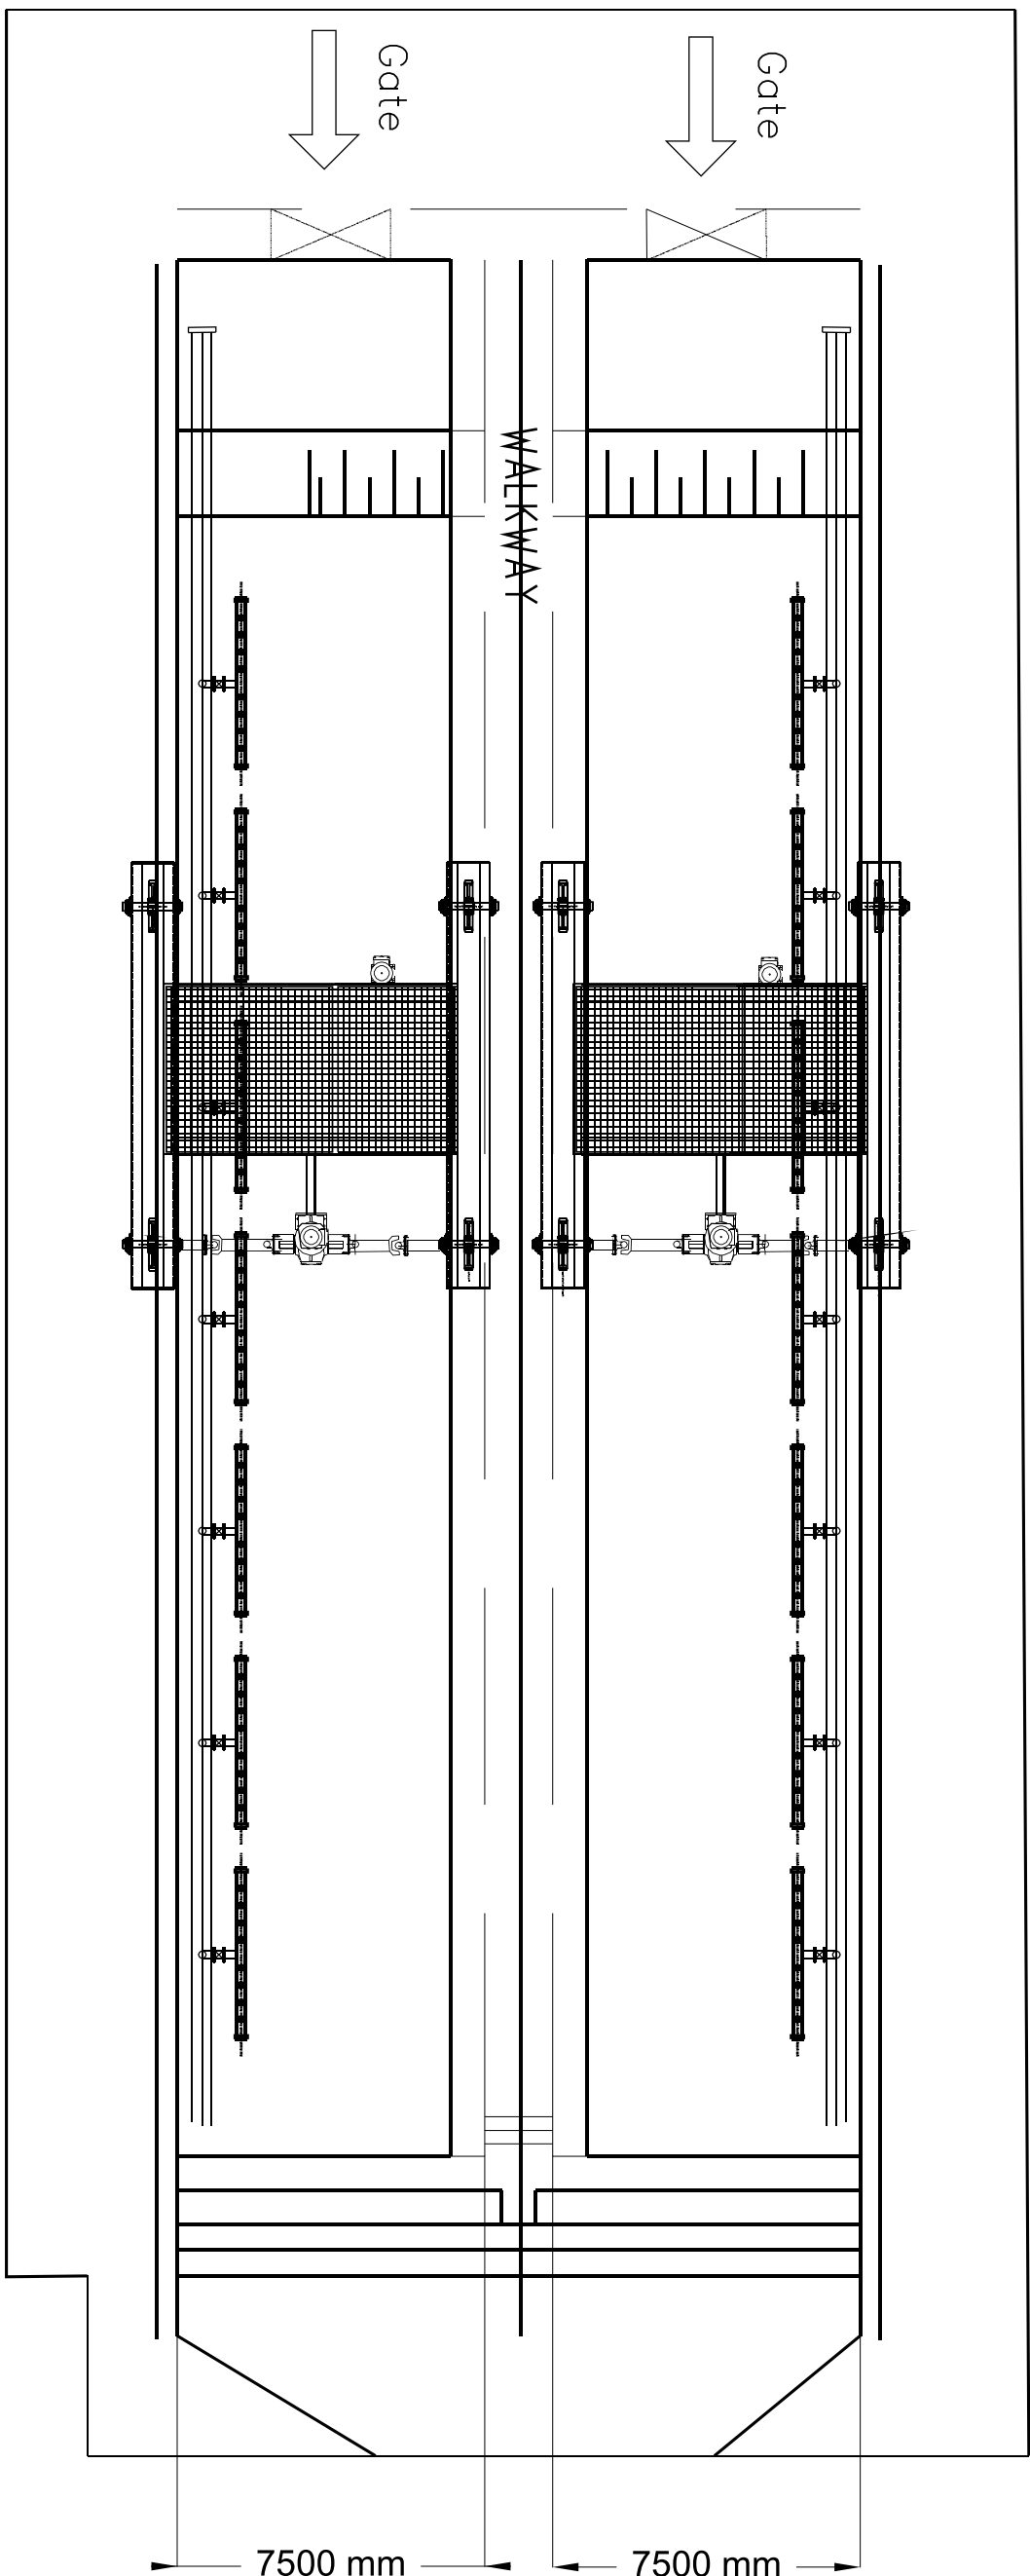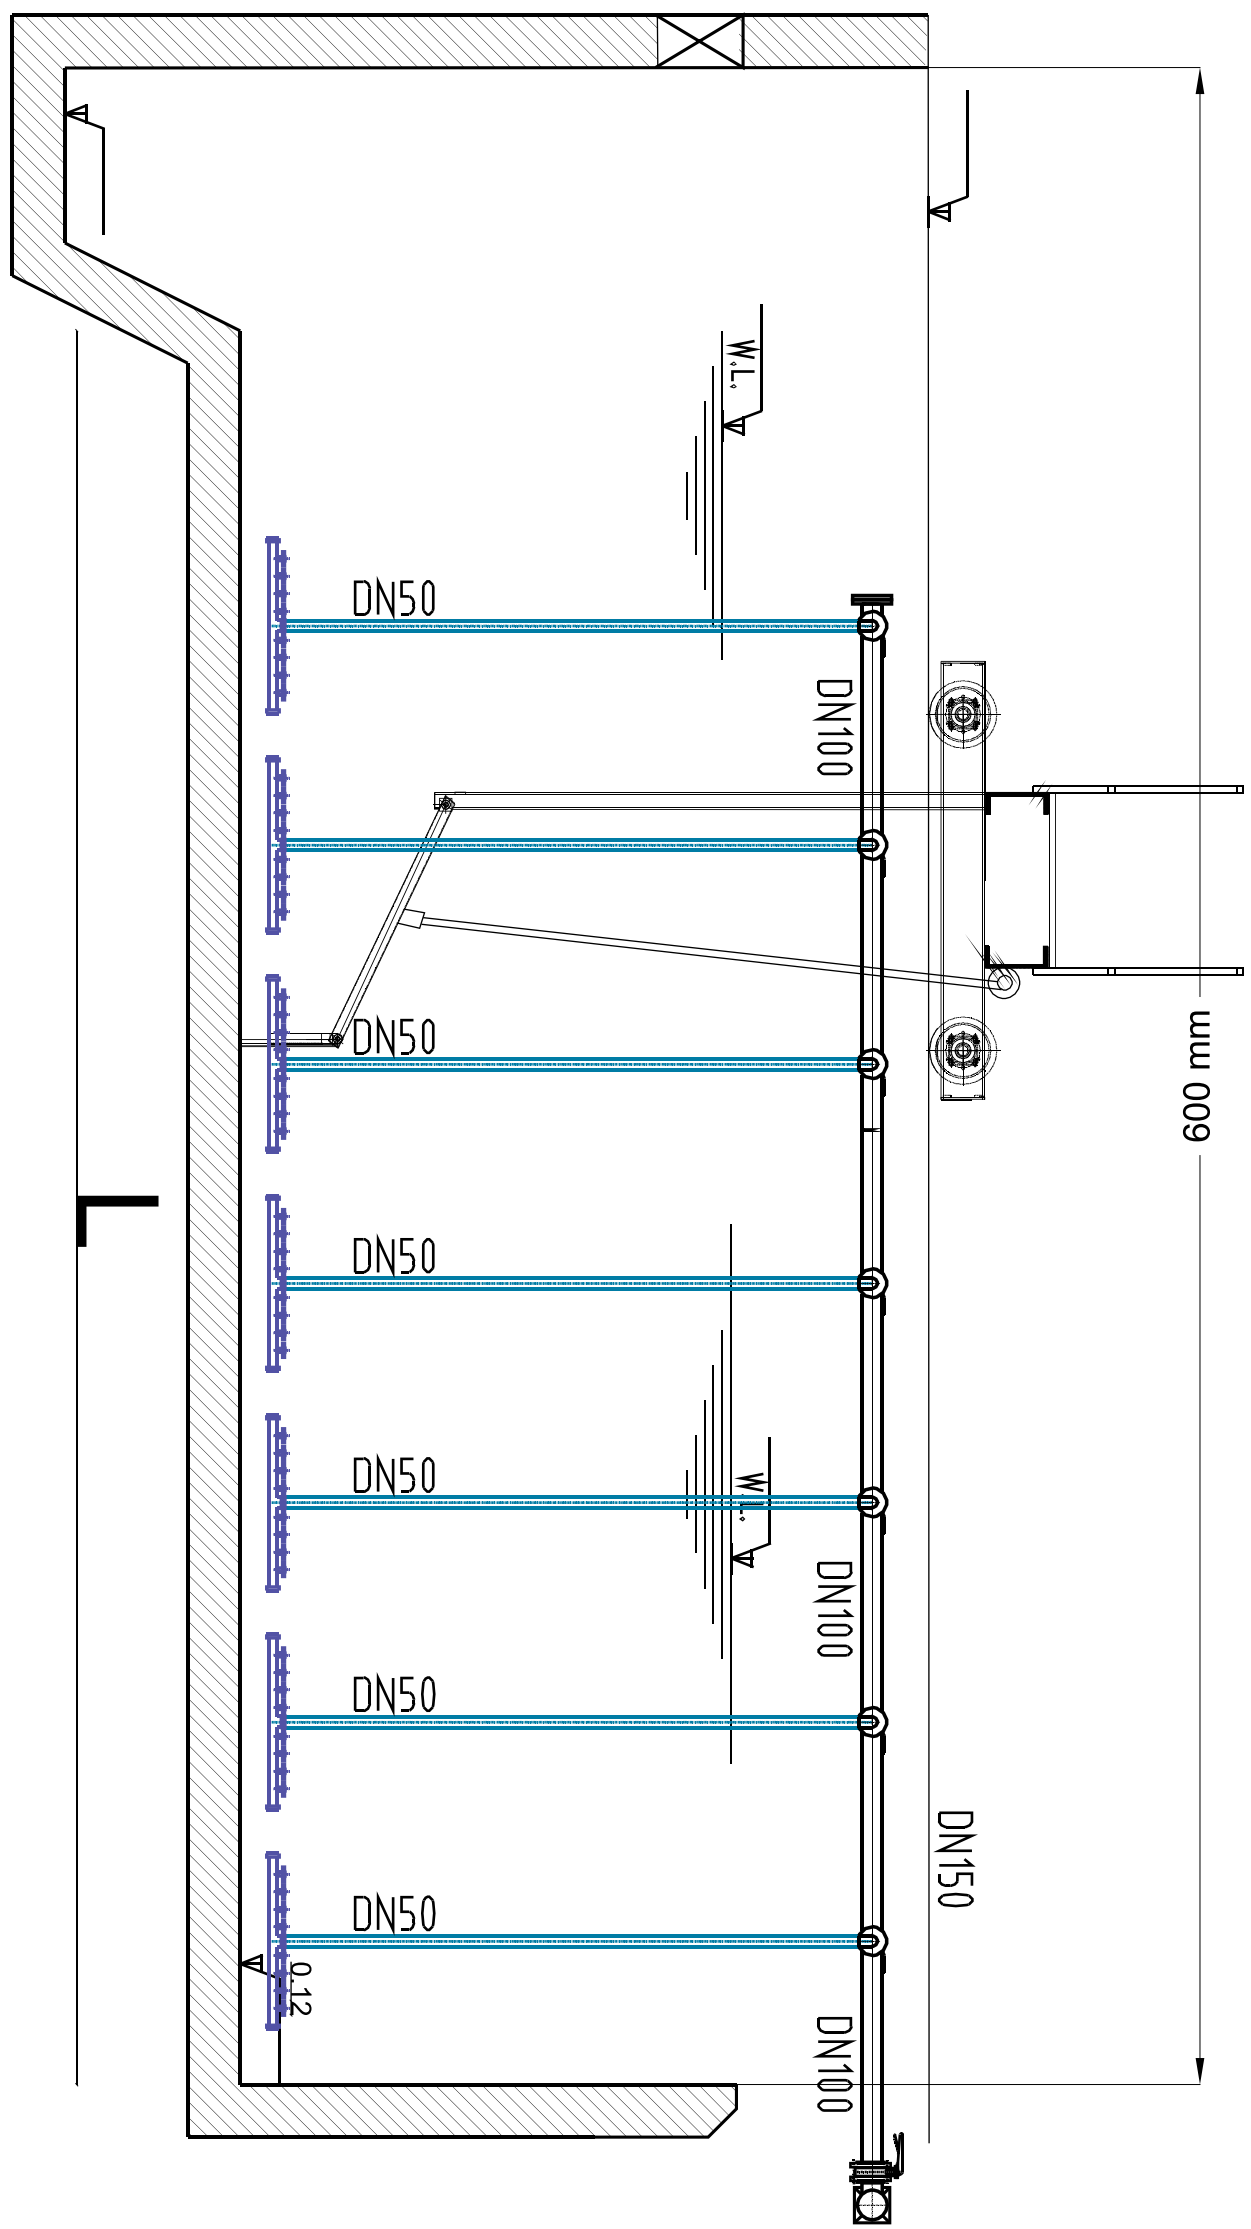

DESIGNER'S CONTRACTORS
Z.C.P.
2000/2001 ROAD, ALBA, ALBA
ALBA, ALBA
ALBA, ALBA

TITLE
GHI 000000

SCALE	REF. DWS. NO.	SIZE	REV.
1:1	AS	AS	DATE
1:1	AS	AS	DATE



Z.C.E

EIZAHRAA FOR ENGINEERING CONTRACTING AND Supplying

شركة الزهراء
للمقاولات الهندسية
والتوريدات

2. Container




Z.C.E

شركة الزهراء
للمقاولات الهندسية
والتوريدات

EIZAHRAA FOR ENGINEERING CONTRACTING AND Supplying

Manufacturer	Factory
Quantity	1
Capacity	2 m3
Thicknesses	6mm
No. of Wheel	4
Automatic safety lock	Yes
Frame	Epoxy Coated
Bolts & Nuts	Galvanized steel
Wheel	Steel with rubber

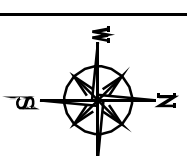


NOTES

1. ALL INFORMATION CONTAINED HEREIN IS UNCLASSIFIED
DATE 07/20/2010 BY 60322 UCBAW

4	Hand pipe	ST - 37
3	Wheel	ST - 37
2	Formed U 80 mm	ST - 37
1	Container 4 mm	ST - 37
Items	Manufacture	Material

VITOLIO KIM - 08-971-628-0024
Z.C.E
MEXARAAA
AUTOSATLAD ROAD _ CAMO _ MEXWAN
e.kim.kim@gmail.com / post@ll.com

◎お礼状				
送附元	送附先	送附金	送附日	送附元印
0104-0099	〒262-0148 徳島県徳島市	0000000000	01.27.09/09/09	0017
送附内容	送附品名	送附金額	送附元印	送附元印
現金振込	現金	0.0000	0017	0000000000

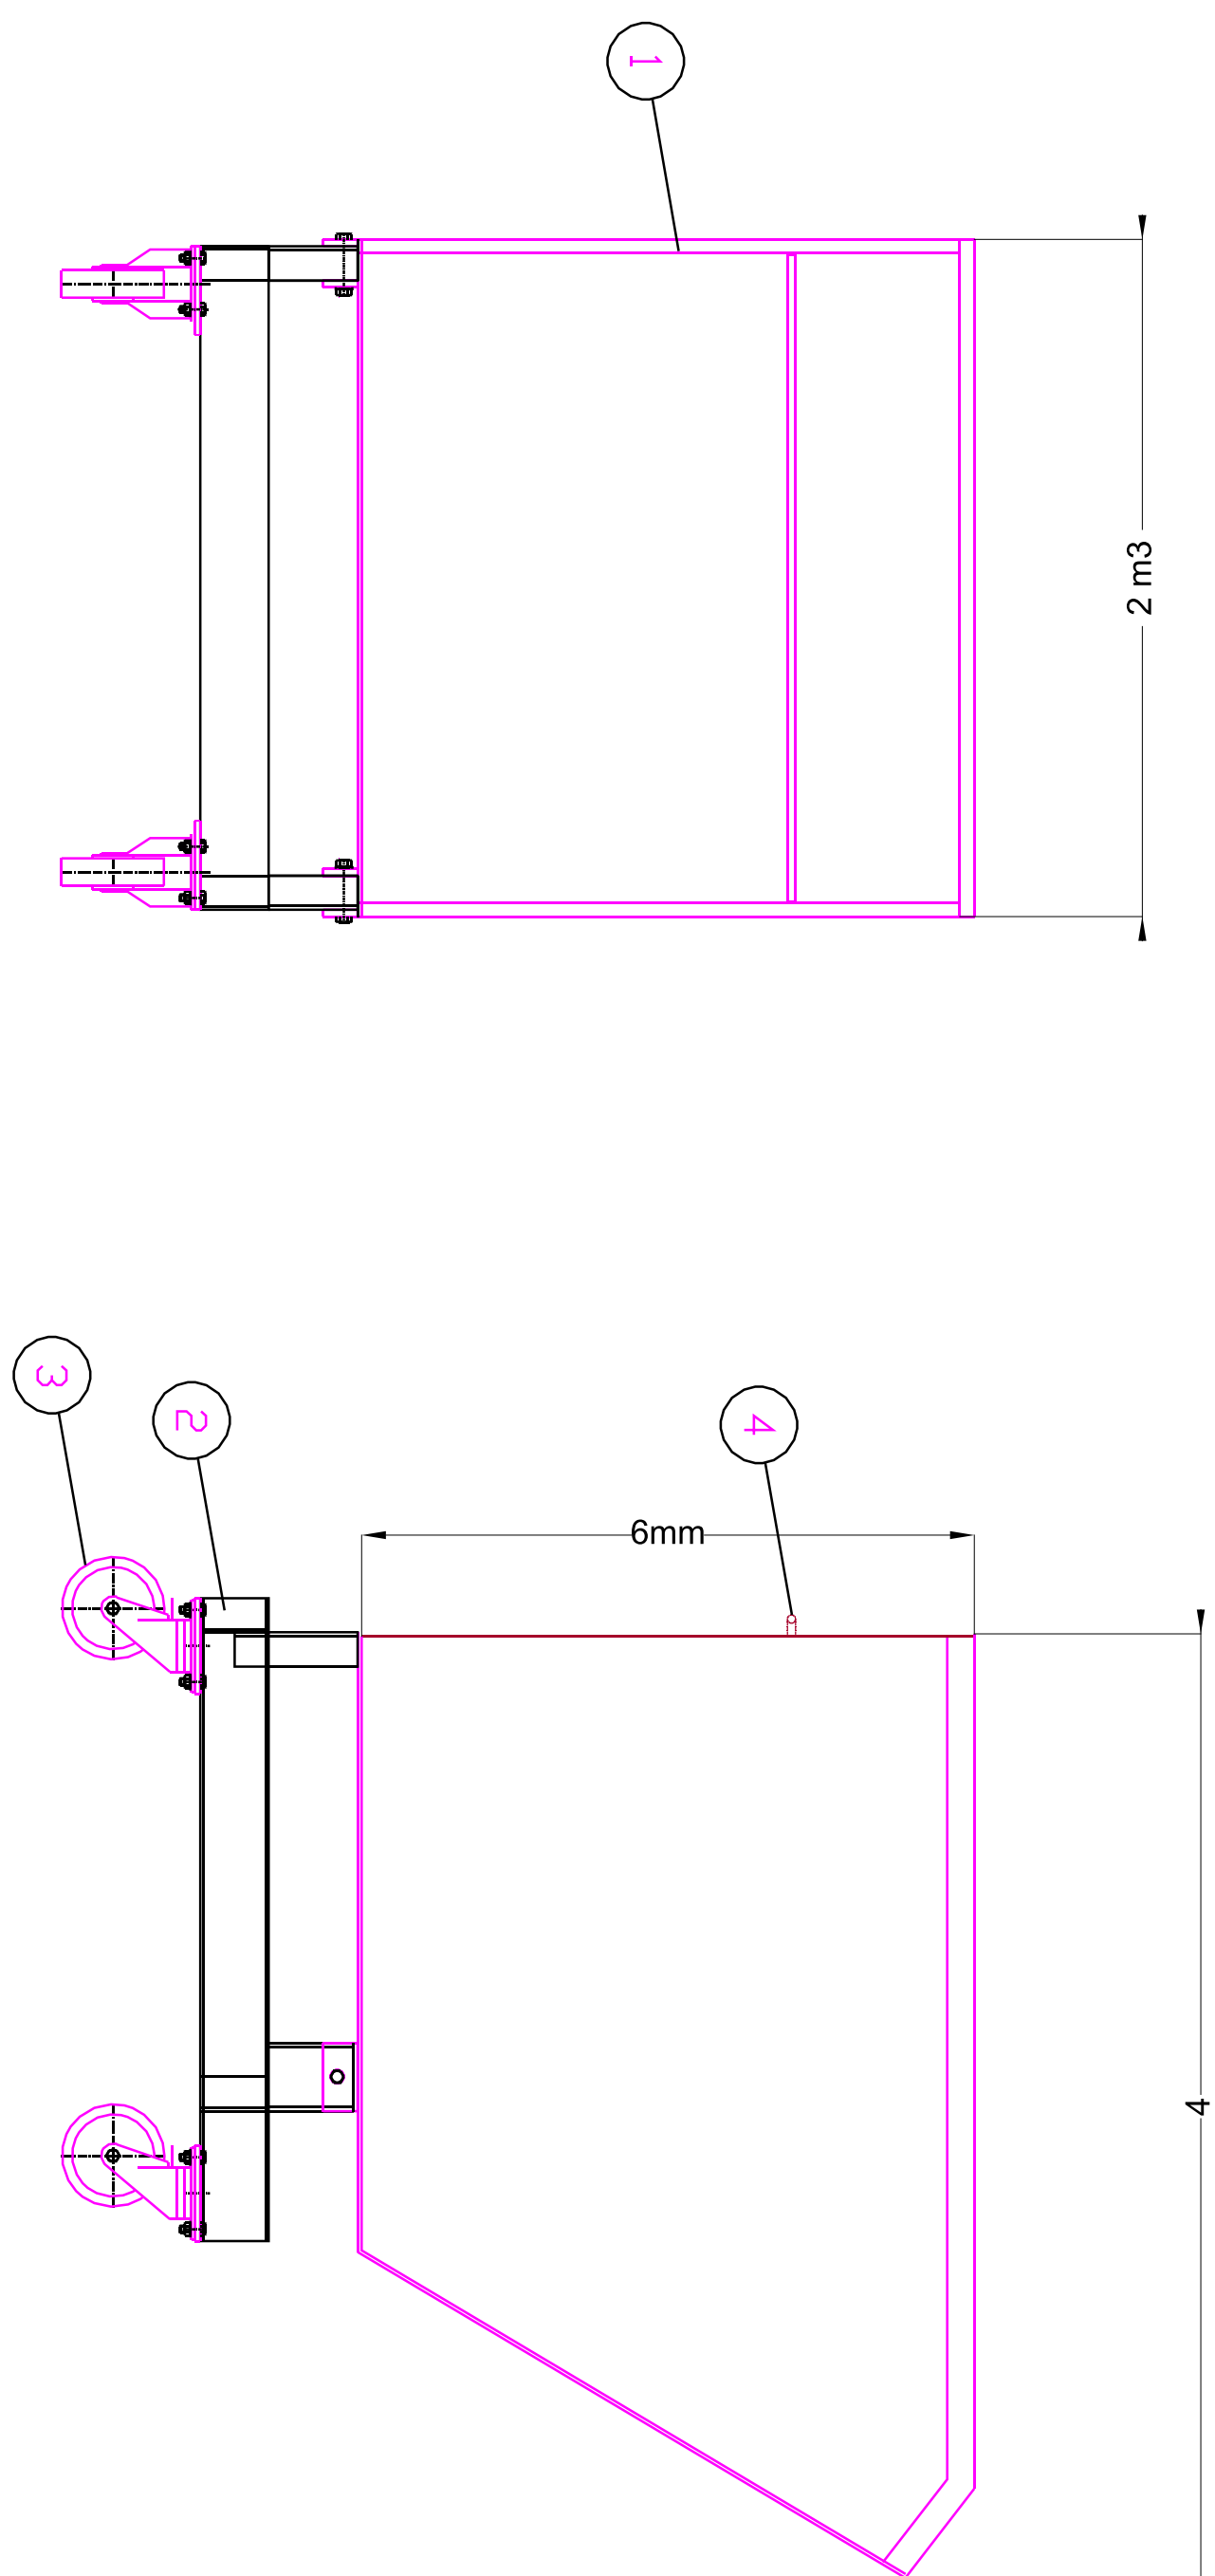



Z.C.E

EIZAHRAA FOR ENGINEERING CONTRACTING AND Supplying

شركة الزهراء
للمقاولات الهندسية
والتوريدات

3. Telescopic Valve




Z.C.E

شركة الزهراء
للمقاولات الهندسية
والتوريدات

EIZAHRAA FOR ENGINEERING CONTRACTING AND Supplying

Manufacturer	Factory
Quantity	1
Operation	Manual rising stem
Diameter	DN 200 mm
Material of Body	AISI 316
Material of Main shaft	AISI 316
Material of Stem nut	Bronze
Gasket	EPDM
Pillar	ST-37

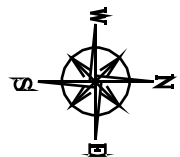


NOTES

1. ALL DIMENSIONS IN MM UNLESS OTHERWISE NOTED
2. ALL DIMENSIONS IN mm

5	Isola ybail & A.C. 10000	
4	Ybail	PS-1116
3	Isola	PS-1116
2	Ybail	PS-1116
1	Ybail	PS-1116
Item	Isola	Isola

DATE OF CONTRACT
Z.C.E
AYYAKKALAI ROAD - CAIRO - ISRAEL
Isola ybail & A.C. 10000

DATE	DATE OF CONTRACT	DATE	DATE
DATE	DATE OF CONTRACT	DATE	DATE
DATE	DATE OF CONTRACT	DATE	DATE
DATE	DATE OF CONTRACT	DATE	DATE

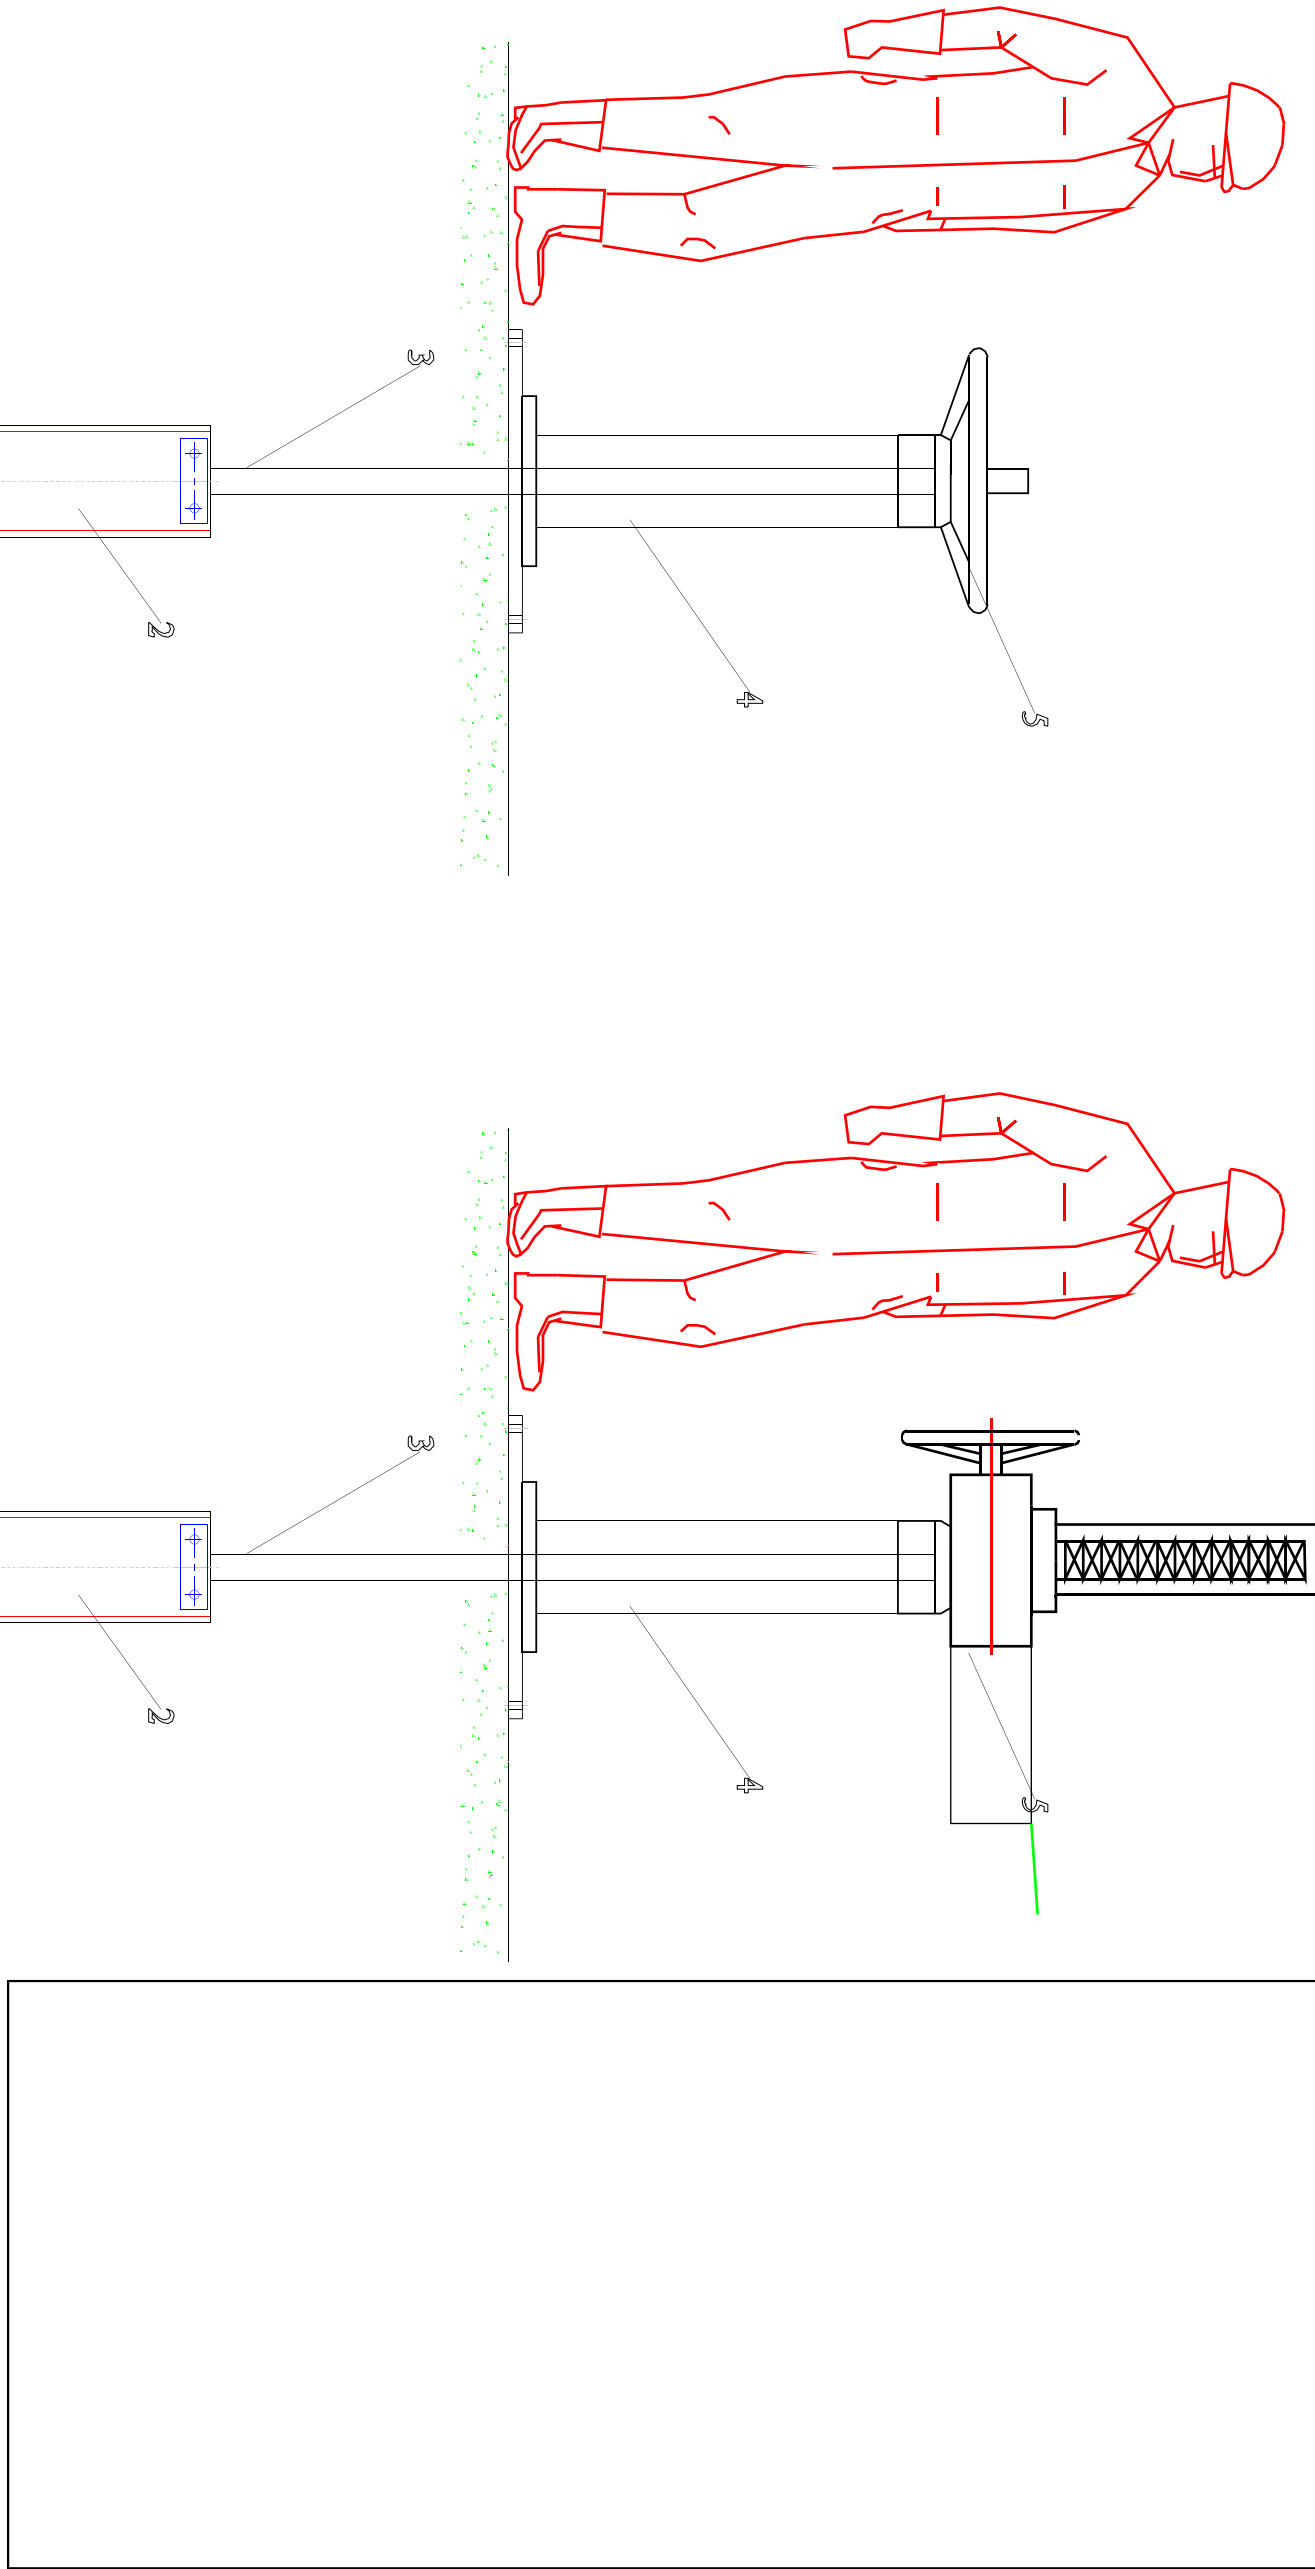

Manual Operation

Electrical Operation

DN	100	200	300	400	500	600
Length	1000	1000	1200	1200	1200	1200



Z.C.E

EIZAHRAA FOR ENGINEERING CONTRACTING AND Supplying

شركة الزهراء
للمقاولات الهندسية
والتوريدات

4. Primary Sedimentation Tank



Z.C.E

شركة الزهراء
للمقاولات الهندسية
والتوريدات

EIZAHRAA FOR ENGINEERING CONTRACTING AND Supplying

Manufacturer	Factory
Quantity	2
Installation location	Circle tank
Installation country	Egypt
Installation (indoor, outdoor)	outdoor
Continuous operation	yes
No. Of hours a day	24/24 h
Total Tank Diameter	11700 mm
Water Depth	3500 mm
Type	Half Bridge
Length of the bridge	7000 mm
Width of the bridge	1000 mm
Qty of driving wheels / bridge	2
Qty of free wheels / bridge	2
Qty of drive gearbox / bridge	1
Admissible load on bridge / tank	500 kg / m ²
Max. Allowable deflection / tank	1/500
Slip ring Trade Mark	Ravioli or equal
Slip ring No. of ring	Minimum 6 ring
Slip ring Ingress Protection	IP 55
Hand rail type	tubular
Height	1000 mm
Walkway type	Grating



Z.C.E

شركة الزهراء
للمقاولات الهندسية
والتوريدات

EIZAHRAA FOR ENGINEERING CONTRACTING AND Supplying

Width	800 mm
Scum box Qty	1
Scum box Width	900 mm
Scum box thickness	4 mm
Diameter of exit pipe	DN 150 mm
Scum box Scraper Thickness	6 mm
Height of the Scraper	300 mm
Fixation of scum scraper	by pipe suspenders
Sludge Scraper Thickness	6 mm
Height of the Scraper	300 mm
Fixation of scum scraper	by pipe suspenders
Rubber wearing strips cross section	13x100mm
Overflow weir Type	V-Notch (adjustable slot)
Slots	12(W) x 50 (H) mm
Thickness	4 mm
Height	200 mm
Type	Baffle plate
Thickness	4mm
Height	300 mm
Local control panel	Electrostatic painting
Panel Thickness	2 mm
Component	Schneider
Operation	Manual / Automatic timer switch




Z.C.E

شركة الزهراء
للمقاولات الهندسية
والتوريدات

EIZAHRAA FOR ENGINEERING CONTRACTING AND Supplying

Gearbox Trade Mark	SEW
Model	SA77/T
Electric Motor Trade Mark	SEW
Rated Power	0.18 kW
Supply Voltage	380 V, 3 Phases, 50 Hz
Insulation	Class F
Temp Rise	Class B
Ingress Protection	IP66
Material of Bridge	Hot deep galvanized steel
Material of Scum scraper	AISI 316
Material of Sludge scraper	AISI 316
Material of Overflow weir	AISI 316
Material of Bolts and nuts	AISI 316 (A4)
Material of Open mesh floor	GRP or Hot deep galvanized steel
Wheel	Polyurethane
Wheel shaft	Carbon steel

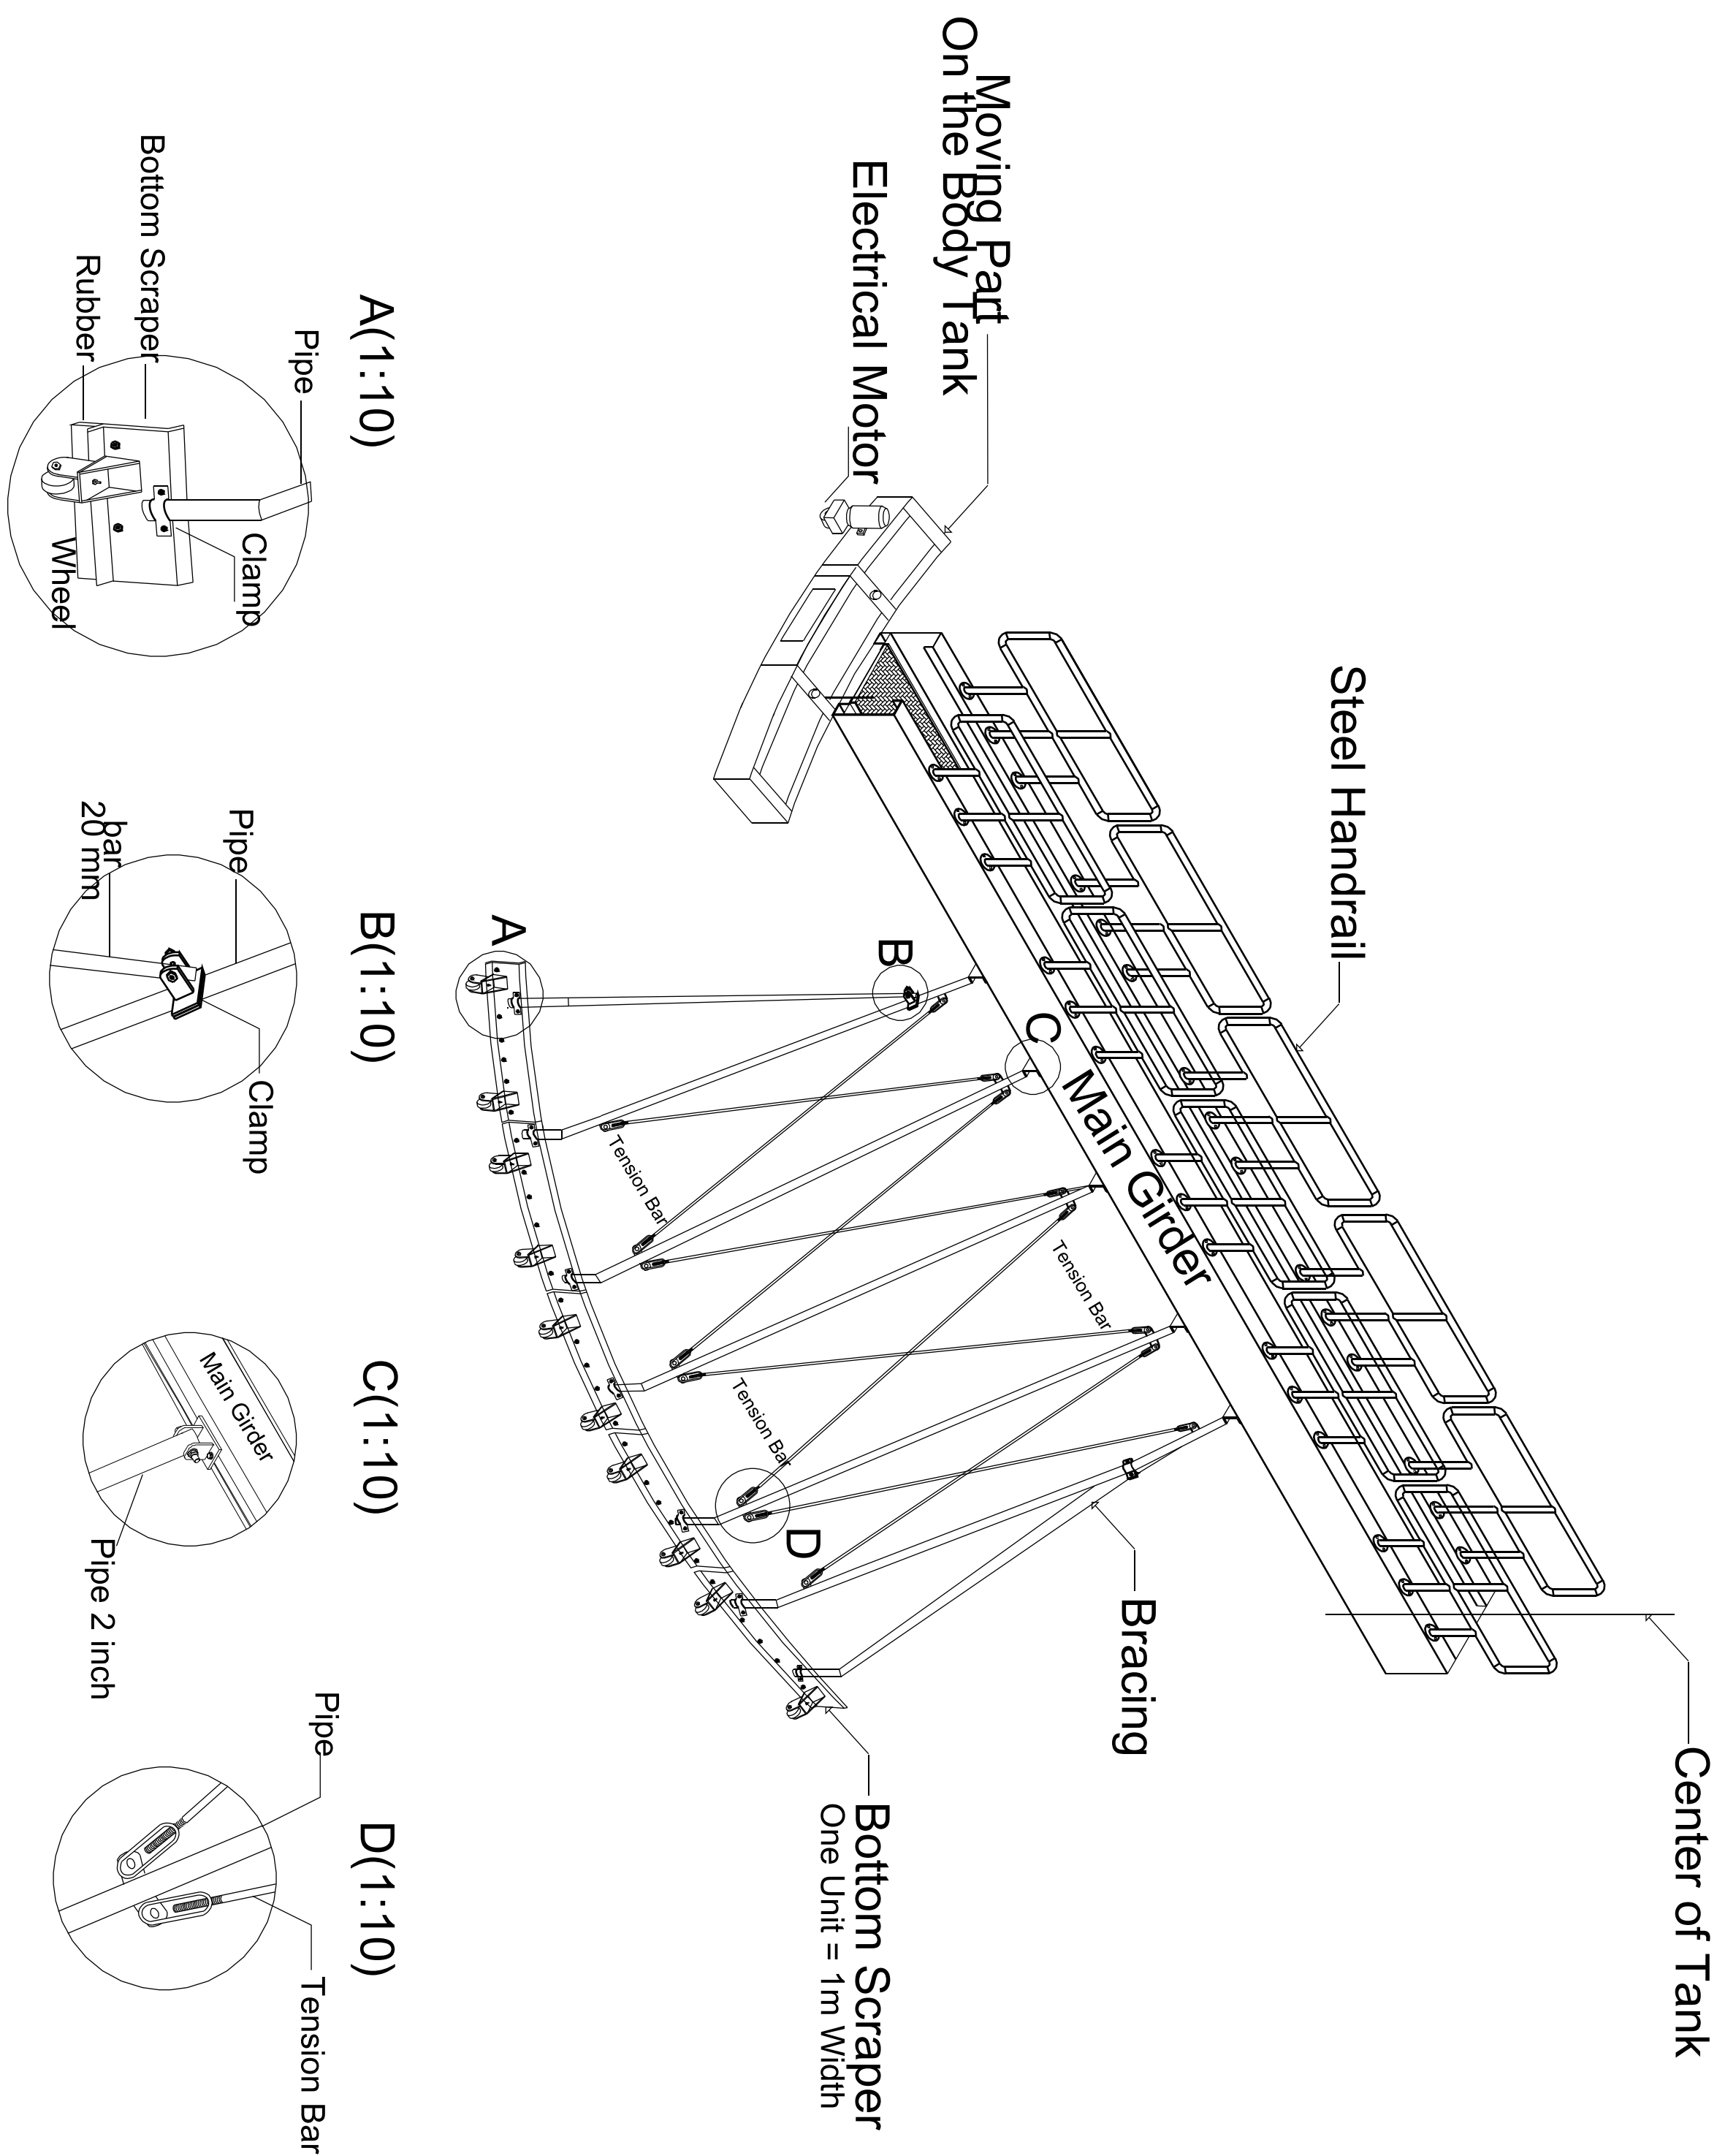

Half Bridge Clarifiers

Isometric DWG

TURNKEY CONTRACTORS			
22,222,222			
Z.C.P.			
AUTOSKETCH ROAD, ALABAMA ROAD, CALIFORNIA, 2000, 2000			
404.444.4444			
TITLE			
Half Bridge			
SCALE			
DRAWN			
K.T.			



Z.C.E

EIZAHRAA FOR ENGINEERING CONTRACTING AND Supplying

شركة الزهراء
للمقاولات الهندسية
والتوريدات

5. Thickener



Z.C.E

شركة الزهراء
للمقاولات الهندسية
والتوريدات

EIZAHRAA FOR ENGINEERING CONTRACTING AND Supplying

Manufacturer	Factory
Quantity	2
Installation location	Circle tank
Installation country	Egypt
Installation (indoor, outdoor)	outdoor
Continuous operation	yes
No. Of hours a day	24/24 h
Total Tank Diameter	6000 mm
Water Depth	3500 mm
Bridge Type	Concrete
Sludge Scraper Thickness	6 mm
Height of the Scraper	270 mm
Rubber wearing strips cross section	8x100mm
Back up plate	AISI 316 (4mm)
No. Of Central shaft	1
Central shaft	Pipe schedule 40
Feeding cylinder	4 mm
Cutting arms	Fabrication Angle 50x50
Bottom bearing type	Fixing pipe with artlon
Overflow weir Type	V-Notch (adjustable slot)
Slots	12(W) x 50 (H) mm
Thickness	4 mm
Height	200 mm




Z.C.E

شركة الزهراء
للمقاولات الهندسية
والتوريدات

EIZAHRAA FOR ENGINEERING CONTRACTING AND Supplying


Local control panel	Electrostatic painting
Panel Thickness	2 mm
Component	Schneider
Operation	Manual / Automatic timer switch
Gearbox Trade Mark	SEW
Model	SA77/T
Electric Motor Trade Mark	SEW
Rated Power	0.37 kW
Supply Voltage	380 V, 3 Phases, 50 Hz
Insulation	Class F
Temp Rise	Class B
Ingress Protection	IP66
Material of Bridge	Concrete
Material of Central shaft	AISI 316
Material of Feeding cylinder	AISI 316
Material of Sludge scraper	AISI 316
Material of Overflow Weir	AISI 316
Material of Bolts and nuts	AISI 316 (A4)

PRODUCED BY AN AUTODESK EDUCATIONAL PRODUCT

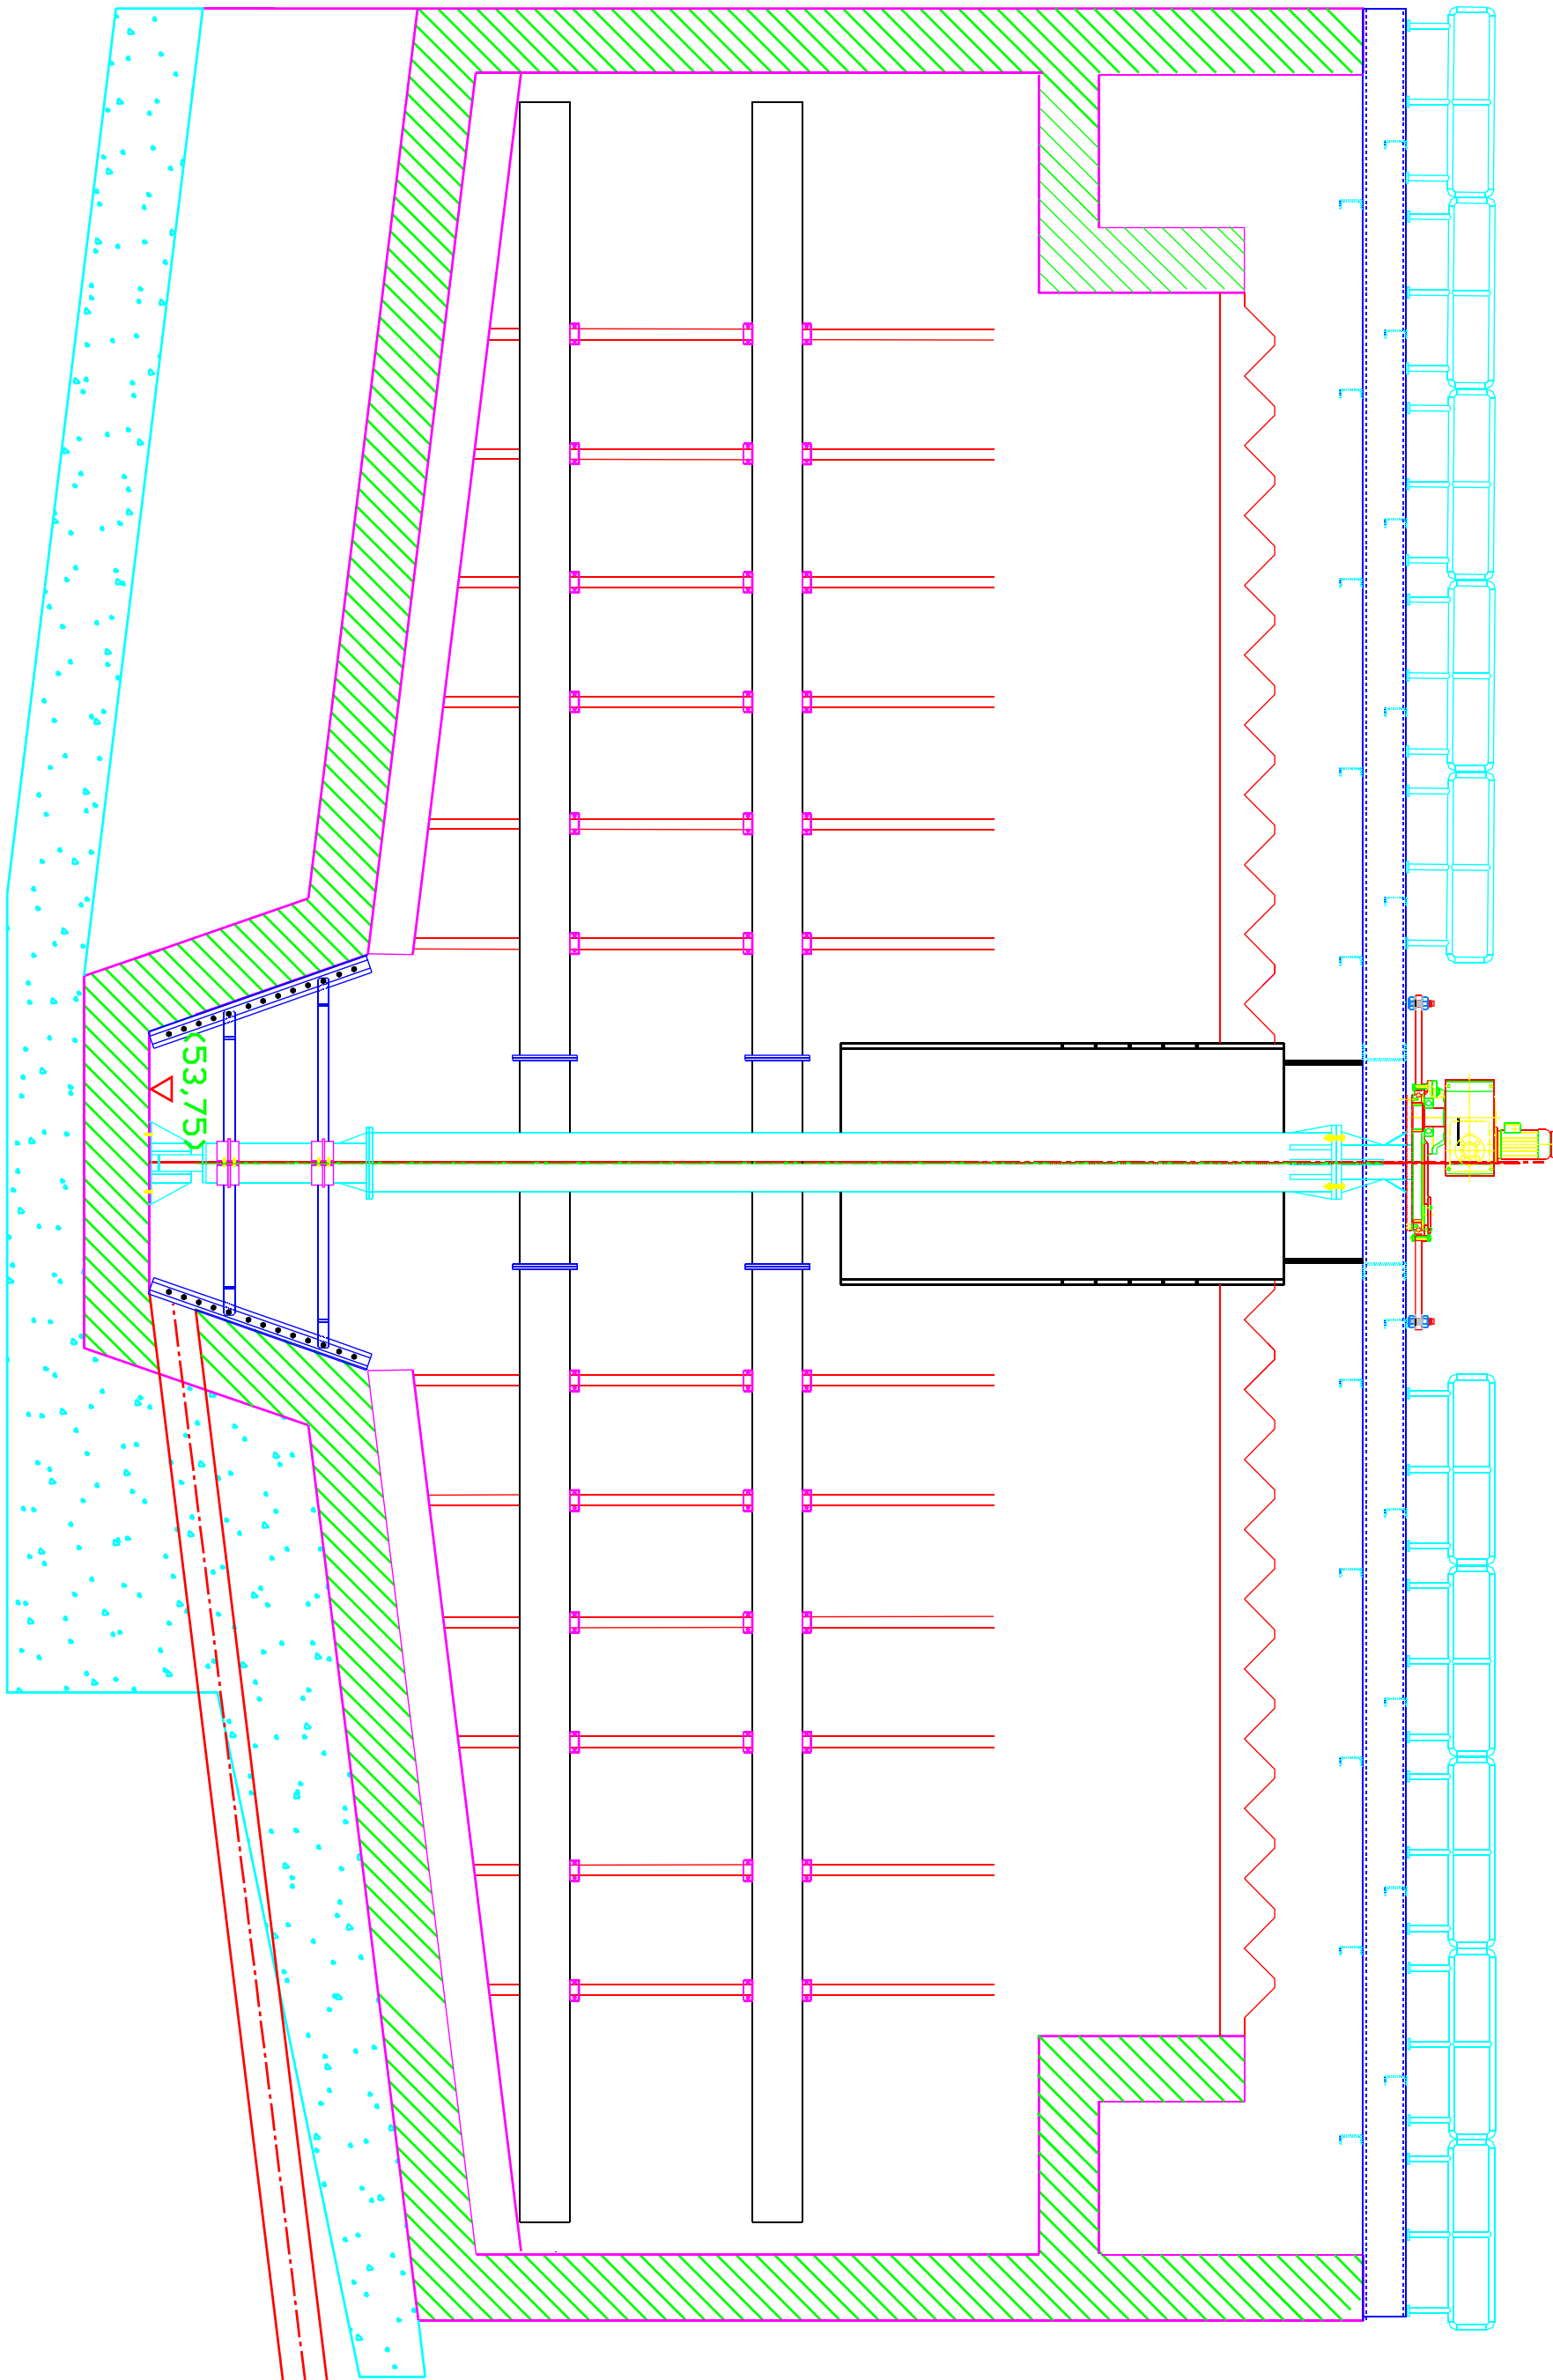

Section Side View

PRODUCED BY AN AUTODESK EDUCATIONAL PRODUCT

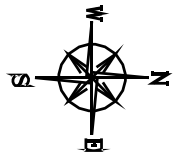

NOTES

1. ALL DIMENSIONS ARE IN METERS UNLESS OTHERWISE NOTED

2. ALL DIMENSIONS ARE IN METERS UNLESS OTHERWISE NOTED

DESIGNER'S COMMENTS:

Z. C. R.
AUTODESK EDUCATIONAL PRODUCT
autodesk.eg001@autodesk.com

TITLE

Sludge thickener tank

SCALE	REF. DIM. NO.	SIZE	REV.
1:100	1	1000	1
1:100	2	1000	1
1:100	3	1000	1

PRODUCED BY AN AUTODESK EDUCATIONAL PRODUCT



Z.C.E

EIZAHRAA FOR ENGINEERING CONTRACTING AND Supplying

شركة الزهراء
للمقاولات الهندسية
والتوريدات

6. Sand Silo





Z.C.E

شركة الزهراء
للمقاولات الهندسية
والتوريدات

EIZAHRAA FOR ENGINEERING CONTRACTING AND Supplying

Manufacturer	Factory
Quantity	1
Capacity	5 m3
Inlet	Pipe 150 mm PN10
Outlet	Pipe 150 mm PN10
Shell	Epoxy coated steel 37
Cone	Epoxy coated steel 37
Nozzle	Epoxy coated steel 37

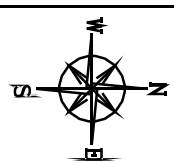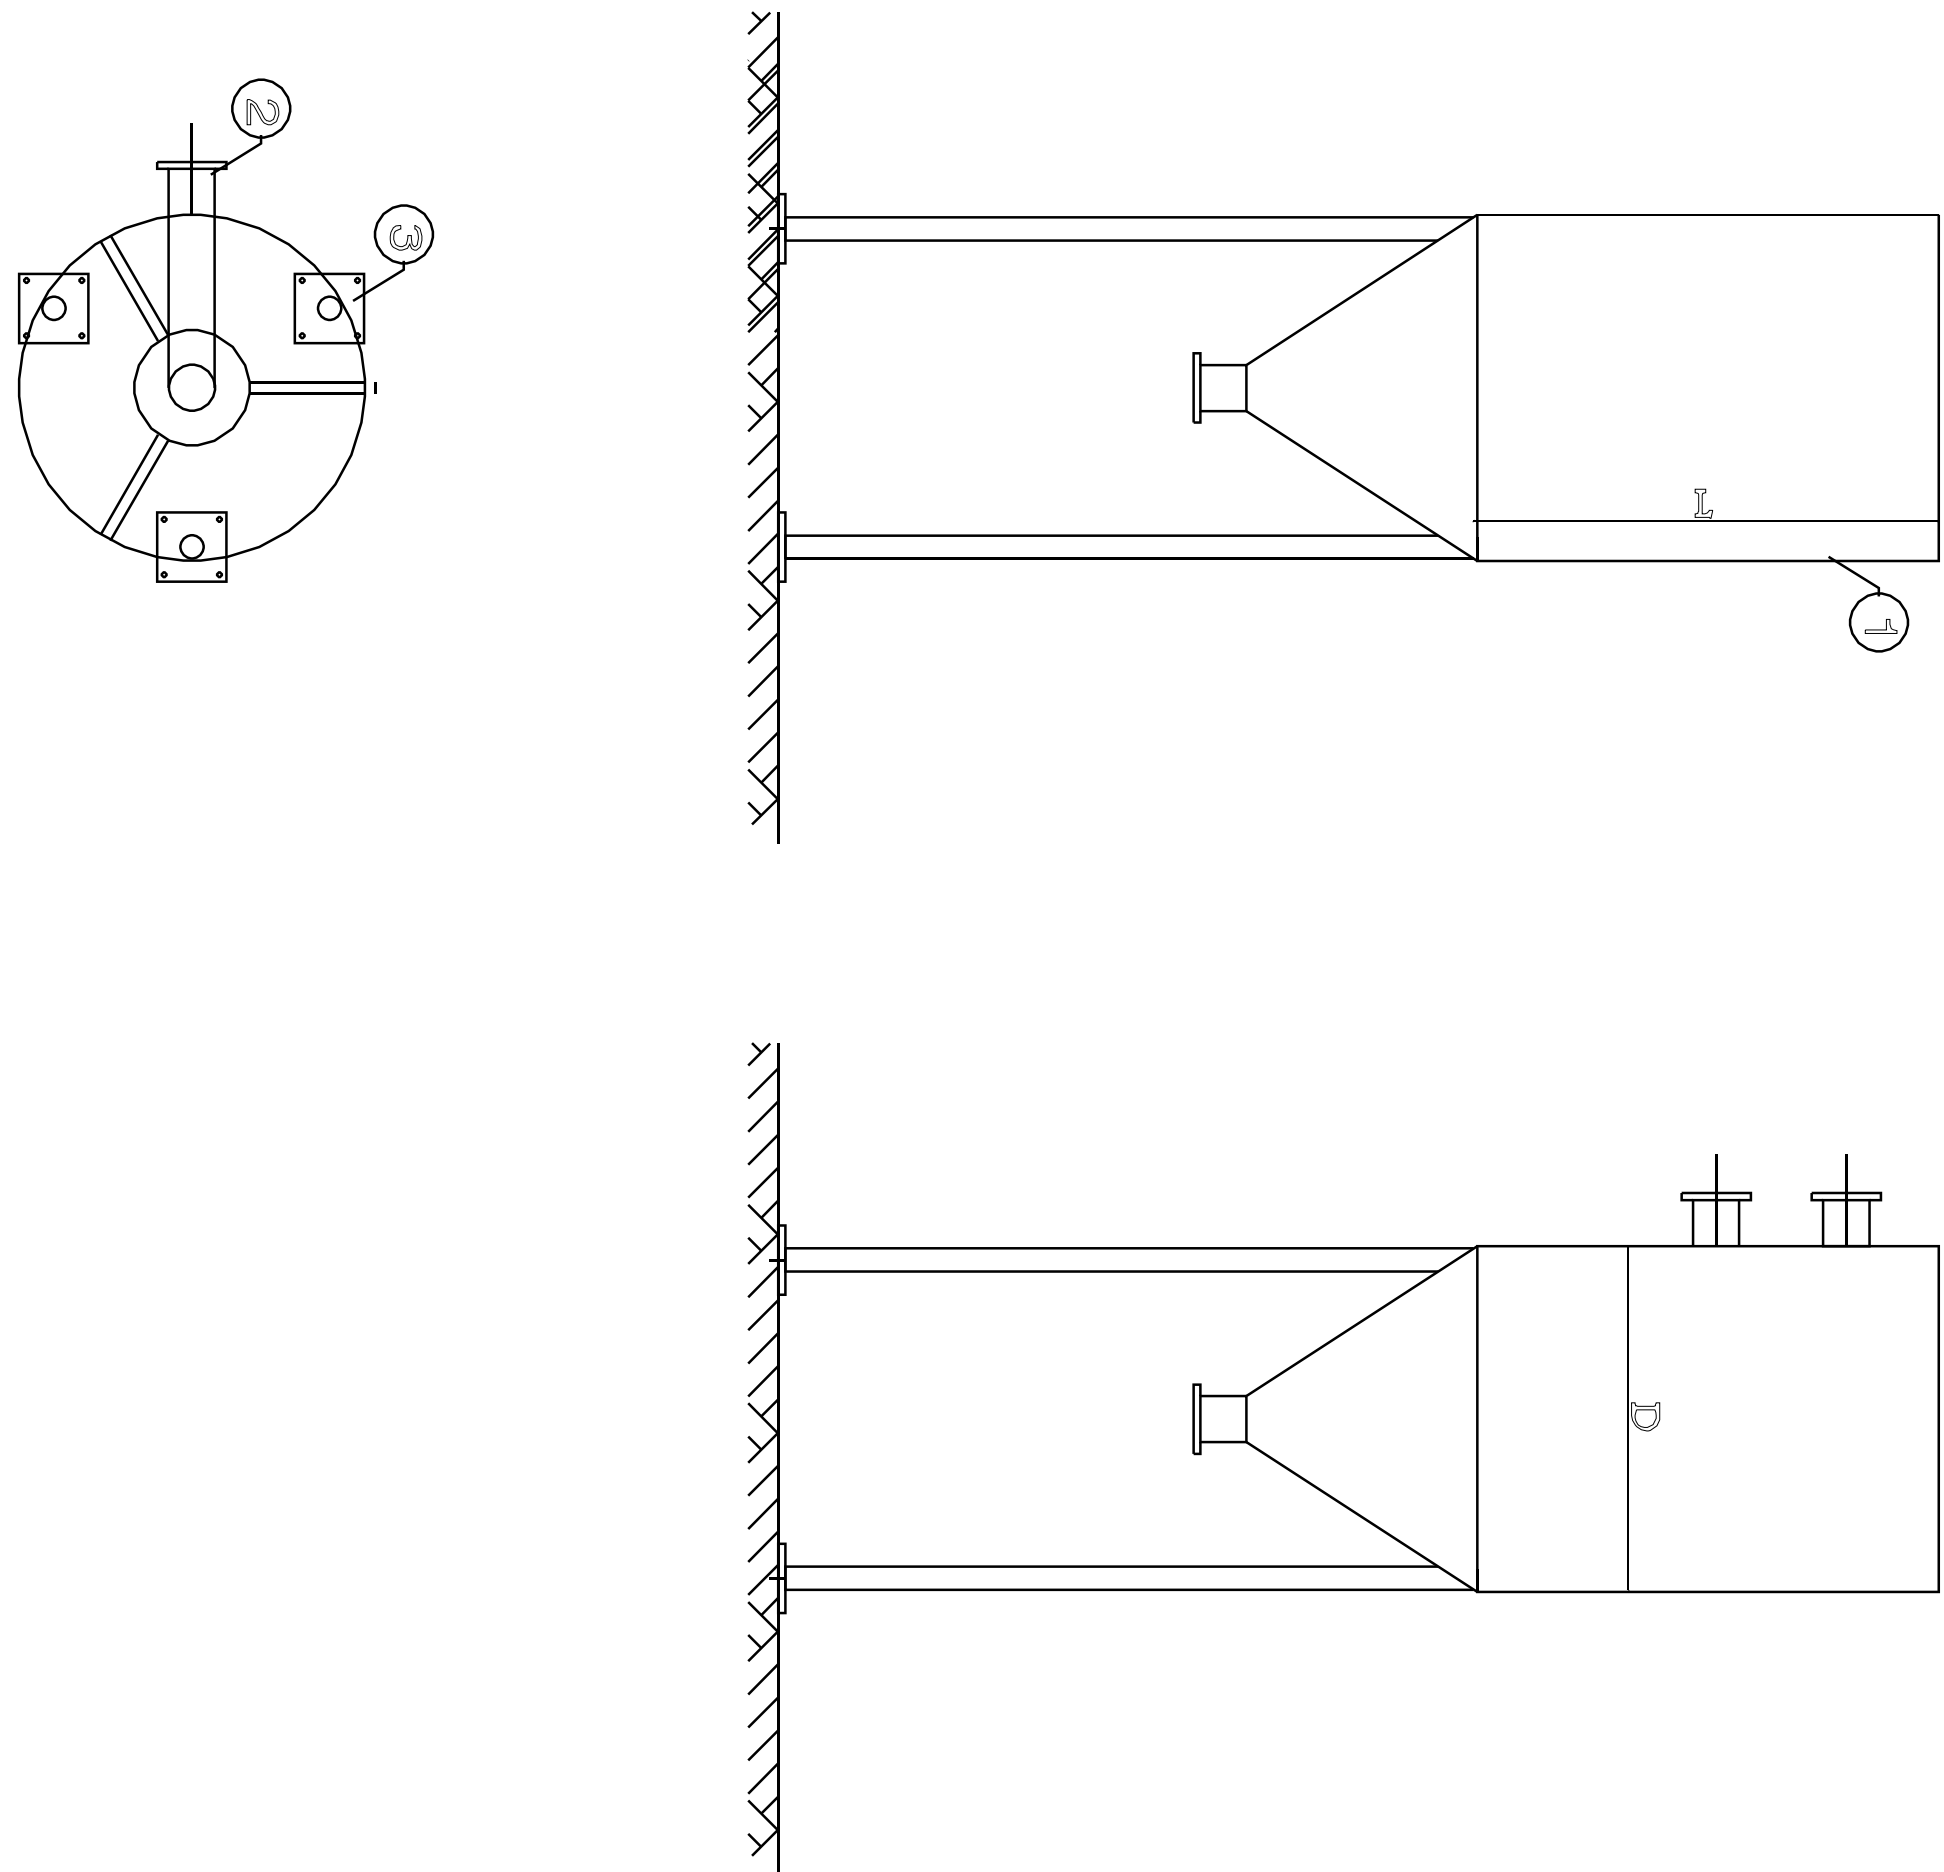

NOTES

7	Level indicator	ST - 37
6	header	ST - 37
5	vent	ST - 37
4	Handrail	ST - 37
3	Leg pipe 3"	ST - 37
2	Inlet pipe 200 mm	ST - 37
1	Cylinder 6 m	ST - 37
Item	Description	Material

[illegible]



Z.C.E

EIZAHRAA FOR ENGINEERING CONTRACTING AND Supplying

شركة الزهراء
للمقاولات الهندسية
والتوريدات

7. Belt Conveyor









Z.C.E

شركة الزهراء
للمقاولات الهندسية
والتوريدات

EIZAHRAA FOR ENGINEERING CONTRACTING AND Supplying

Manufacturer	Winkel
Quantity	1
Width	800
Length	2000
Trade Mark	SEW
Model	SA57T
Trade Mark	SEW
Rated Power	0.37 kW
Supply Voltage	380 V, 3 Phases, 50 Hz
Insulation	Class F
Temp Rise	Class B
Ingress Protection	IP65
Frame	Hot deep galvanized steel
Roller	Hot deep galvanized steel
Bolts & Nuts	AISI 304 (A2)
Conveyor	Rubber 10 mm (3Ply cotton/nylon)

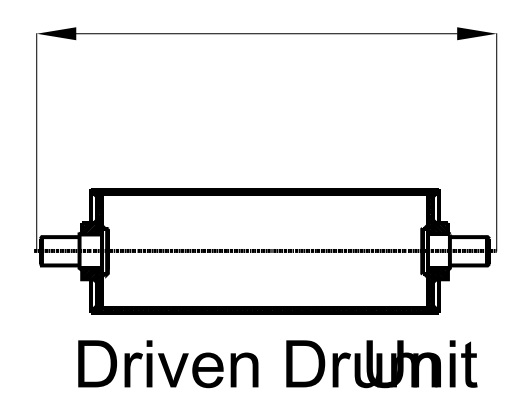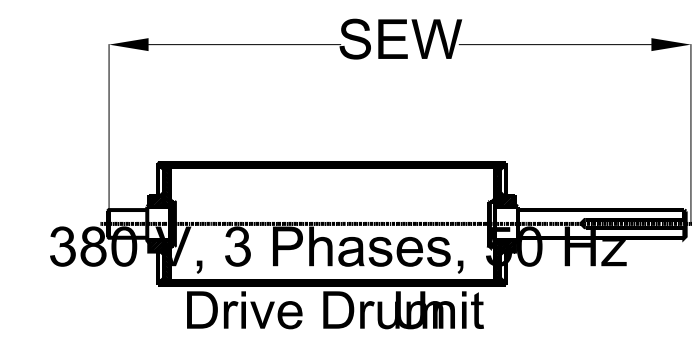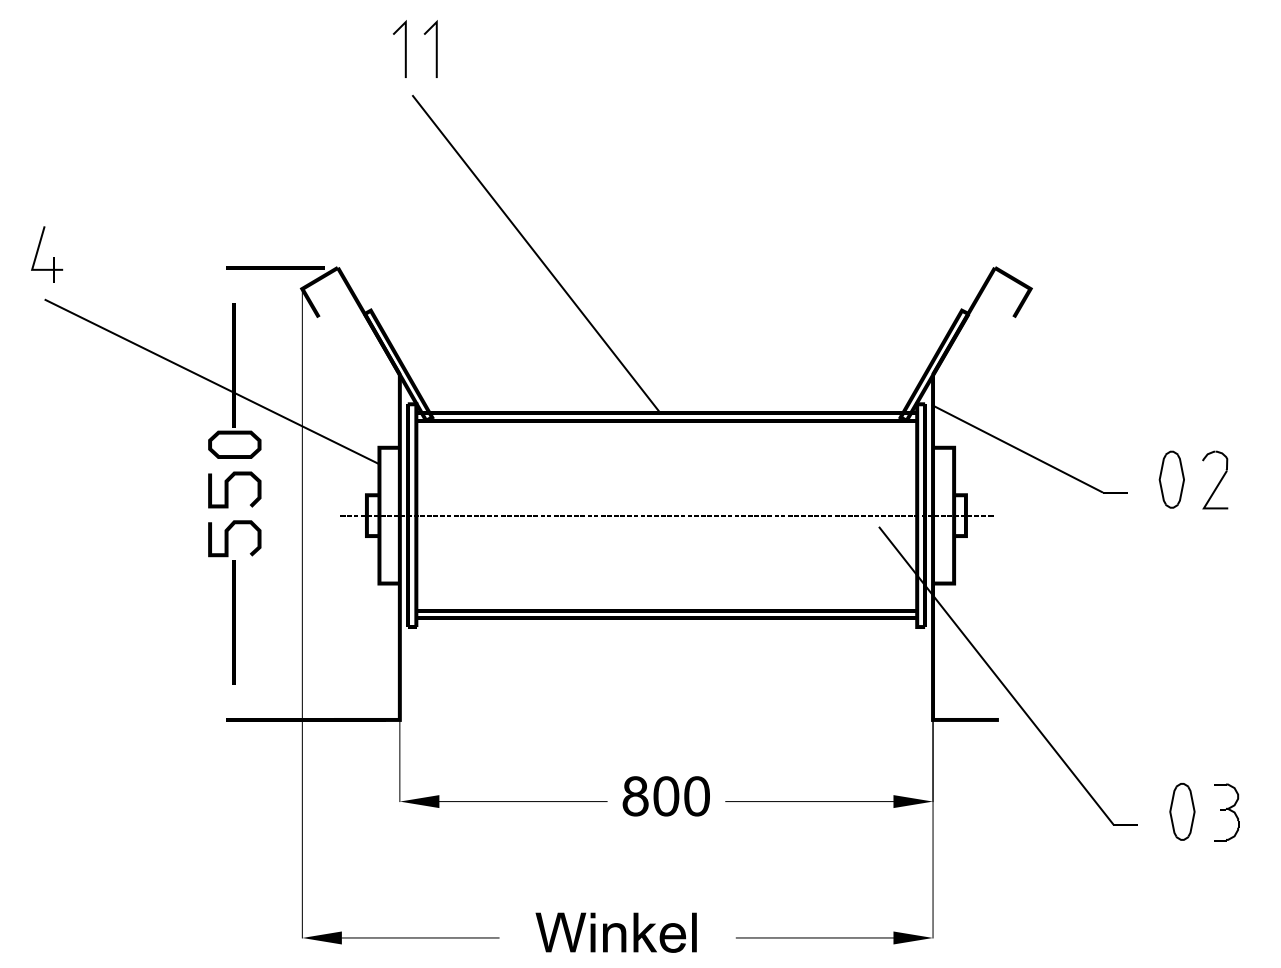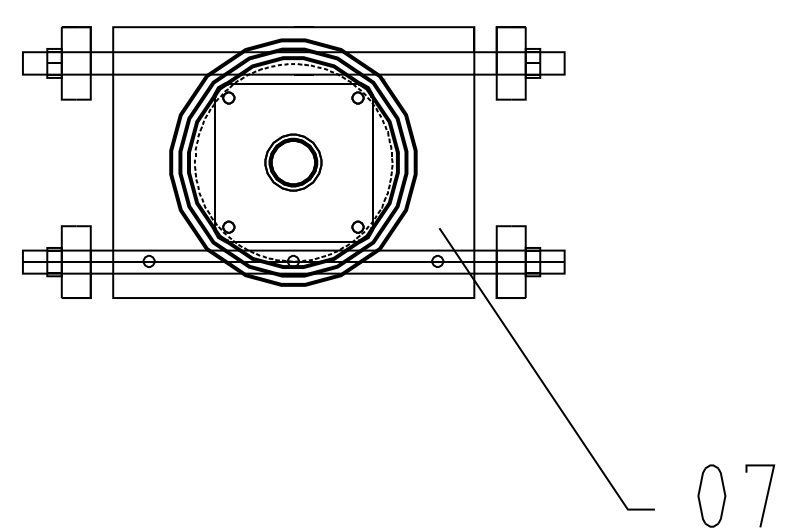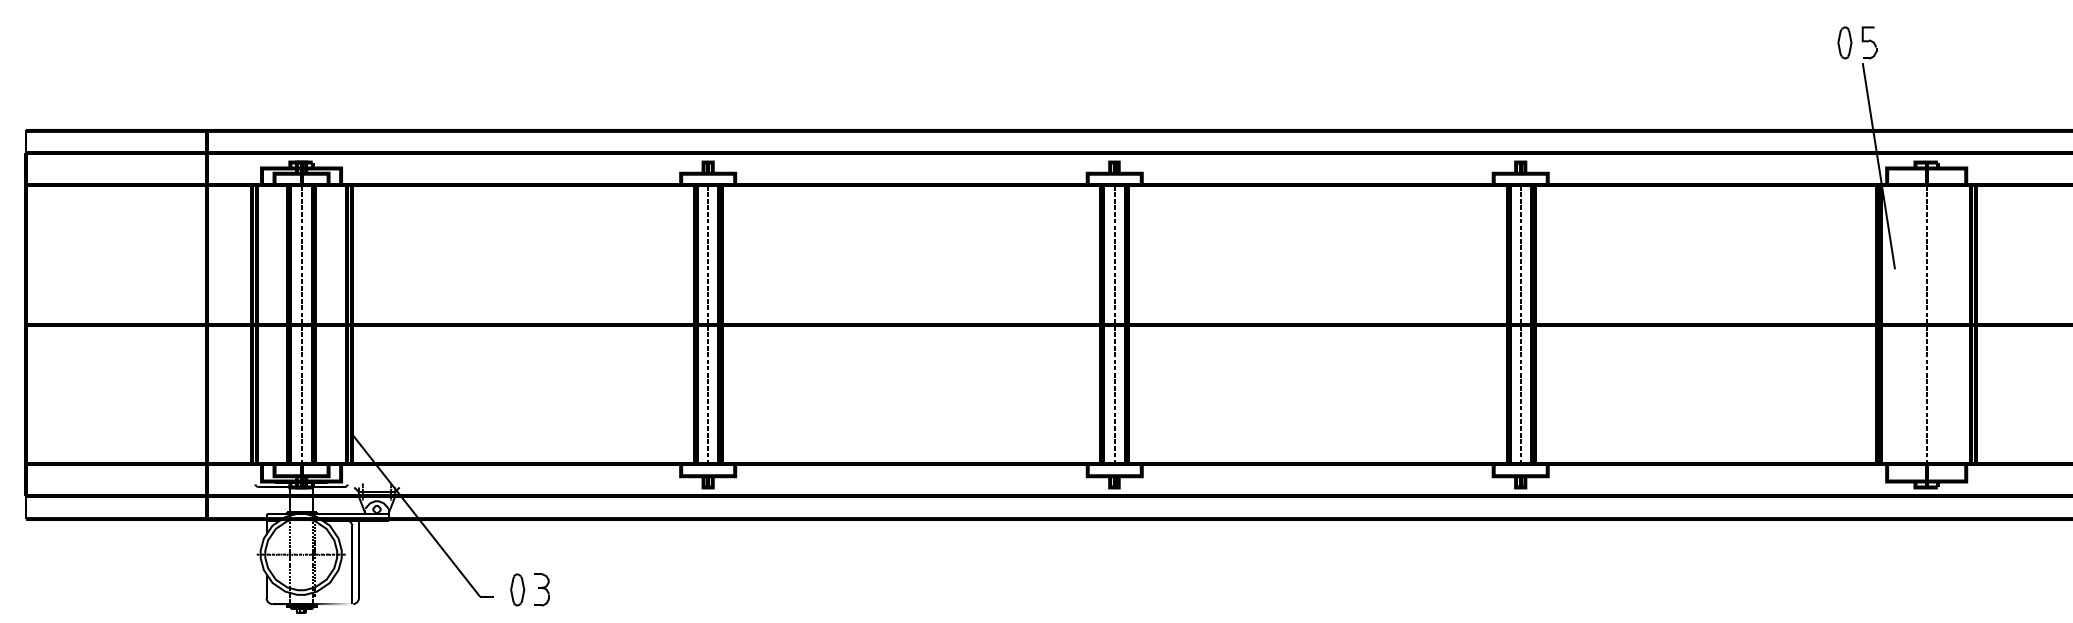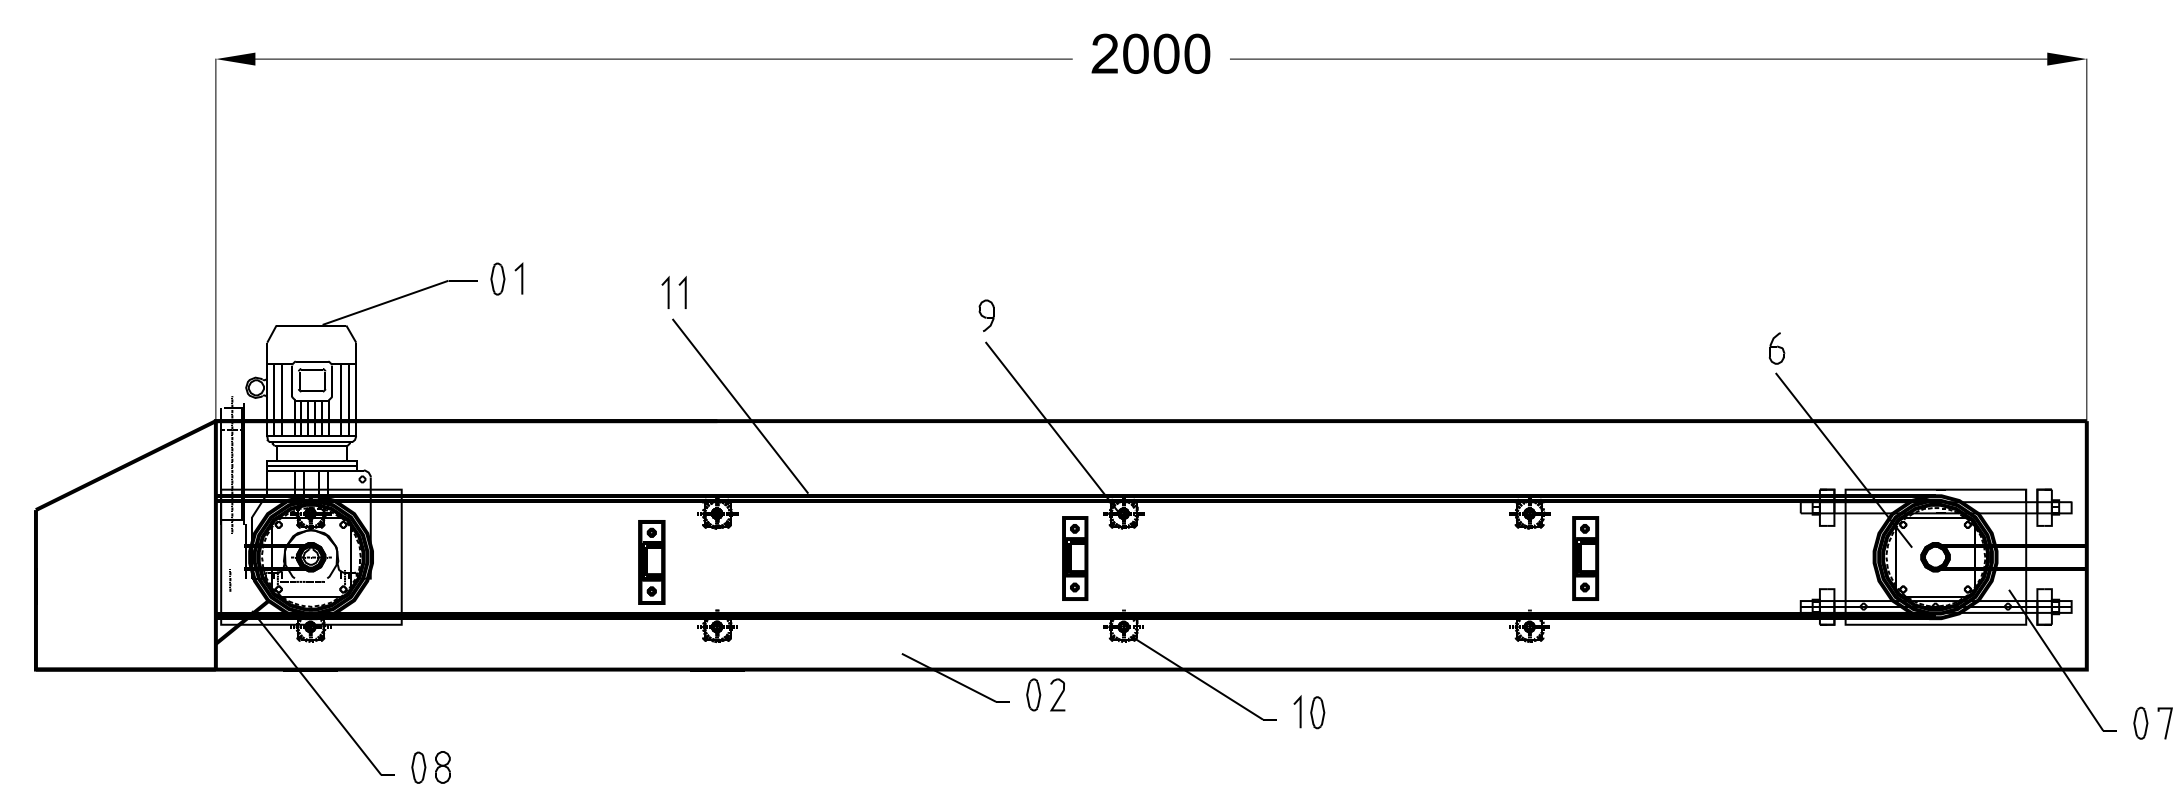

TURN KEY CONTRACTORS:

Z.C.E ELZABRAA
AUTOSATRAD ROAD _ ARAB ABO SAAD _ CAIRO _ EGYPT
elzabaraa.sag2014@gmail.com

TITALE

Belt conveyor

SCALE	REF. DWG. NO.	SIZE	REV.
DRAWN	PREPARED	CHECKED	APPROVED
K.T	A.S	A.S	S.MICHAEL



Z.C.E

EIZAHRAA FOR ENGINEERING CONTRACTING AND Supplying

شركة الزهراء
للمقاولات الهندسية
والتوريدات

8. Mechanical Screen



Z.C.E

شركة الزهراء
للمقاولات الهندسية
والتوريدات

EIZAHRAA FOR ENGINEERING CONTRACTING AND Supplying

Manufacturer	Factory
Quantity	1
Type	Multi tack
Flow	0.11 m3/sec
No. of Rake	3
Width	580 mm
Length	3000 mm
Dead plate	4 mm
Space between bars	25 mm
Bar Type	Rectangular
Bar section	10x20 mm
Inclination	75 Deg
Gearbox Trade mark	SEW
Model	SA77/T
Electric Motor Trade Mark	SEW
Rated Power	0.18 kW
Supply Voltage	380 V, 3 Phases, 50 Hz
Insulation	Class F
Temp Rise	Class B
Ingress Protection	IP65
Local control panel	Electrostatic painting
Panel thicknesses	2 mm
Protection	IP 54




Z.C.E

شركة الزهراء
للمقاولات الهندسية
والتوريدات

EIZAHRAA FOR ENGINEERING CONTRACTING AND Supplying

Component	Schneider
Operation	Manual / Automatic timer switch
Material of Frame & Guide	AISI 316
Dead plate	AISI 316
Rake	AISI 316
Bar screen	AISI 316
Sprocket	AISI 316
Motorize shaft	AISI 316
Bolts & Nuts	AISI 316 (A4)
Channel Width	600 mm
Channel Depth	1180 mm

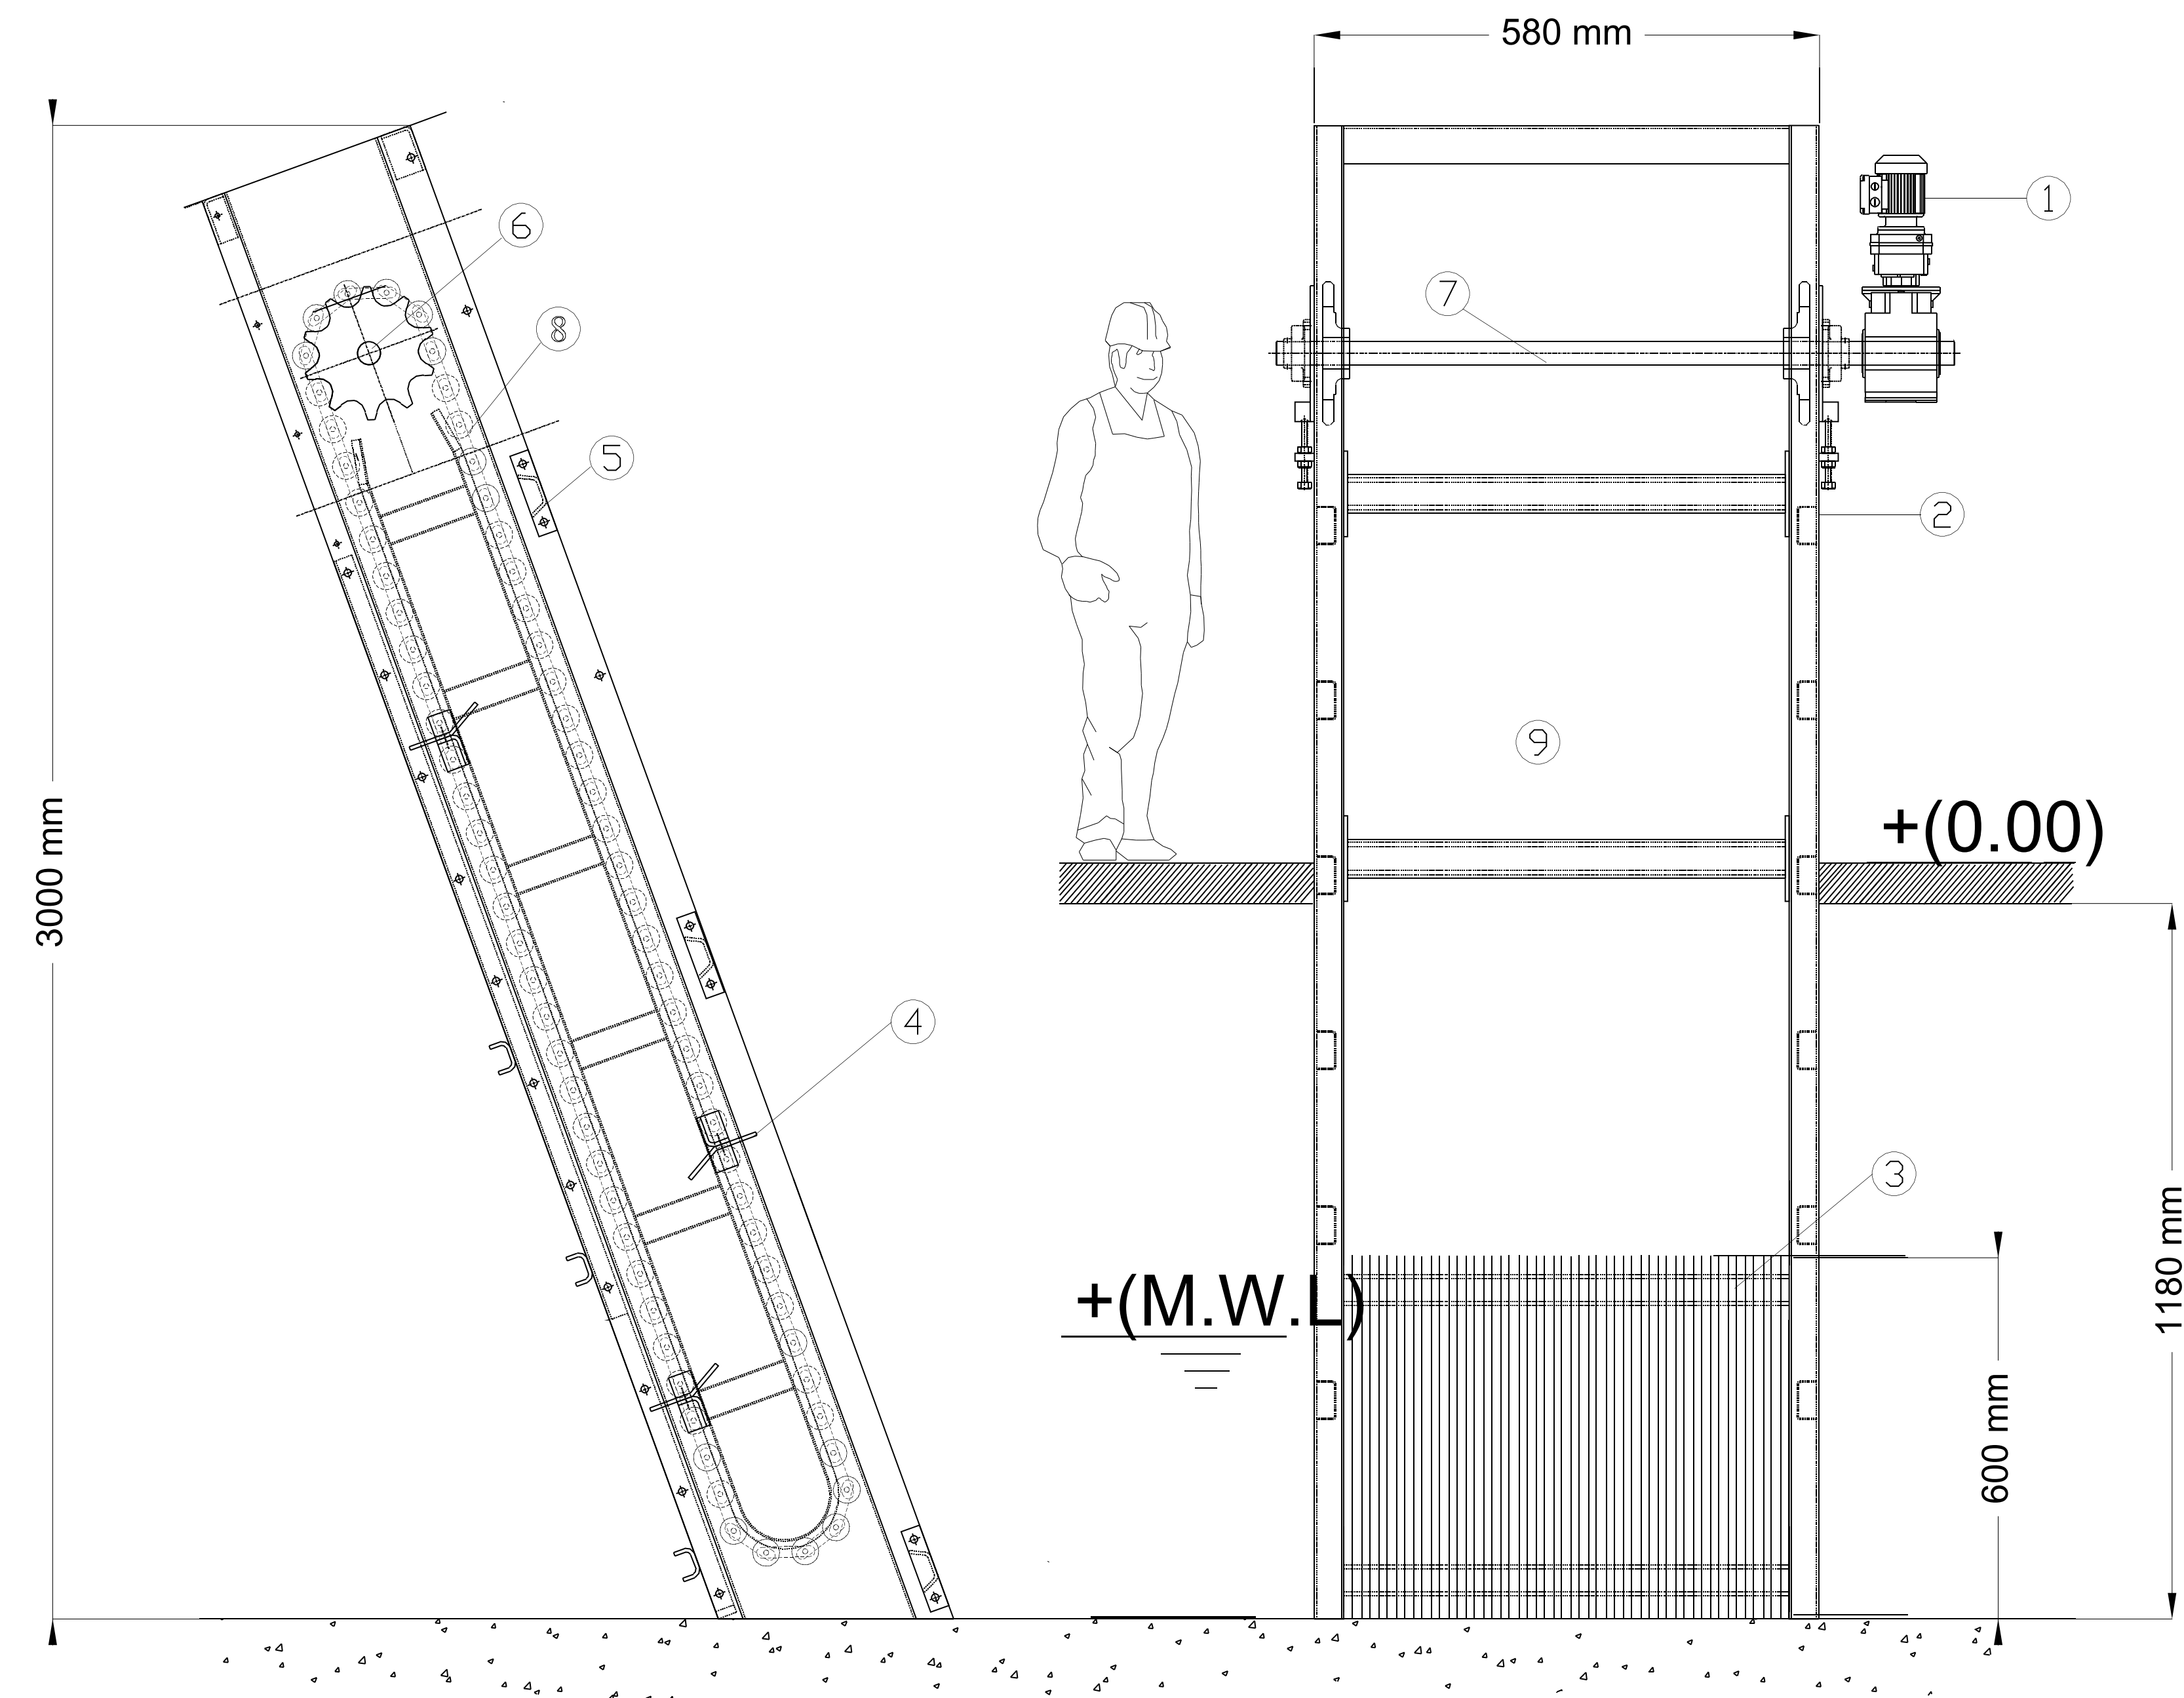

TURN KEY CONTRACTORS:

Z.C.E
AUTOSATRAD ROAD _ ARAB ABO SAAD _ CAIRO _ HELWAN
elzabzaa.sag2014@gmail.com

TITALE

Mechanical screen

SCALE	REF. DWG. NO.	SIZE	REV.
DRAWN	PREPARED	CHECKED	APPROVED
K.T	A.S	A.S	S.MICHAEL



Z.C.E

EIZAHRAA FOR ENGINEERING CONTRACTING AND Supplying

شركة الزهراء
للمقاولات الهندسية
والتوريدات

9. Manual Screen




Z.C.E


شركة الزهراء
للمقاولات الهندسية
والتوريدات

EIZAHRAA FOR ENGINEERING CONTRACTING AND Supplying


Manufacturer	Factory
Quantity	1
Operation	Manual
Flow	0.11 m ³ /s
Width	570 mm
Length	2000 mm
Hand rake	No. 2
Space between bar	25 mm
Bar Type	Rectangular
Bar section	10x30 mm
Inclination	45 Deg
Frame	AISI 316
Rake	AISI 316
Bar screen	AISI 316
Channel Width	600 mm
Depth	1180 mm

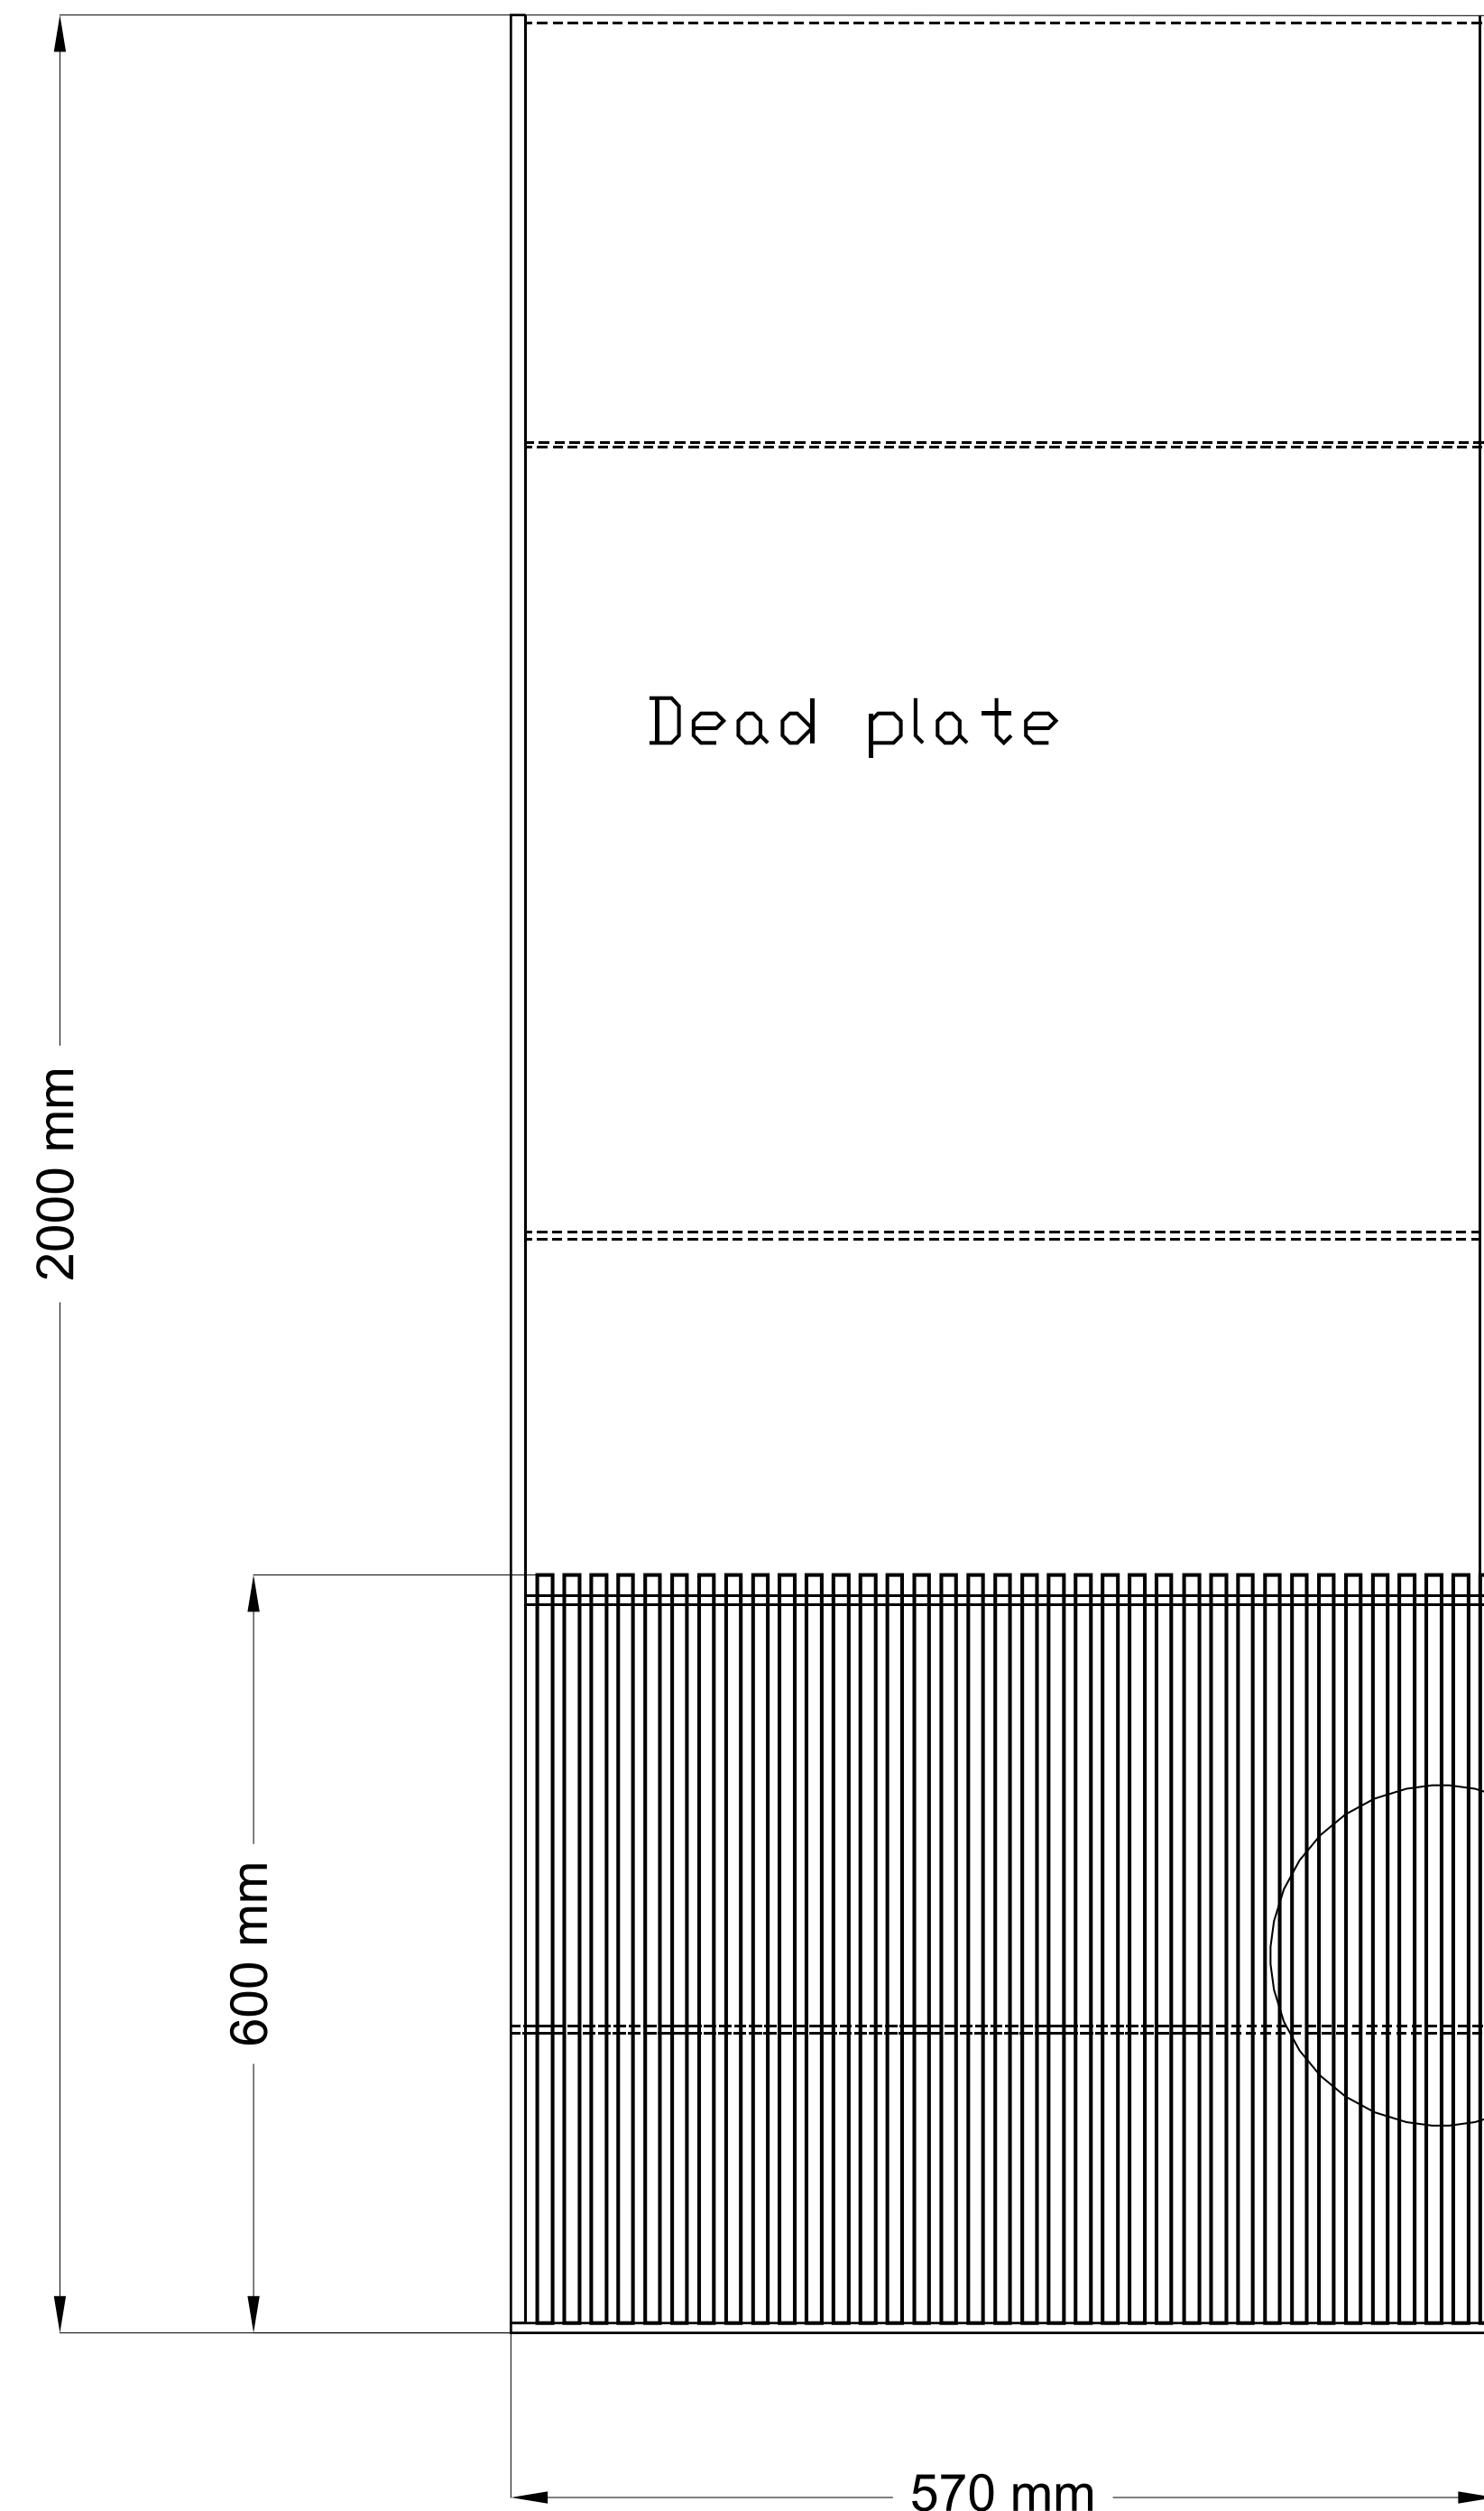

View - A

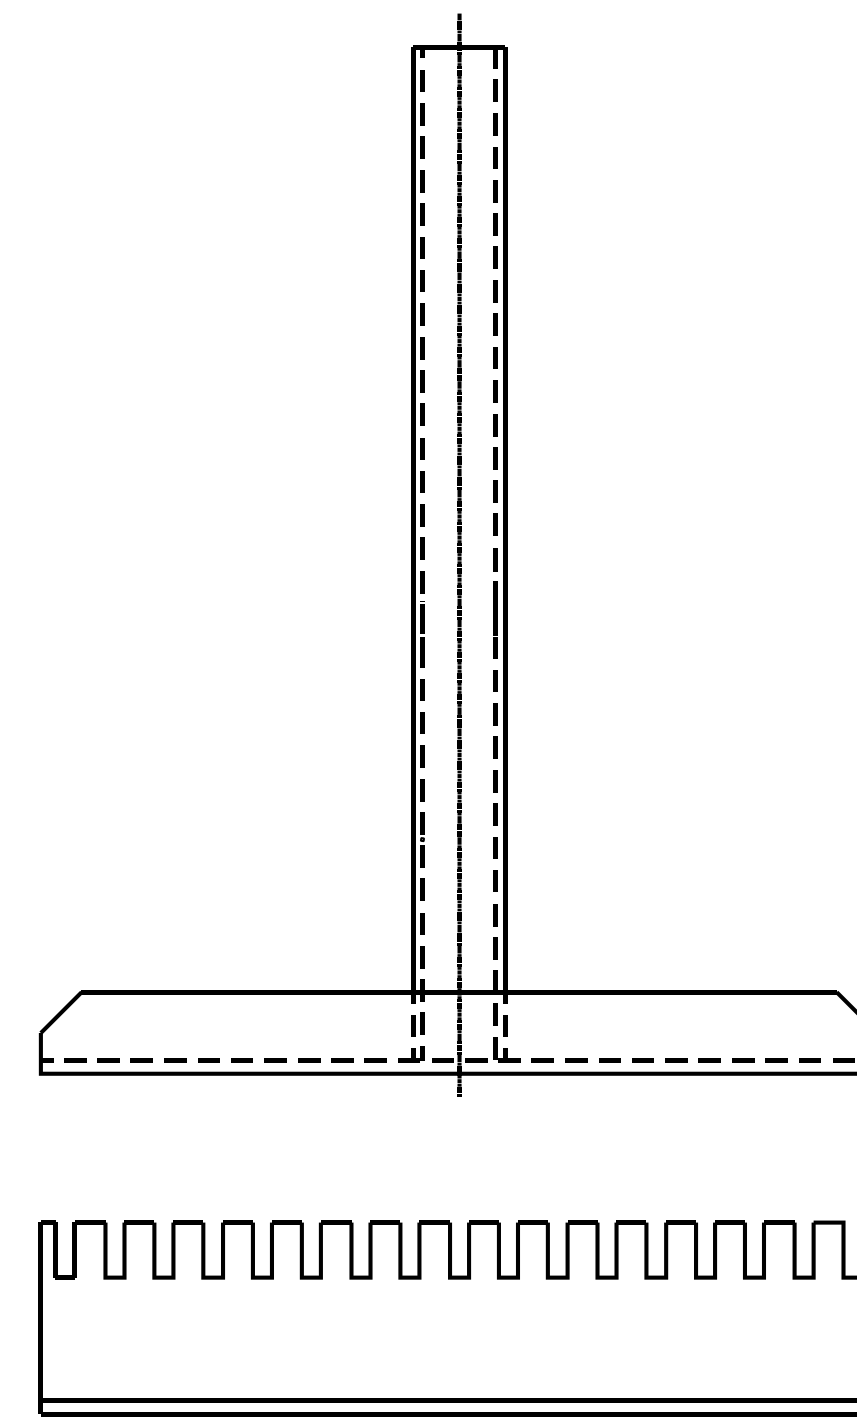

Rack

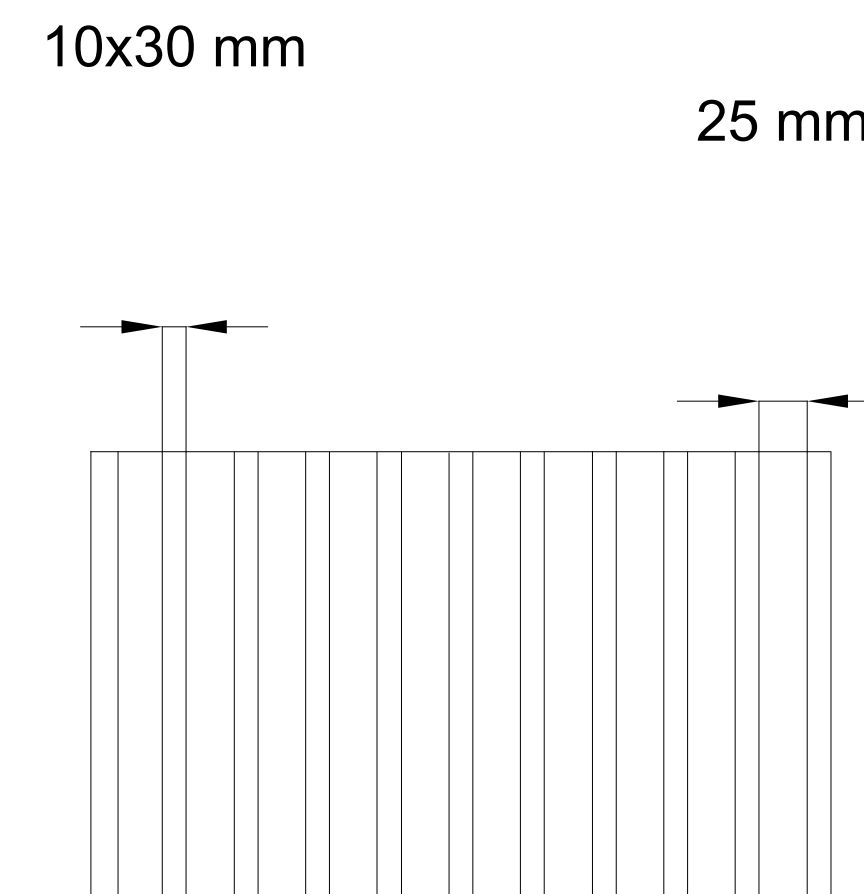

View - A

TURN KEY CONTRACTORS:

Z.C.E ELZABRAA
AUTOSATRAD ROAD _ ARAB ABO SAAD _ CAIRO _ EGYPT
elzabaraa.sag2014@gmail.com

TITALE

Manual screen

SCALE	REF. DWG. NO.	SIZE	REV.
DRAWN	PREPARED	CHECKED	APPROVED
K.T	A.S	A.S	S.MICHAEL