
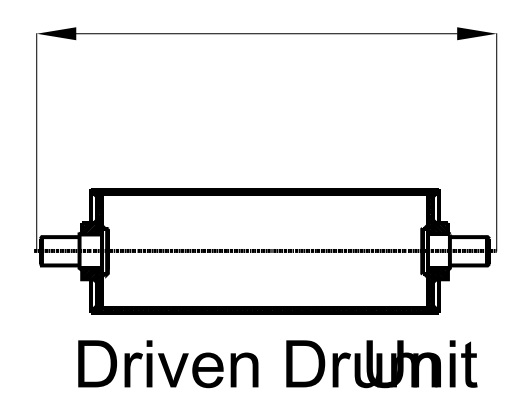
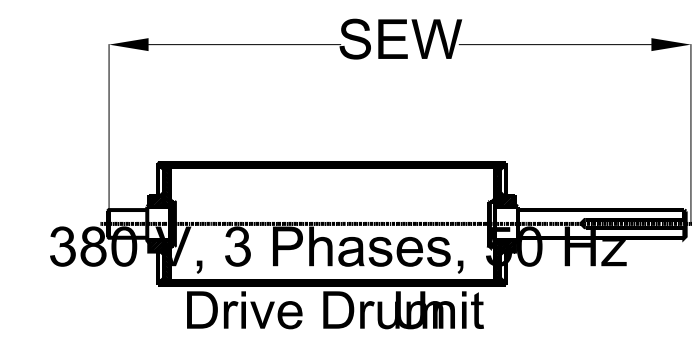
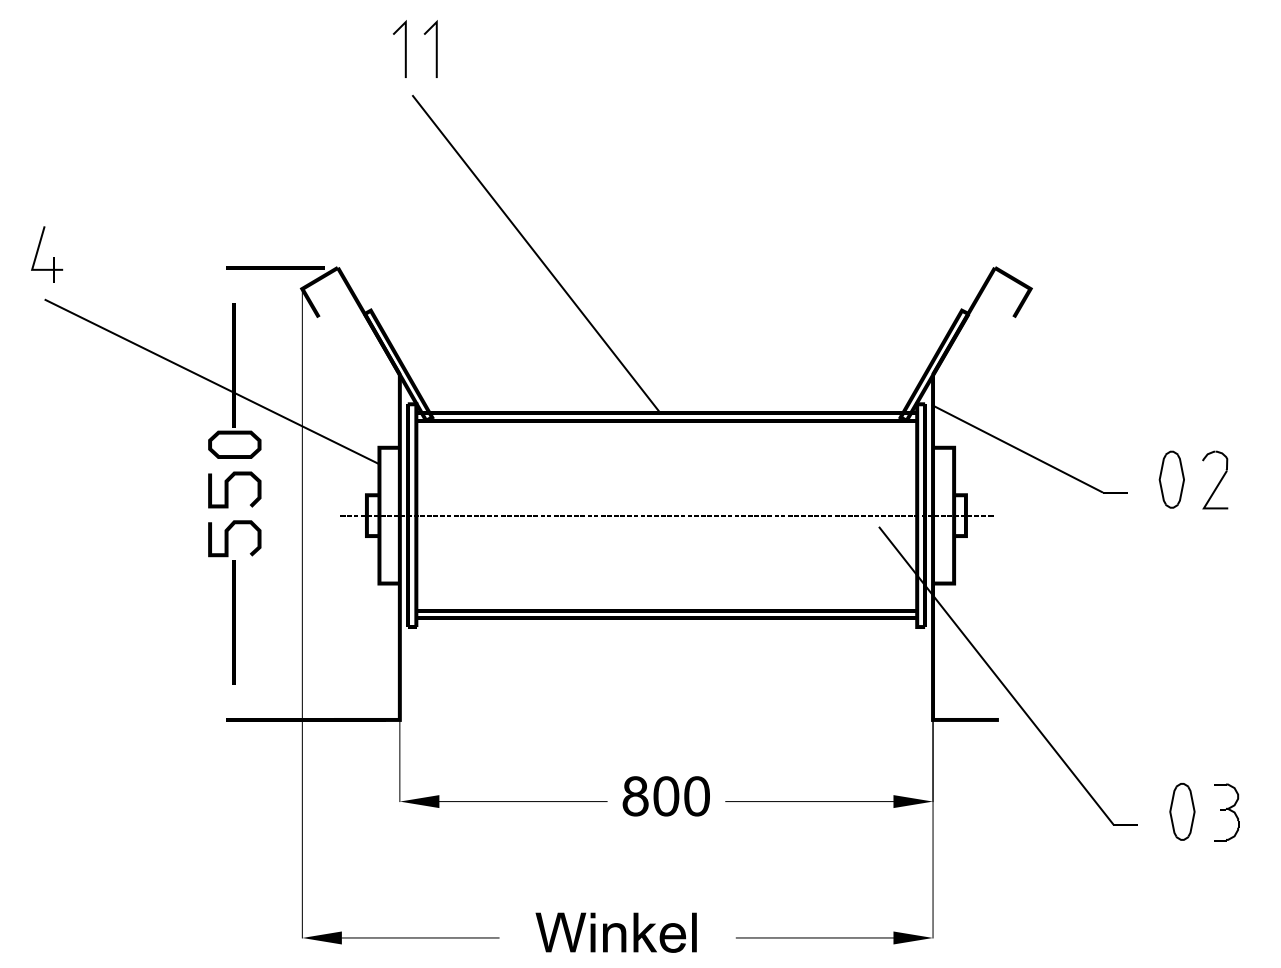
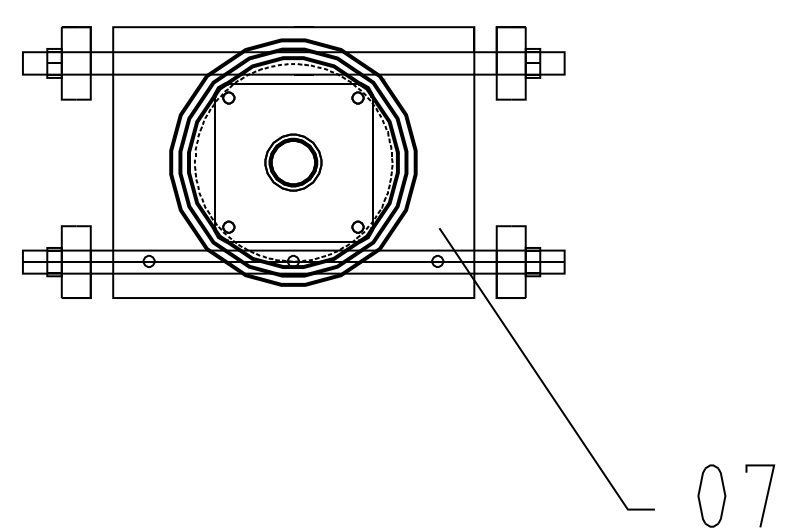
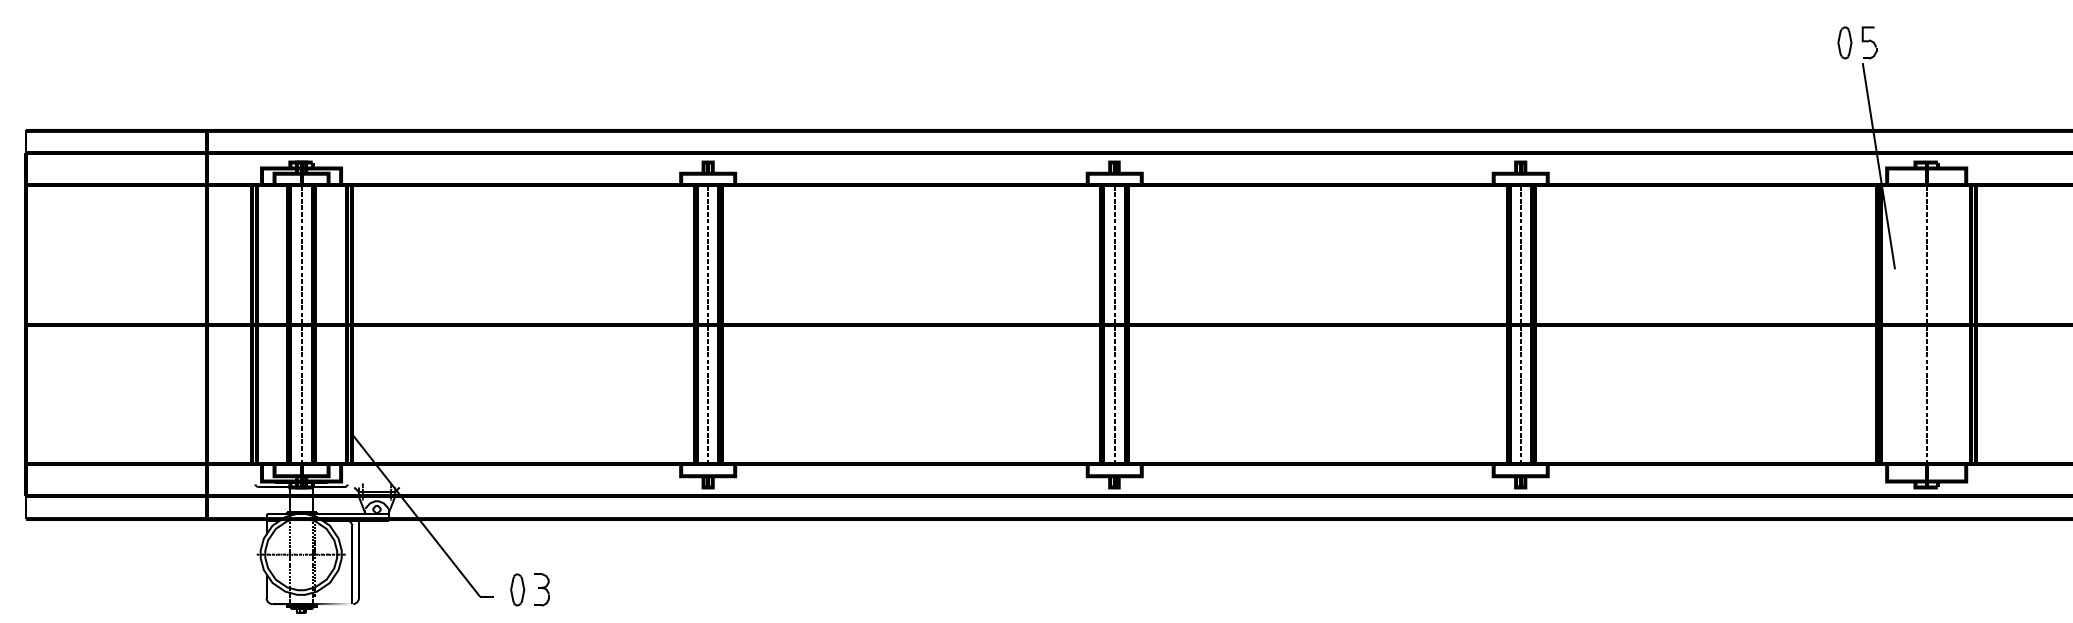


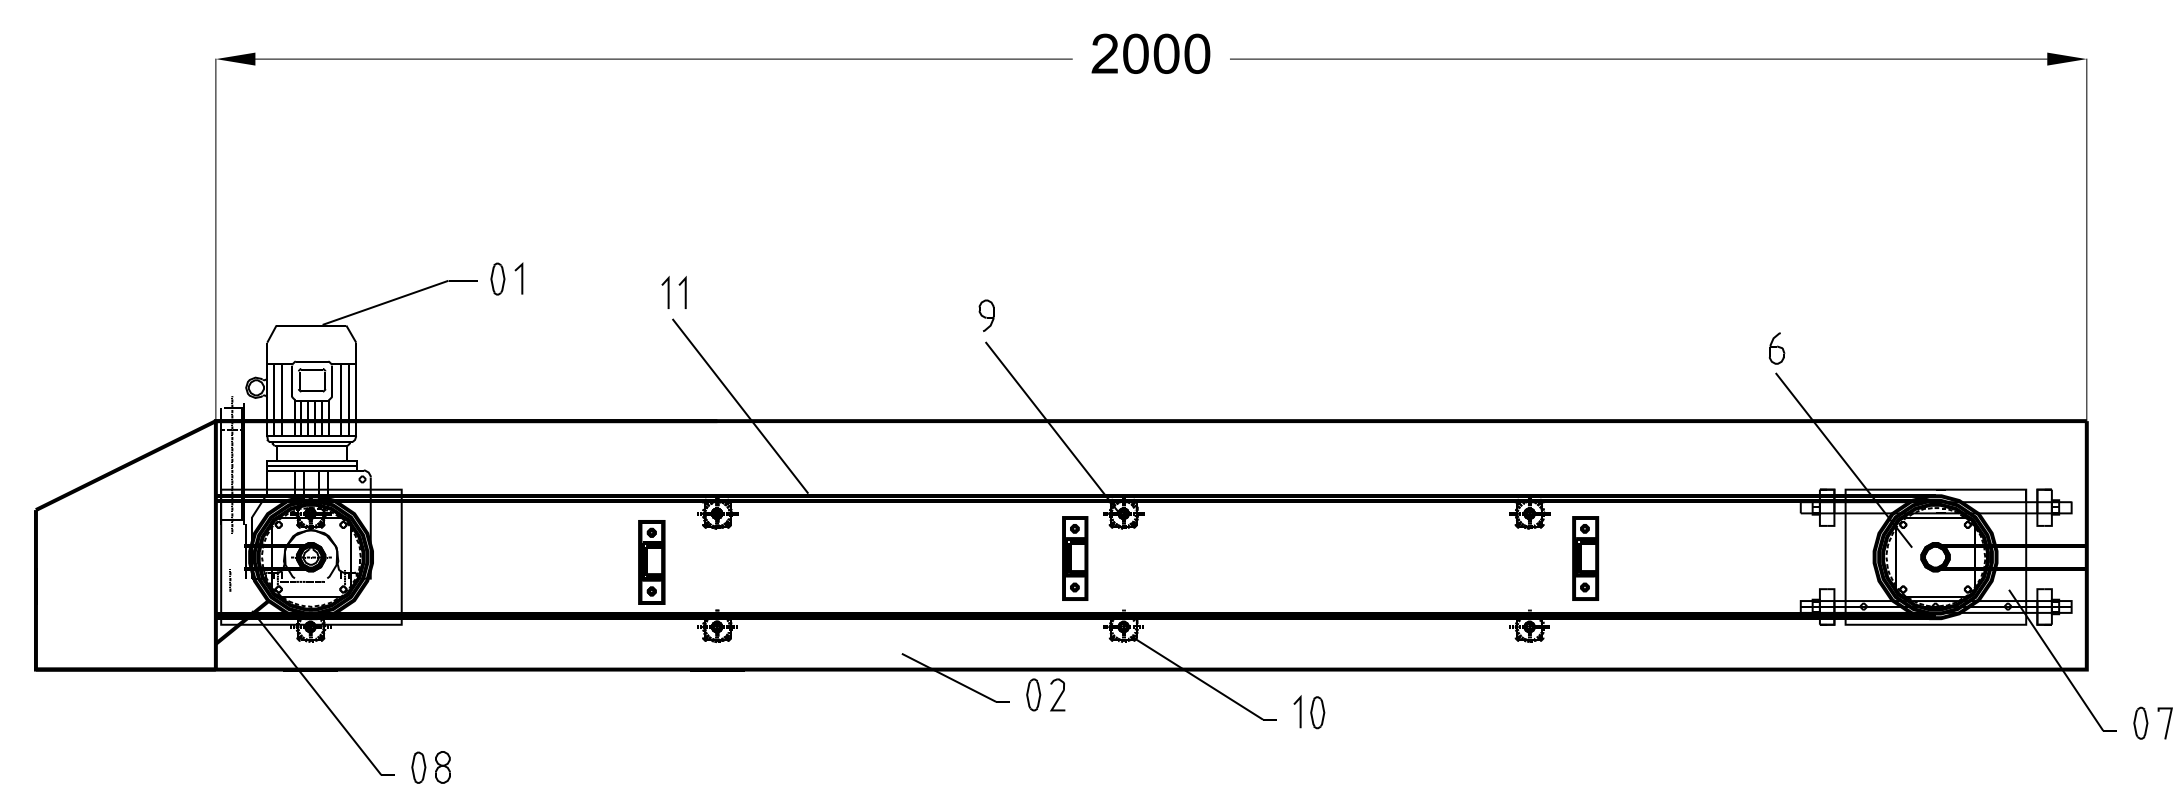

TURN KEY CONTRACTORS:				
Z.C.E ELZABRAA AUTOSATRAD ROAD _ ARAB ABO SAAD _ CAIRO _ EGYPT elzabaraa.sag2014@gmail.com				
TITALE				
Belt conveyor				
SCALE	REF. DWG. NO.	SIZE	REV.	
DRAWN	PREPARED	CHECKED	APPROVED	DATE
K.T	A.S	A.S	S.MICHAEL	