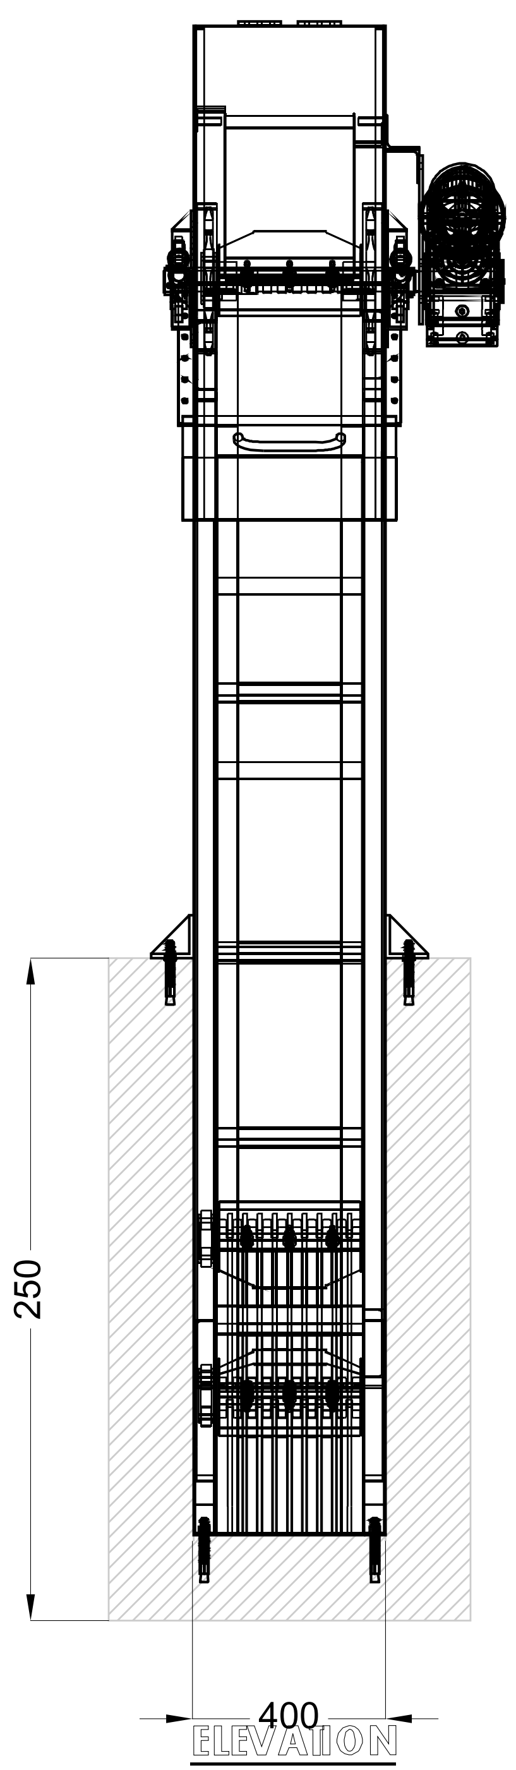

ELEVATION

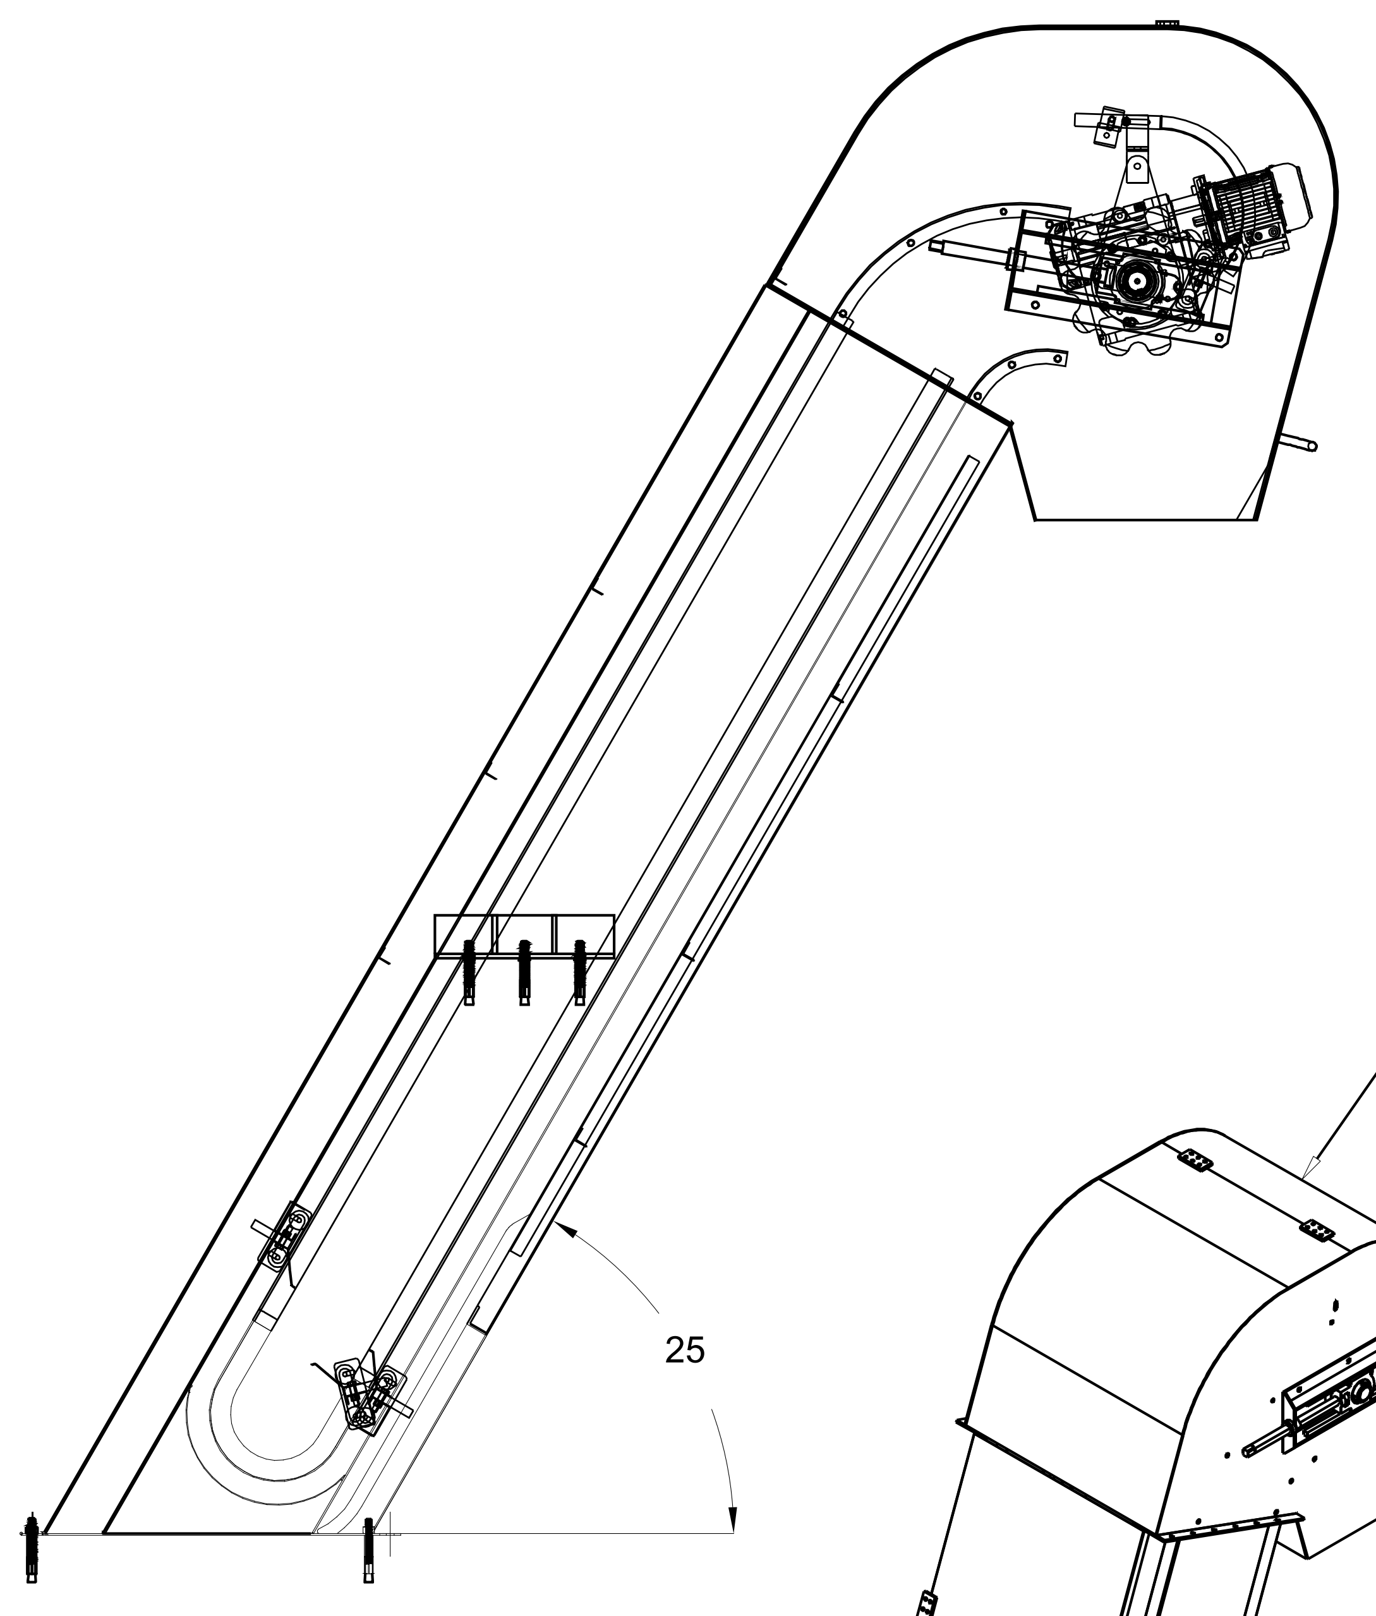

SIDE VIEW

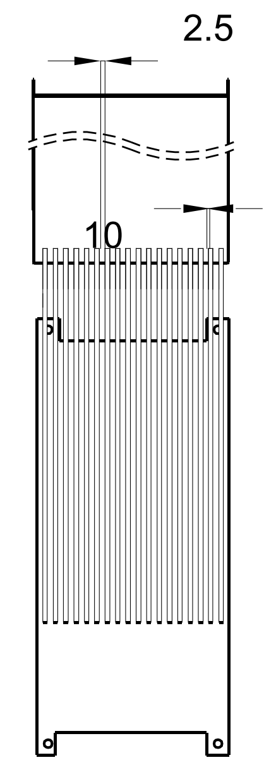

BARS

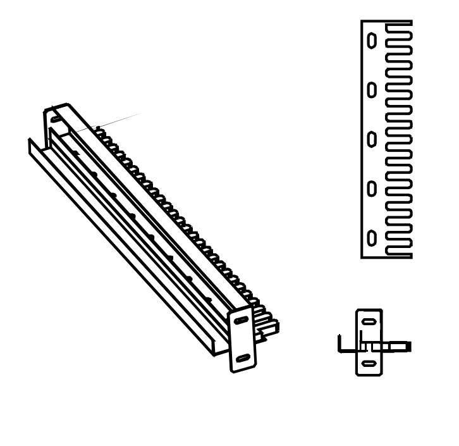

Vertical & Horizontal
Adjustable Rake

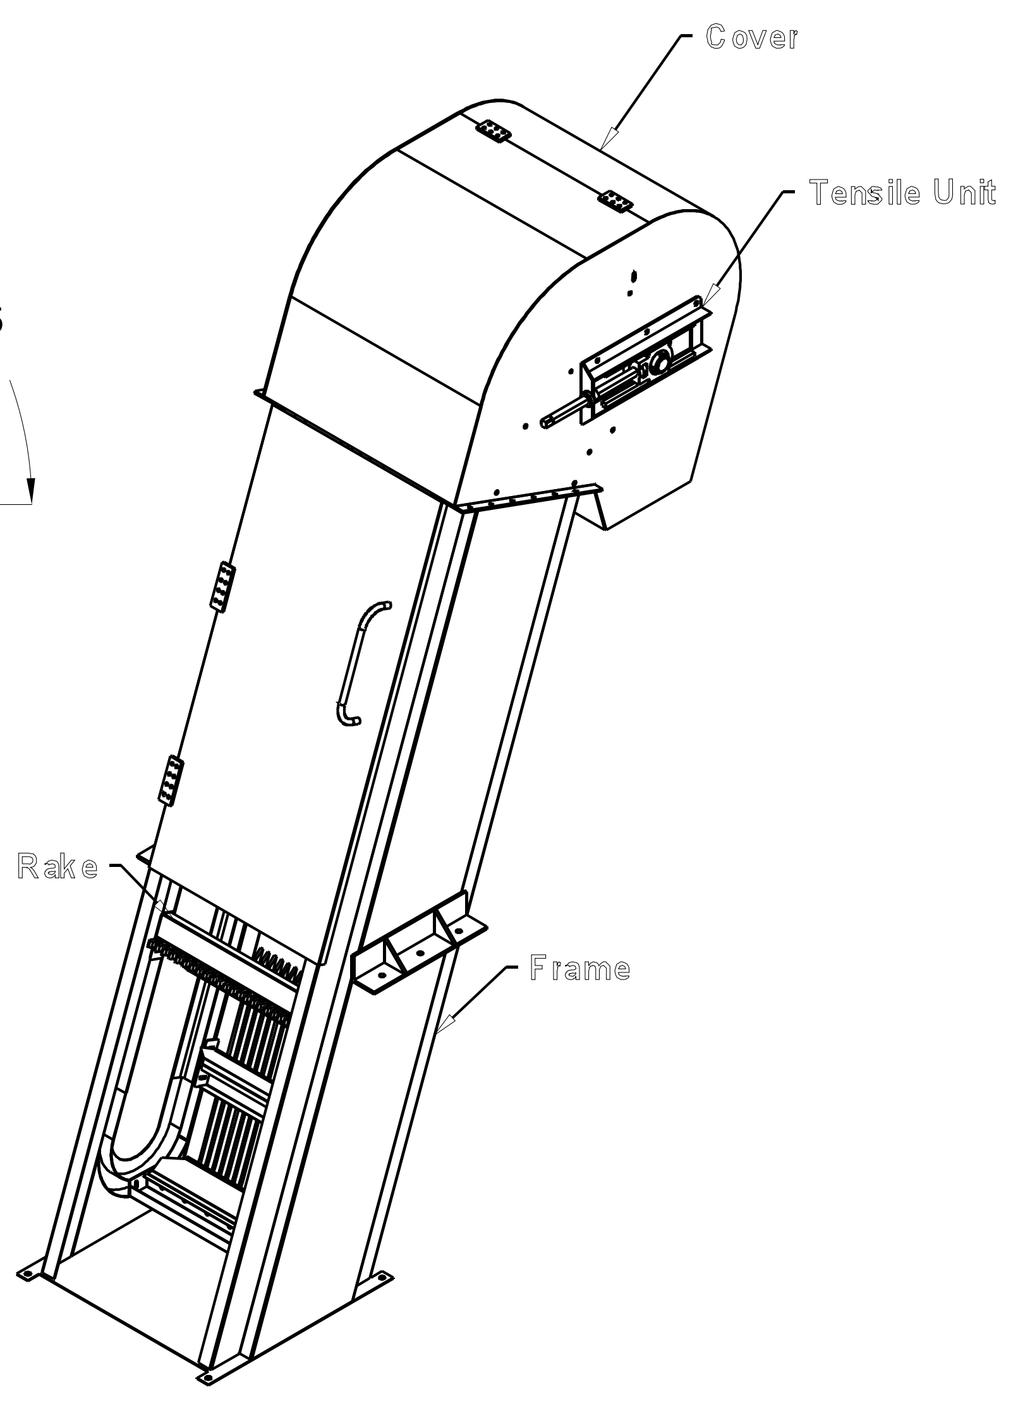

ISOMETRIC

| REV.NO. | DATE | ZONE | REVISION | BY. | APPVD. |
|---|---|---|---|---|---|
| | | | | | |

**General Description**

| | |
|---|---|
| Service | : Inlet Area |
| Type | :Mechanical Coarse Screen<br>Multi rake |
| Channel Depth | : 1500 |
| Channel Width | : 600 |
| Water Depth | : 500 |
| Bar Section | : 12 x 50 |
| Bar Spacing | : 15 |
| Inclination Angle | : 60° |
| Material | : St.St. 304 |
| Qty | : 3 |
| Dimensions | : All Dimensions in mm |

General Tolerance According to DIN 7168-M

| | | | |
|---|---|---|---|
| APPVD. | W.A | | |
| CHKD. | W.F | | |
| DRAWN | D.M | 01/09/2024 | |
| OWNER: | National Organization For Potable Water and Sanitary Drainage "NOPWASD" | | |
| CONSULTANT: | | | |
| MAIN CONTRACTOR: | | | |
| Client | VA TECH WABAG | | |
| CIVIL CONTRACTOR: | | | |
| MANUFACTURER: | The Integrated Environmental Technologies and OilServices Co. S.A.E.<br>5,Heliopolis Company Bldg. Block No. 1226 Tel : + 02 22684645 , + 02 22689889<br>Behind Sheraton Heliopolis Hotel, Airport Road. Cairo, Egypt Fax : + 02 22675150<br>P.O.Box : 2472 Ciaro 11361 E-mail : ietcs@ietcs.com | | |
| PROJECT: | Delga WWTP – Capacity 15000 m3/day<br>El Fashn Center – Beni Suif Governorate | | |
| TITLE: | Mechanical Screen<br>(General Assembly) | | |
| DWG NO. | | SIZE | A3 |
| SCALE | 1:10 | SHEET | 1 OF 1 |
| WELD: | | | |

THIS DRAWING IS FOR OFFER PURPOSE ONLY AND MAY BE CHANGED DURING FABRICATION .